PERFIL LONGITUDINAL TOPOGRÁFICO Y DISTRIBUCIÓN DE ESTRUCTURAS — LÍNEA PRIMARIA 22.9 kV

SECTOR CHIFRÓN, CAPACHICA (PUNO) | CONDUCTOR AAAC 35 mm² | ESCALAS: HORIZONTAL 1:2000, VERTICAL 1:500

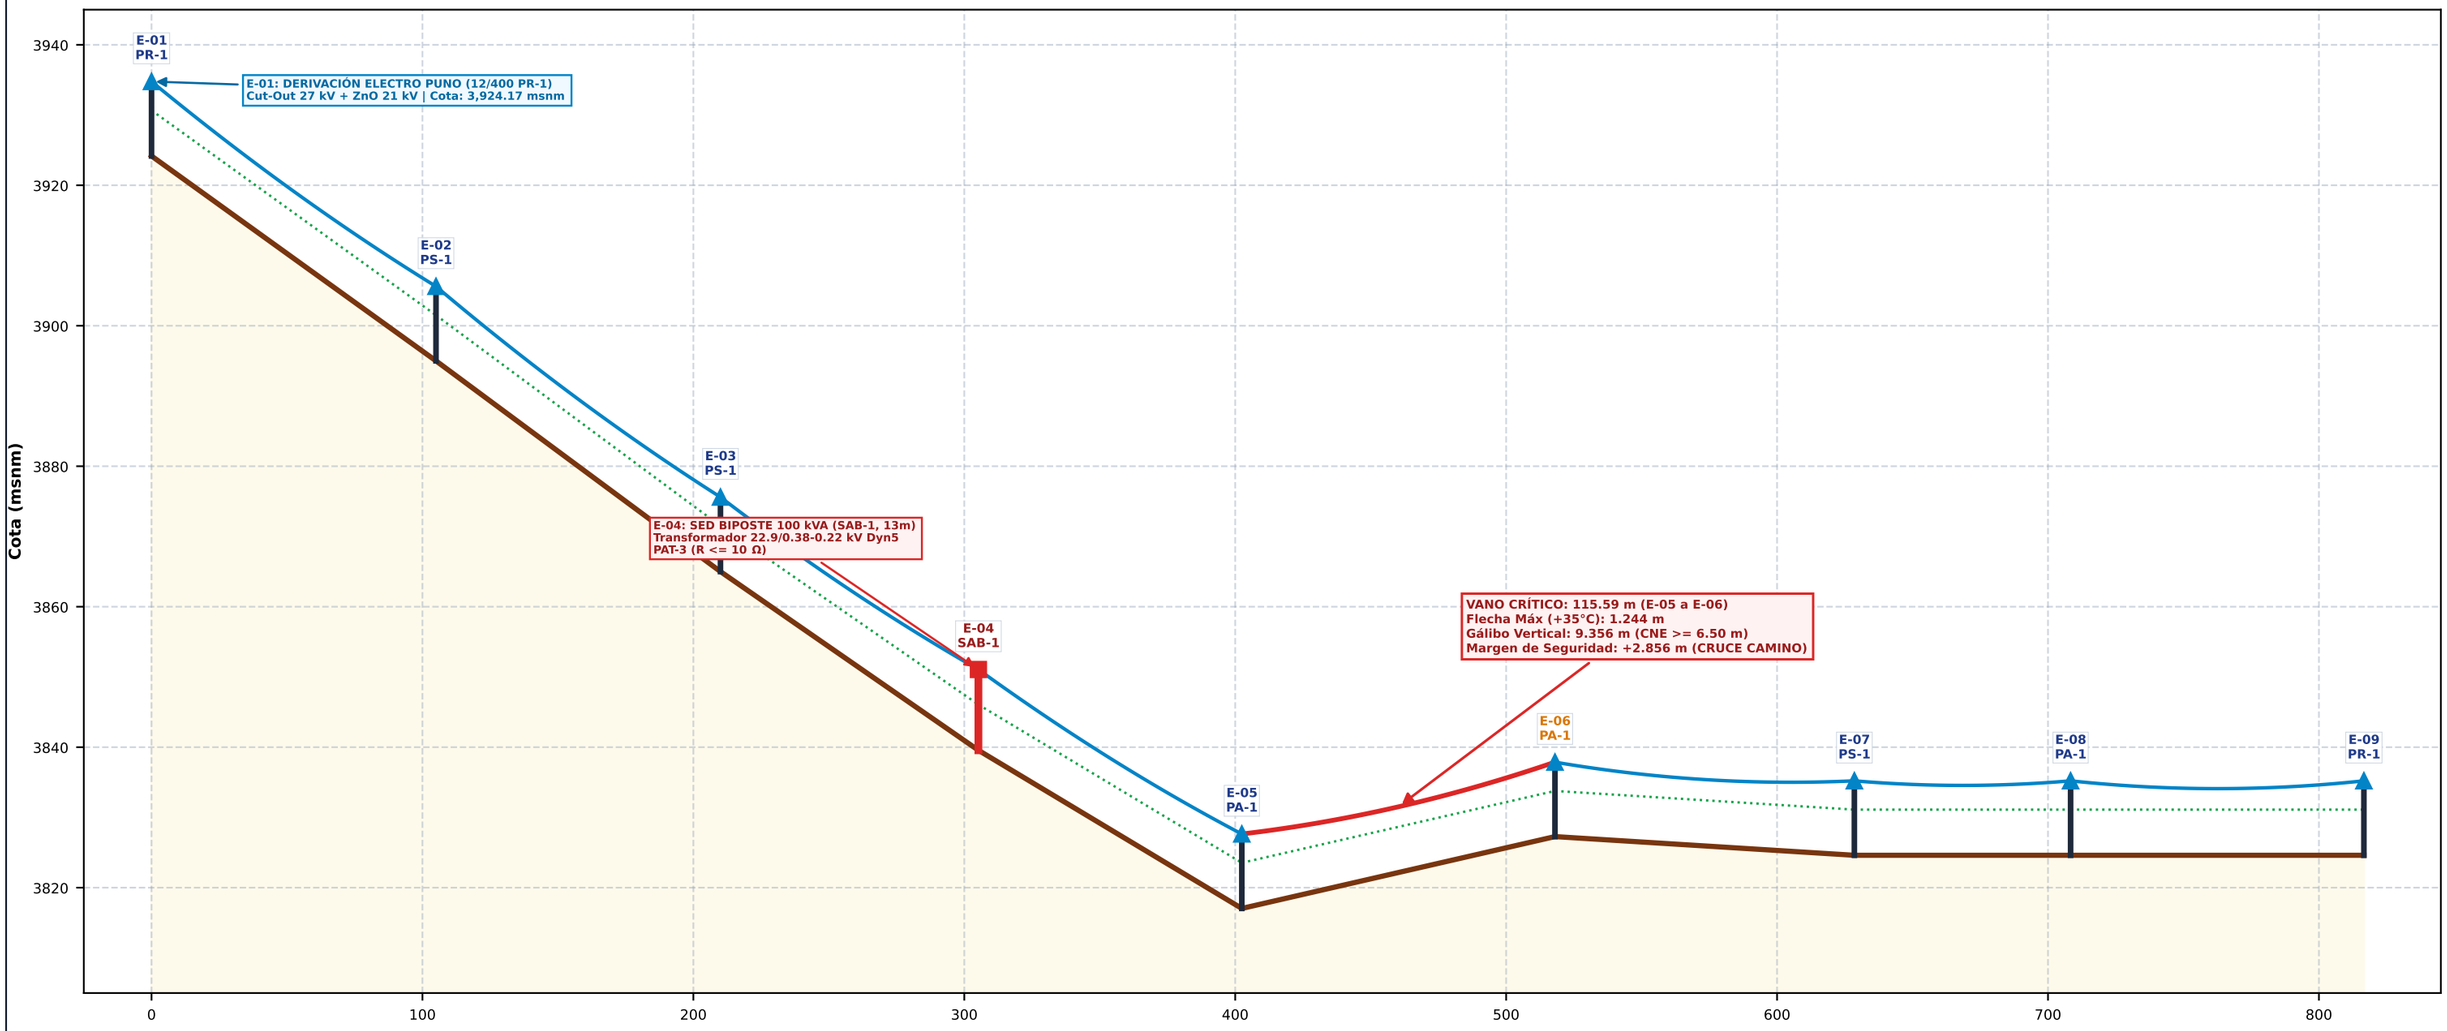

ESTRUCTURA	E-01	E-02	E-03	E-04	E-05	E-06	E-07	E-08	E-09
ARMADO DGE	PR-1	PS-1	PS-1	SAB-1	PA-1	PA-1	PS-1	PA-1	PR-1
POSTE C.A.C.	C.A.C. 12/400	C.A.C. 12/300	C.A.C. 12/300	2xC.A.C. 13/400	C.A.C. 12/400	C.A.C. 12/400	C.A.C. 12/300	C.A.C. 12/400	C.A.C. 12/400
COTA TERRENO (m)	3924.17	3895.00	3865.00	3839.56	3817.04	3827.27	3824.61	3824.61	3824.61
COTA CABEZA POSTE (m)	3934.77	3905.60	3875.60	3851.06	3827.64	3837.87	3835.21	3835.21	3835.21
VANO PARCIAL (m)	---	105.0	105.0	95.2	97.2	115.6	110.5	79.8	108.3
PROGRESIVA (m)	0.00	105.00	210.00	305.21	402.43	518.02	628.53	708.34	816.60
ÁNGULO DESVÍO (°)	+0.0°	+0.0°	+0.0°	-35.2°	-36.1°	+31.4°	-6.0°	+33.0°	+0.0°
RETENIDA / PAT	Inclina / PAT-3	---	---	Contrav / PAT-3	Biselar si	Biselar si	---	Biselar si	Inclina / PAT-3

UNIVERSIDAD NACIONAL DEL ALTIPLANO — PUNO

FACULTAD DE INGENIERÍA MECÁNICA ELÉCTRICA, ELECTRÓNICA Y SISTEMAS

ESCUELA PROFESIONAL DE INGENIERÍA MECÁNICA ELÉCTRICA

ASIGNATURA: MEC330 — INSTALACIONES ELÉCTRICAS II (SEMESTRE 2026-II)

PROYECTO: INSTALACIÓN DEL SISTEMA DE ELECTRIFICACIÓN RURAL

LP 22.9 kV Y REDES SECUNDARIAS SED 100 kVA SECTOR CHIFRÓN (CAPACHICA)

PLANO: PERFIL LONGITUDINAL TOPOGRÁFICO Y DISTRIBUCIÓN DE ESTRUCTURAS LP 22.9 kV

PROYECTISTA: Br. Renzo Gabriel Mamani Galindo (Cód. 228447)

DOCENTES: Ing. Leonidas Vilca Callata / Ing. Marcos José Villanueva Cornejo

FECHA:	ESCALA:	LÁMINA:
Octubre 2026	H: 1/2000 | V: 1/500	PL-01