
NOTAS: Cotas en mm. Ferretería de acero galvanizado en caliente (ASTM A153/A123).
Fase superior a 0,30 m sobre la cabeza; cruceta a 1,40 m bajo la cabeza (conductores inferiores a 1,10 m).
La numeración de los globos corresponde al orden de la lista de materiales.

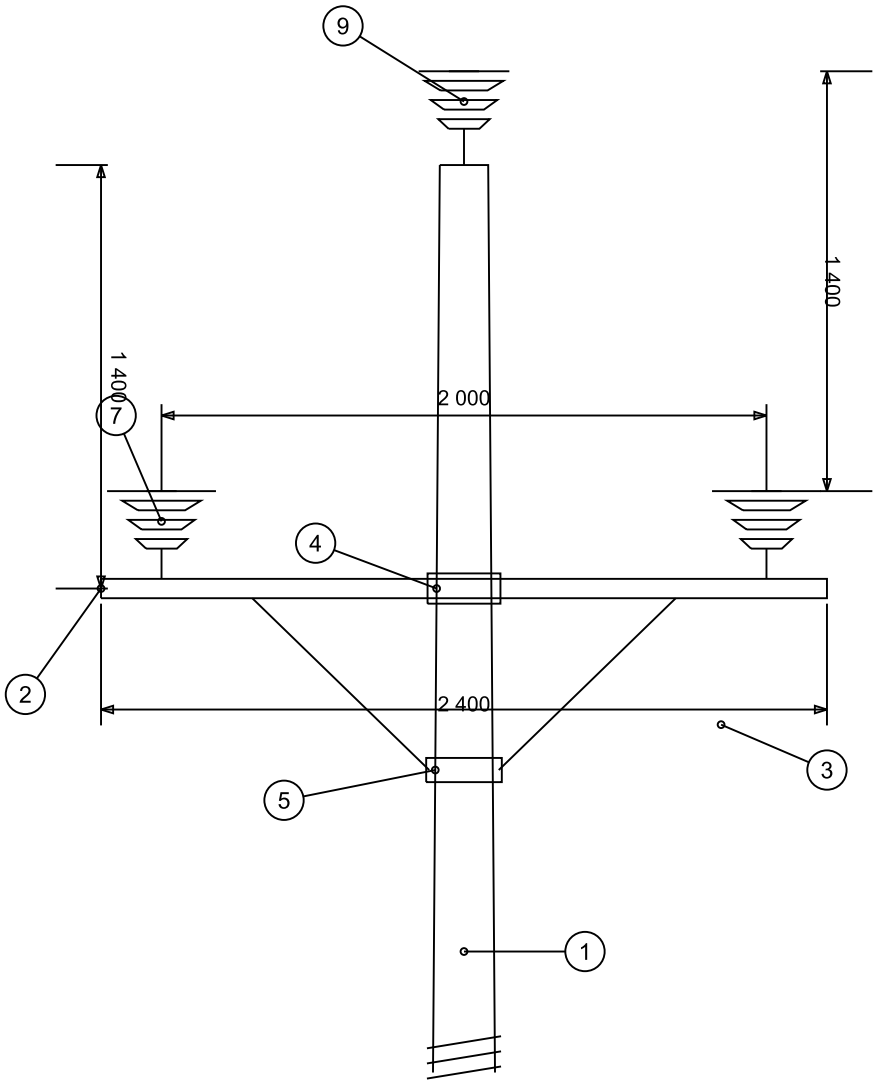

VISTA FRONTAL

LISTA DE MATERIALES

ITEM	DESCRIPCIÓN	UND.	CANT.
1	Poste de C.A.C. 12/300 daN, con perilla	u	1
2	Cruceta de perfil angular FºGº de 64 x 64 x 2400 mm, E = 6,4 mm, con 02 dados. TIPO I	u	1
3	Riostra de perfil angular FºGº de 64 x 64 x 1000 mm, E = 6,4 mm	u	2
4	Abrazadera tipo CAS simple de 75 mm, E = 6,4 mm, D = 206 mm	u	1
5	Abrazadera partida para cruceta de 75 mm, E = 6,4 mm, D = 196 mm, c/2P/2T/2C/4A/2AP	u	1
6	Perno maquinado de AºGº L = 50 mm, D = 13 mm, c/T/C/2A/AP	u	2
7	Perno de AºGº de 16 mm ⌀ x 254 mm, con tuerca y contratuerca	u	2
8	Arandela cuadrada plana de AºGº 57 x 57 x 5 mm, agujero 18 mm ⌀	u	2
9	Aislador de porcelana tipo PIN, clase ANSI 56-4 (línea de fuga 685 mm)	u	3
10	Espiga de AºGº de 609 mm de longitud, para cabeza de poste y aislador ANSI 56-4	u	1
11	Espiga de AºGº para cruceta y aislador ANSI 56-4, de 381 mm de longitud, con accesorios	u	2
12	Varilla de armar preformada simple para conductor AAAC de 70 mm²	u	3
13	Alambre de amarre de aluminio de 16 mm²	m	7,2

DISEÑO : —	PROYECTISTA: POR DESIGNAR	ESCALA : 1:25
REVISÓ : —	LÍNEA PRIMARIA 22,9 kV TRIFÁSICA CAPACHICA – LLACHÓN	LÁMINA N.°
FECHA : OCTUBRE 2026	SOPORTE DE SUSPENSIÓN 0°–5°, TRIFÁSICO SIN NEUTRO TIPO PS1-3	LD-LP-01