
NOTAS: Cotas en mm. Ferretería de acero galvanizado en caliente (ASTM A153/A123).
Fase superior a 0,30 m sobre la cabeza; cruceta a 1,40 m bajo la cabeza (conductores inferiores a 1,10 m).
La numeración de los globos corresponde al orden de la lista de materiales.

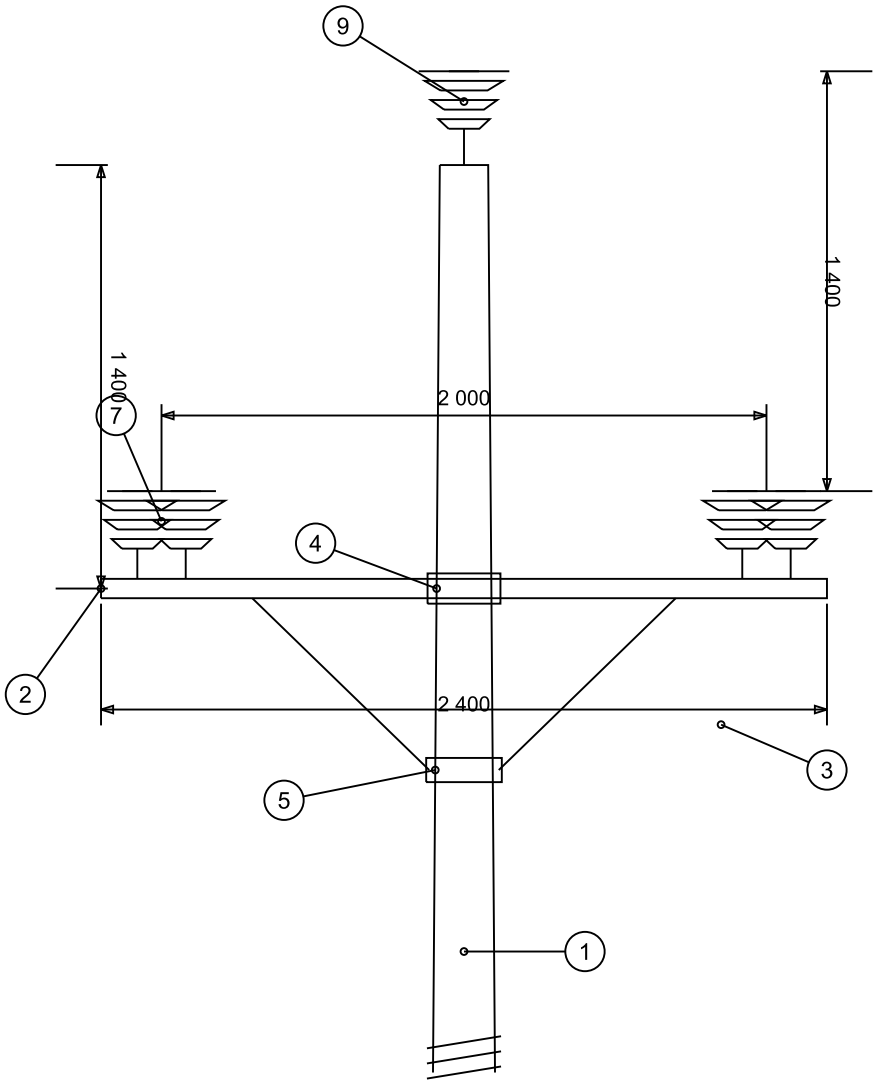

VISTA FRONTAL

LISTA DE MATERIALES

ITEM	DESCRIPCIÓN	UND.	CANT.
1	Poste de C.A.C. 12/400 daN, con perilla	u	1
2	Cruceta de perfil angular FºGº de 64 x 64 x 2400 mm, E = 6,4 mm, con 02 dados. TIPO I	u	2
3	Riostra de perfil angular FºGº de 64 x 64 x 1000 mm, E = 6,4 mm	u	4
4	Abrazadera tipo CAS doble de 75 mm, E = 6,4 mm, D = 206 mm	u	1
5	Perno de doble armado de AºGº de 16 mm ◪ x 508 mm, c/4 tuercas y arandelas	u	4
6	Perno maquinado de AºGº L = 50 mm, D = 13 mm, c/T/C/2A/AP	u	4
7	Arandela cuadrada plana de AºGº 57 x 57 x 5 mm, agujero 18 mm ◪	u	16
8	Aislador de porcelana tipo PIN, clase ANSI 56-4 (línea de fuga 685 mm)	u	5
9	Espiga de AºGº de 609 mm de longitud, para cabeza de poste y aislador ANSI 56-4	u	1
10	Espiga de AºGº para cruceta y aislador ANSI 56-4, de 381 mm de longitud, con accesorios	u	4
11	Varilla de armar preformada simple para conductor AAAC de 70 mm²	u	5
12	Alambre de amarre de aluminio de 16 mm²	m	12

DISEÑO : —	PROYECTISTA: POR DESIGNAR	ESCALA : 1:25
REVISÓ : —	LÍNEA PRIMARIA 22,9 kV TRIFÁSICA CAPACHICA – LLACHÓN	LÁMINA N.°
FECHA : OCTUBRE 2026	SOPORTE DE ÁNGULO 5°–30°, TRIFÁSICO SIN NEUTRO TIPO PA1-3	LD-LP-02