

NOTAS: Cotas en mm. Ferretería de acero galvanizado en caliente (ASTM A153/A123).
Fase superior a 0,30 m sobre la cabeza; cruceta a 1,40 m bajo la cabeza (conductores inferiores a 1,10 m).
La numeración de los globos corresponde al orden de la lista de materiales.

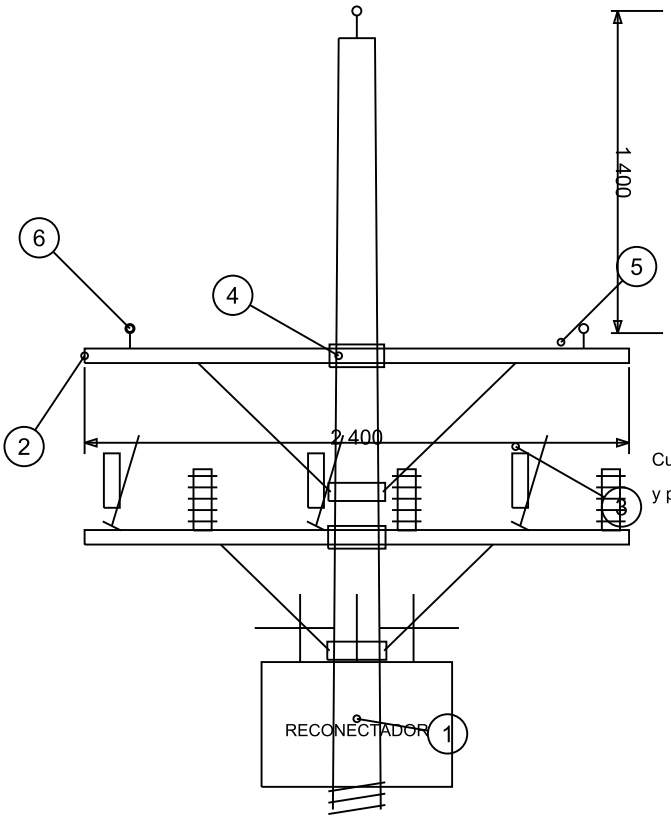


VISTA FRONTAL

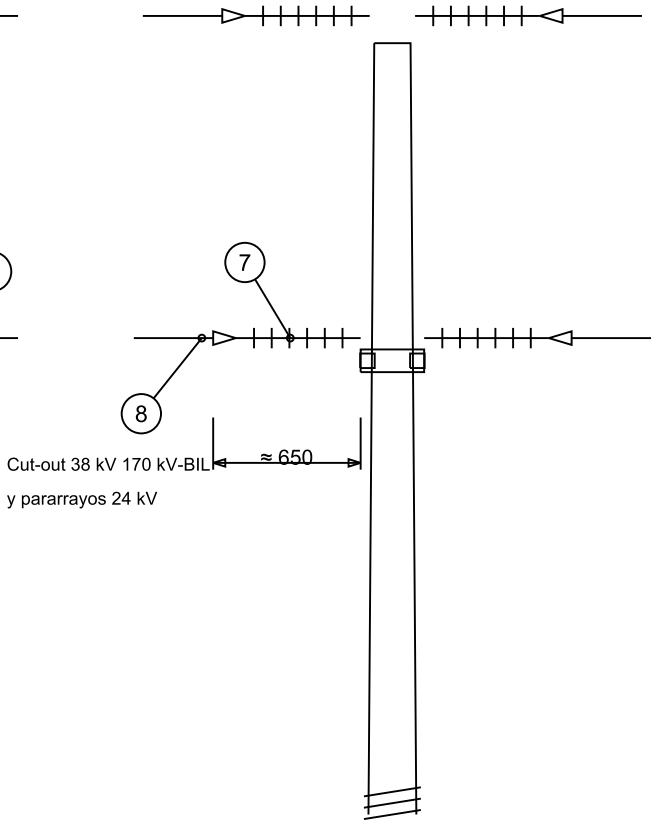


VISTA LATERAL (EN EL SENTIDO DE LA LÍNEA)

## LISTA DE MATERIALES

| ITEM | DESCRIPCIÓN | UND. | CANT. |
|---|---|---|---|
| 1 | Poste de C.A.C. 12/400 daN, con perilla | u | 1 |
| 2 | Cruceta de perfil angular FºGº de 64 x 64 x 2400 mm, E = 6,4 mm, con 02 dados. TIPO I | u | 3 |
| 3 | Riostra de perfil angular FºGº de 64 x 64 x 1000 mm, E = 6,4 mm | u | 5 |
| 4 | Abrazadera tipo CAS doble de 75 mm, E = 6,4 mm, D = 206 mm | u | 1 |
| 5 | Perno de doble armado de AºGº de 16 mm ⌀ x 508 mm, c/4 tuercas y arandelas | u | 4 |
| 6 | Perno maquinado de AºGº L = 50 mm, D = 13 mm, c/T/C/2A/AP | u | 4 |
| 7 | Arandela cuadrada plana de AºGº 57 x 57 x 5 mm, agujero 18 mm ⌀ | u | 16 |
| 8 | Soporte metálico de FºGº para montaje de reconectador en poste, con accesorios | u | 1 |
| 9 | Tuerca ojo de AºGº para perno de 16 mm ⌀ | u | 3 |
| 10 | Perno ojo de AºGº de 16 mm ⌀ x 254 mm, con tuerca y contratuerca | u | 1 |
| 11 | Perno de AºGº de 16 mm ⌀ x 254 mm, con tuerca y contratuerca | u | 2 |
| 12 | Aislador polimérico tipo suspensión 36 kV, conexión horquilla-lengüeta (línea de fuga ≥ 720 mm) | u | 3 |
| 13 | Grillete de AºGº tipo lira de 16 mm ⌀, con pasador de seguridad | u | 3 |
| 14 | Grapa de anclaje tipo pistola de 3 pernos para conductor AAAC 35–70 mm² | u | 3 |
| 15 | Conector doble vía Al/Al para conductor 35–70 mm², tres pernos | u | 6 |
| 16 | Conector bimetálico Al/Cu para conexión de equipos | u | 6 |
| 17 | Seccionador fusible unipolar tipo expulsión (cut-out) de 38 kV, 100 A, 170 kV-BIL | u | 3 |
| 18 | Fusible tipo expulsión tipo K para el seccionamiento del reconectador (calibre según Vol. IX) | u | 3 |
| 19 | Pararrayos de óxido metálico 24 kV, 10 kA, clase 1, MCOV 19,5 kV, línea de fuga ≥ 780 mm | u | 3 |
| 20 | Reconectador automático trifásico 38 kV, 170 kV-BIL, 630 A, 12,5 kA, con control electrónico y TT auxiliar | u | 1 |
| 21 | Conductor AAAC 70 mm² para puentes y conexión a equipos | m | 15 |

| | | |
|---|---|---|
| DISEÑO : — | PROYECTISTA: POR DESIGNAR | ESCALA : 1:30 |
| REVISÓ : — | LÍNEA PRIMARIA 22,9 kV TRIFÁSICA CAPACHICA – LLACHÓN | LÁMINA N.° |
| FECHA : OCTUBRE 2026 | ARMADO CON RECONECTADOR (ARRANQUE) TIPO PSER-3 | LD-LP-06 |