
NOTAS: Tiro máximo de trabajo por retenida 15,15 kN; FS cable ≥ 2,0; FS bloque ≥ 2,0 (Anexo 7).
La retenida se instalará en la bisectriz del ángulo o en la prolongación del alineamiento (anclajes y terminales).

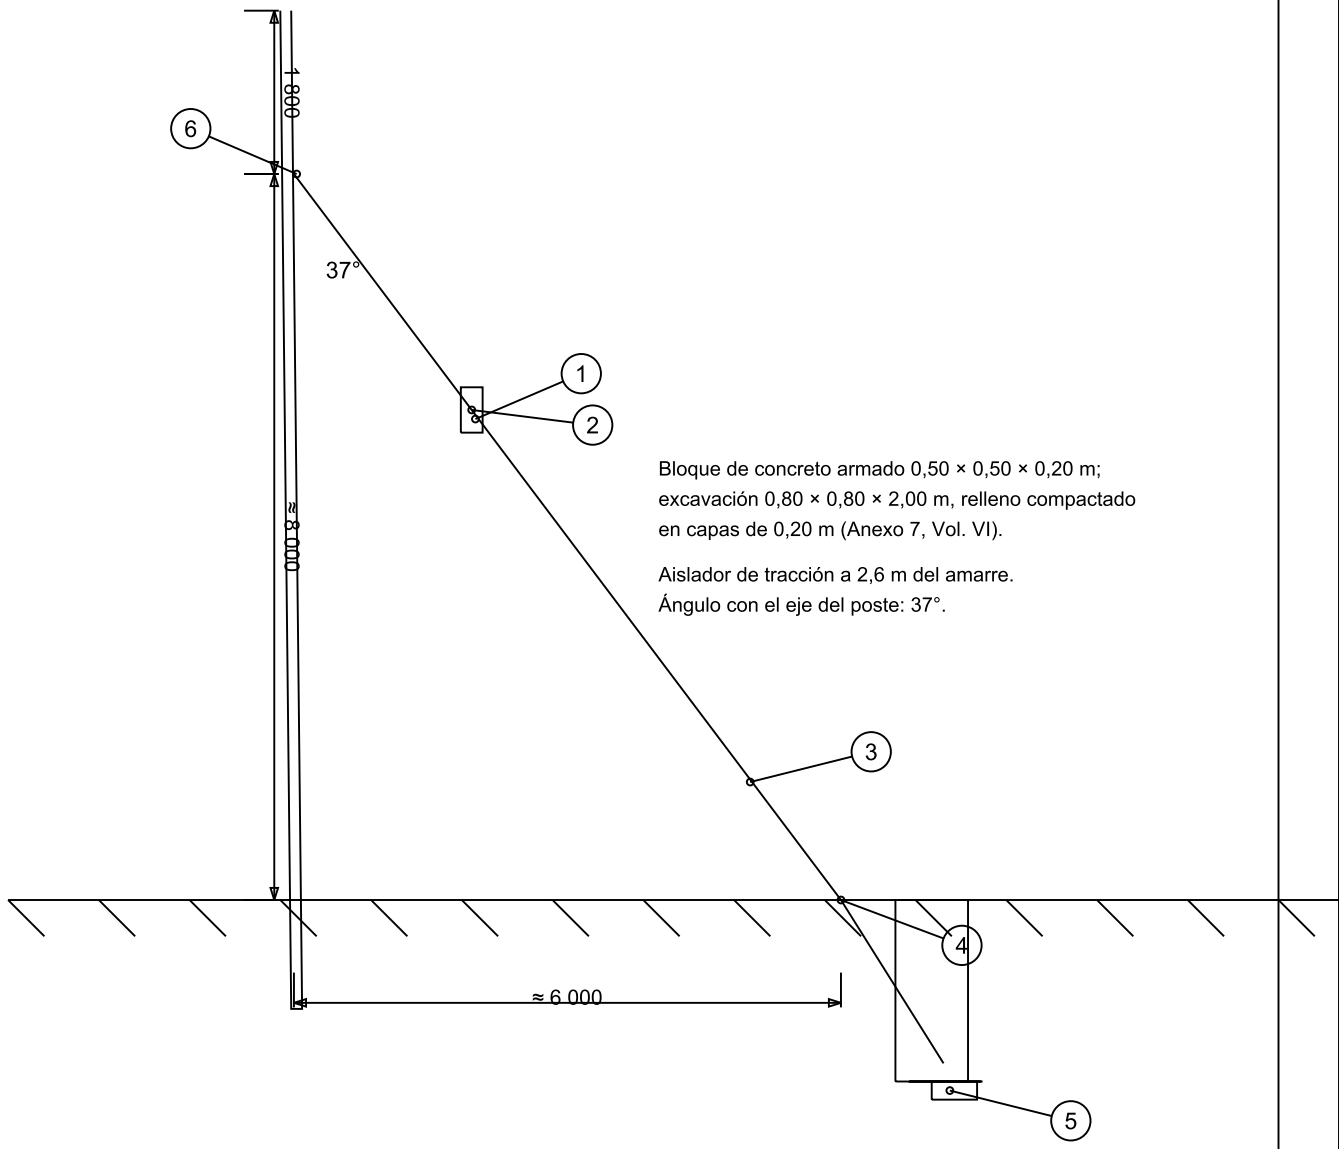


RETENIDA INCLINADA – ELEVACIÓN

## LISTA DE MATERIALES

| ITEM | DESCRIPCIÓN | UND. | CANT. |
|---|---|---|---|
| 1 | Varilla de anclaje de AºGº de 16 mm ⌀ x 2,40 m, con ojal guardacabo, tuerca y contratuerca | u | 1 |
| 2 | Grapa paralela de doble vía de FºGº de tres pernos | u | 2 |
| 3 | Abrazadera de FºGº 185 mm ⌀ x 64 mm x 6,4 mm, tipo partida, c/3 pernos 16 mm ⌀ | u | 1 |
| 4 | Aislador polimérico de tracción para retenida 36 kV | u | 1 |
| 5 | Arandela de anclaje cuadrada plana de FºGº 102 x 102 x 6,4 mm, agujero 20 mm | u | 1 |
| 6 | Guardacabo de FºGº de 16 mm para cable de 10 mm | u | 2 |
| 7 | Guardacable de FºGº de 1,80 mm x 2,40 m, incluye accesorios de fijación | u | 1 |
| 8 | Bloque de concreto armado 0,50 x 0,50 x 0,20 m | u | 1 |
| 9 | Alambre galvanizado de entorche N.° 14 para amarre | m | 1,5 |
| 10 | Cable de acero 10 mm ⌀, 7 hilos, grado Siemens-Martin (poste 12 m / 13 m) | m | 14,0 / 15,1 |

| | | |
|---|---|---|
| DISEÑO : — | PROYECTISTA: POR DESIGNAR | ESCALA : 1:80 |
| REVISÓ : — | LÍNEA PRIMARIA 22,9 kV TRIFÁSICA CAPACHICA – LLACHÓN | LÁMINA N.° |
| FECHA : OCTUBRE 2026 | RETENIDA INCLINADA<br>TIPO RI | LD-LP-08 |