
NOTAS: Resistencia máxima en estructuras con equipos: 25 Ω (medir; Anexo 3).
Relleno con tierra de cultivo cernida + cemento conductivo (1 dosis por varilla).

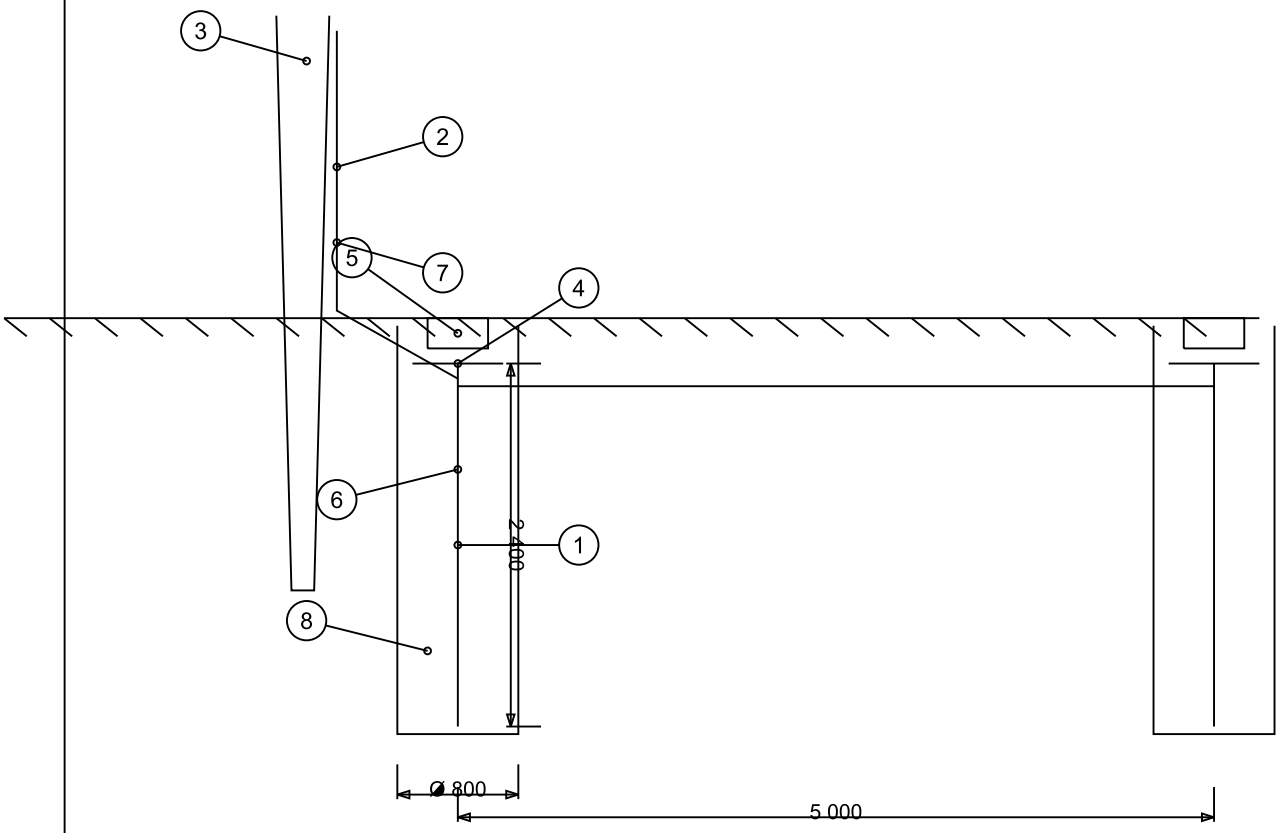

PUESTA A TIERRA TIPO PAT-2 – ELEVACIÓN

LISTA DE MATERIALES

ITEM	DESCRIPCIÓN	UND.	CANT.
1	Varilla de cobre de 16 mm Ø x 2,40 m, con rosca al final de 100 mm	u	2
2	Conductor de cobre recocido cableado de 25 mm², para puesta a tierra	m	22
3	Plancha doblada de cobre para toma a tierra de espigas y/o pernos	u	2
4	Conector de bronce para electrodo de 16 mm Ø y conductor de cobre de 25 mm²	u	2
5	Conector de cobre tipo perno partido para conductor de cobre de 25 mm²	u	2
6	Caja de registro de concreto para puesta a tierra 0,40 x 0,40 x 0,20 m	u	2
7	Cemento conductivo (dosis de 25 kg)	u	2
8	Tubo de PVC SAP de 19 mm Ø x 0,50 m, con curva de 90°	u	1
9	Tierra negra de cultivo, cernida	m3	2,6

DISEÑO : —	PROYECTISTA: POR DESIGNAR	ESCALA : 1:40
REVISÓ : —	LÍNEA PRIMARIA 22,9 kV TRIFÁSICA CAPACHICA – LLACHÓN	LÁMINA N.°
FECHA : OCTUBRE 2026	PUESTA A TIERRA TIPO PAT-2	LD-LP-10