

NOTAS: Cotas en mm. Ferretería de acero galvanizado en caliente (ASTM A153/A123).
Fase superior a 0,30 m sobre la cabeza; cruceta a 1,40 m bajo la cabeza (conductores inferiores a 1,10 m).
La numeración de los globos corresponde al orden de la lista de materiales.

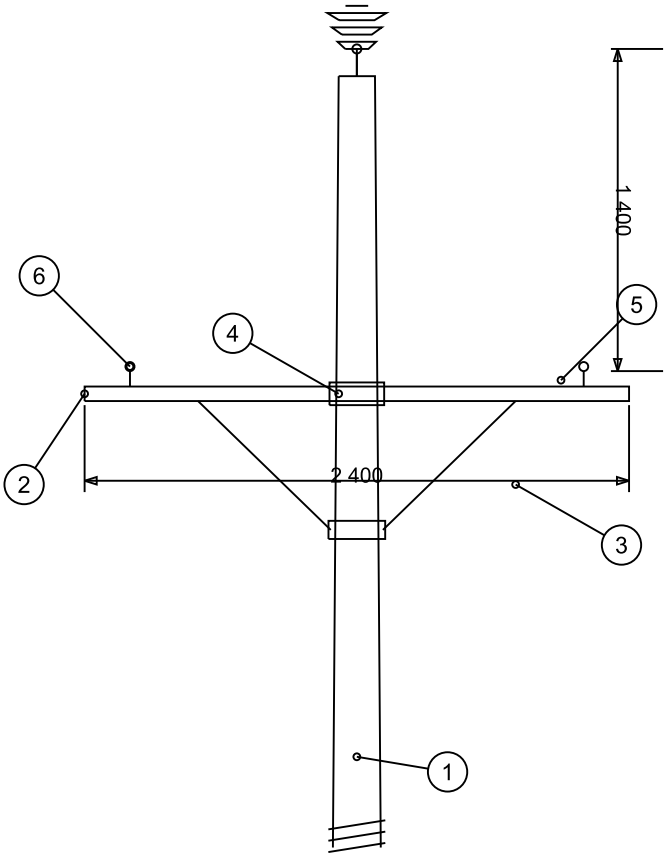

VISTA FRONTAL

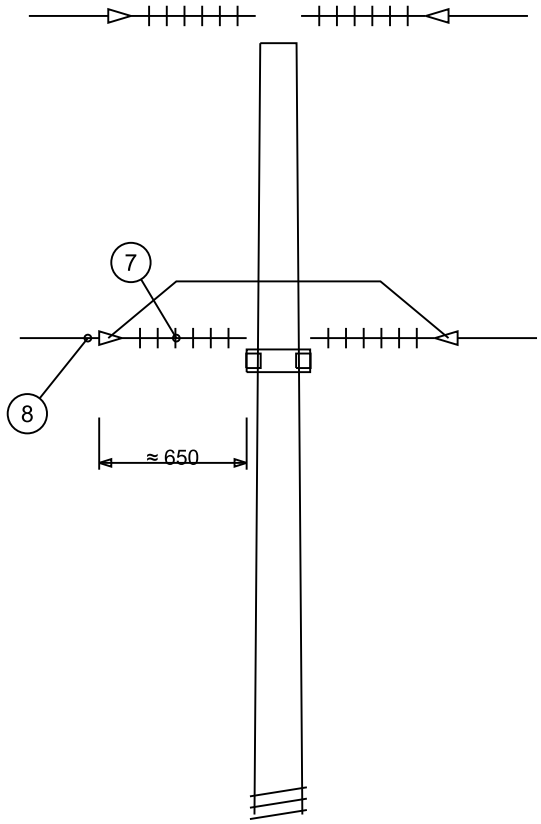

VISTA LATERAL (EN EL SENTIDO DE LA LÍNEA)

LISTA DE MATERIALES

ITEM	DESCRIPCIÓN	UND.	CANT.
1	Poste de C.A.C. 12/400 daN, con perilla	u	1
2	Cruceta de perfil angular FºGº de 64 x 64 x 2400 mm, E = 6,4 mm, con 02 dados. TIPO I	u	2
3	Riostra de perfil angular FºGº de 64 x 64 x 1000 mm, E = 6,4 mm	u	4
4	Abrazadera tipo CAS doble de 75 mm, E = 6,4 mm, D = 206 mm	u	1
5	Perno de doble armado de AºGº de 16 mm ⌀ x 508 mm, c/4 tuercas y arandelas	u	4
6	Perno maquinado de AºGº L = 50 mm, D = 13 mm, c/T/C/2A/AP	u	4
7	Arandela cuadrada plana de AºGº 57 x 57 x 5 mm, agujero 18 mm ⌀	u	16
8	Tuerca ojo de AºGº para perno de 16 mm ⌀	u	6
9	Perno ojo de AºGº de 16 mm ⌀ x 254 mm, con tuerca y contratuerca	u	1
10	Perno de AºGº de 16 mm ⌀ x 254 mm, con tuerca y contratuerca	u	2
11	Aislador polimérico tipo suspensión 36 kV, conexión horquilla-lengüeta (línea de fuga ≥ 720 mm)	u	6
12	Grillete de AºGº tipo lira de 16 mm ⌀, con pasador de seguridad	u	6
13	Grapa de anclaje tipo pistola de 3 pernos para conductor AAAC 35–70 mm²	u	6
14	Aislador de porcelana tipo PIN, clase ANSI 56-4 (línea de fuga 685 mm)	u	1
15	Espiga de AºGº de 609 mm de longitud, para cabeza de poste y aislador ANSI 56-4	u	1
16	Alambre de amarre de aluminio de 16 mm²	m	2,4
17	Cinta plana de armar de aluminio	m	1
18	Conector doble vía Al/Al para conductor 35–70 mm², tres pernos	u	3
19	Conductor AAAC 70 mm² para puentes y conexión a equipos	m	6

DISEÑO : —	PROYECTISTA: POR DESIGNAR	ESCALA : 1:30
REVISÓ : —	LÍNEA PRIMARIA 22,9 kV TRIFÁSICA CAPACHICA – LLACHÓN	LÁMINA N.°
FECHA : OCTUBRE 2026	SOPORTE DE RETENCIÓN/SUSPENSIÓN, TRIFÁSICO SIN NEUTRO TIPO TS-3	LD-LP-14