


PLANO ELECTRICO - PISO 2 V4

Casa de Aquiles - segundo nivel

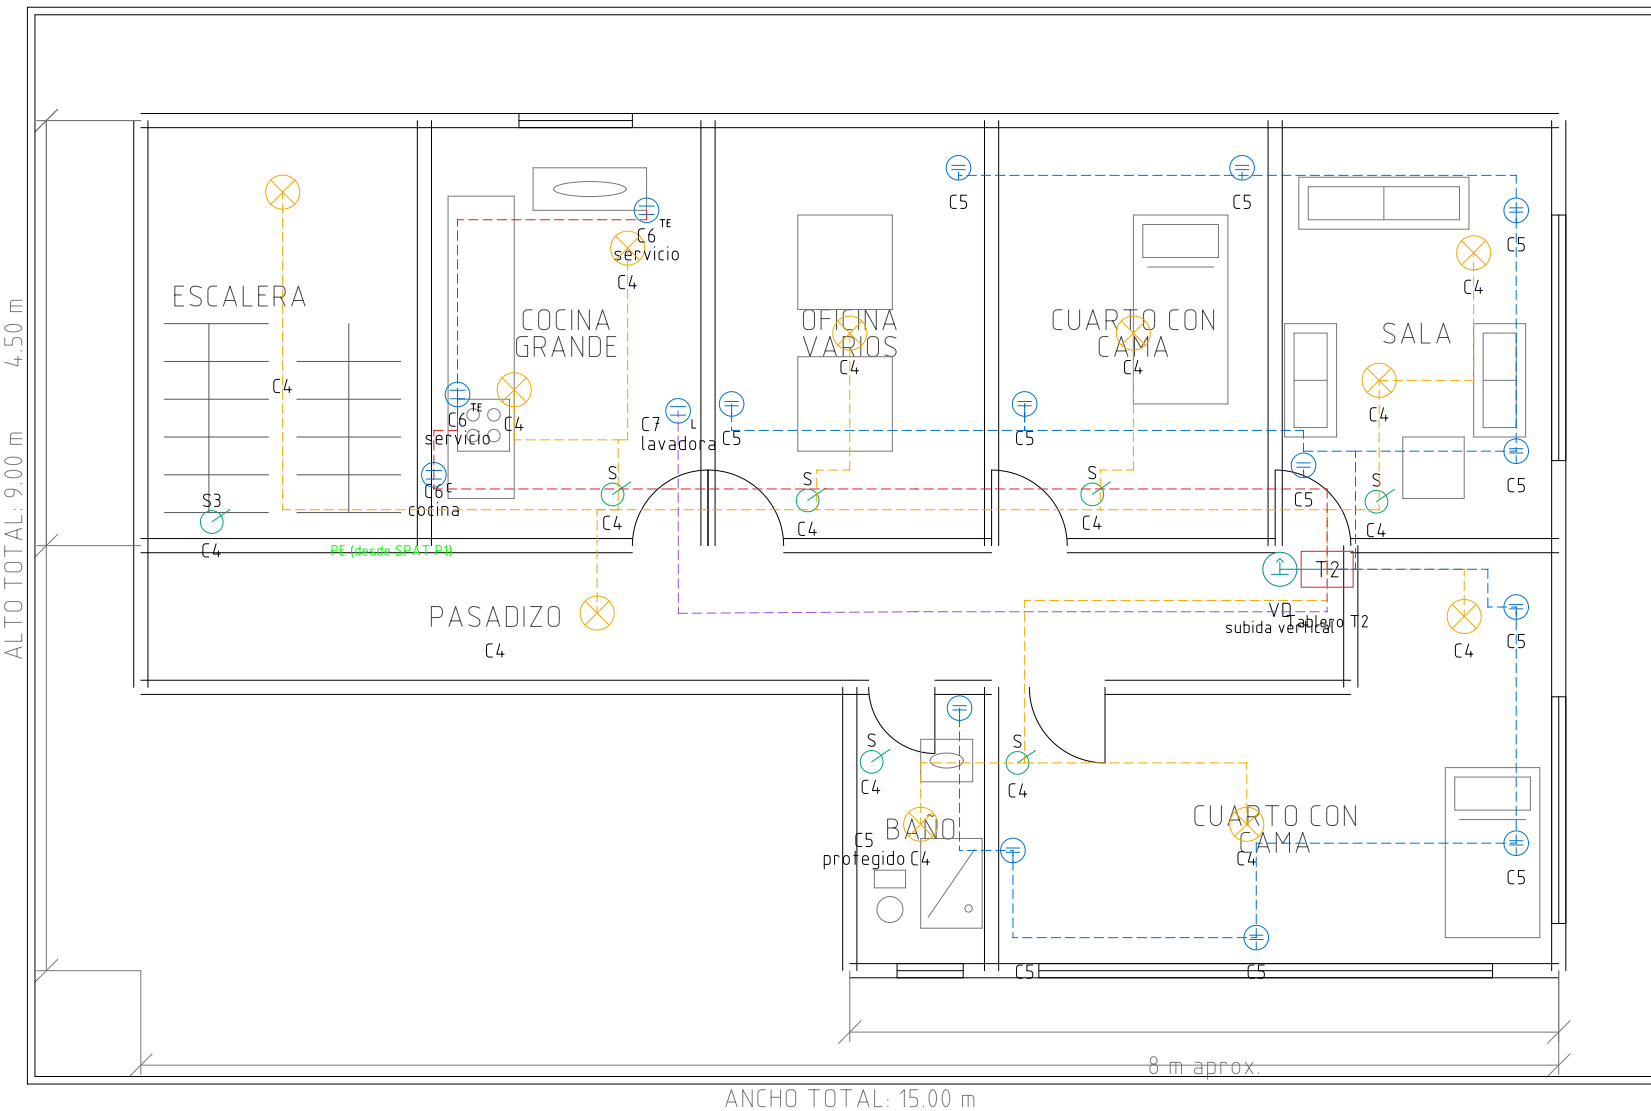

LEYENDA ELECTRICA

Simbolos

- Punto para foco
- Interruptor simple
- Tomacorriente con tierra
- Toma especial monofasica (cocina/servicio)
- Salida especial monofasica (lavadora)
- Tablero segundo piso T2
- Ducto vertical VD

Lineas

- C4 Alumbrado
- C5 Tomacorrientes
- C6 Cocina/servicio
- C7 Lavadora
- Subida/bajada TG-T2
- Canalizacion empotrada

Base: Seccion 9 DGE / ubicaciones manuales v2 preservadas

NOTA: Toda la instalacion de tomacorrientes es MONOFASICA (220V).
No existen tomacorrientes trifasicos en esta vivienda.