
LÍNEA PRIMARIA LIMBANI – HUANCASAYANI

LP-02

LP-R02 | 18/10/2026

Unifilar funcional y alternativas de tensión

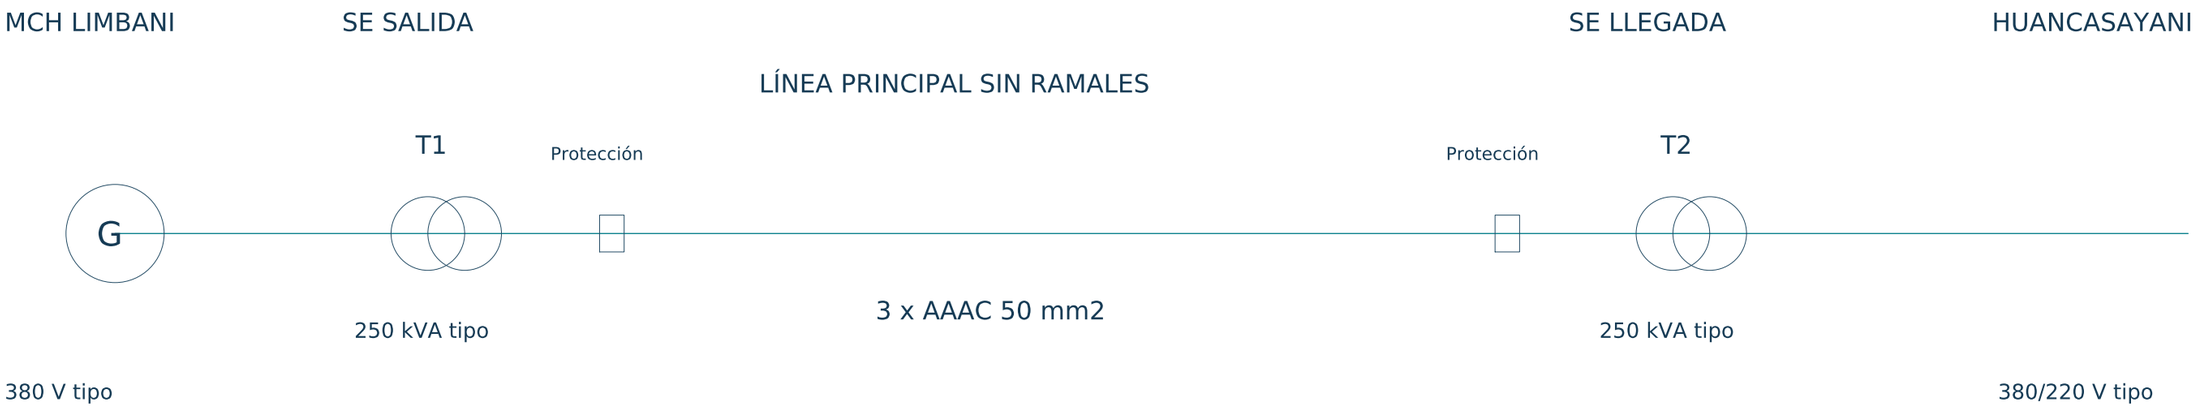

Escenario de compatibilidad: T1 0.38/10 kV y T2 10/0.38 kV, ambas relaciones sin placa verificada.

Alternativa rural nueva a estudiar: T1 0.38/22.9 kV y T2 22.9/0.38 kV. Requiere oferta y selección integral de equipos.

380 V,250 kVA y potencia200 kW son hipótesis del modelo; no datos confirmados de la instalación. La oferta150 kW se contrasta como sensibilidad.

Si los devanadosMT son delta, la puesta a tierra del neutroMT exige transformador de puesta a tierra compatible; NGR no puede conectarse a un neutro inexistente.

Esquema funcional. Grupos, tomas, relacionesTC/TT, aislamiento y ajustes de protección quedan pendientes. VerCSV de cortocircuito y memoria4.5.