
LÍNEA PRIMARIA LIMBANI – HUANCASAYANI


LP-07

LP-R02 | 18/10/2026

Planta y perfil de gabinete: P033 – P049

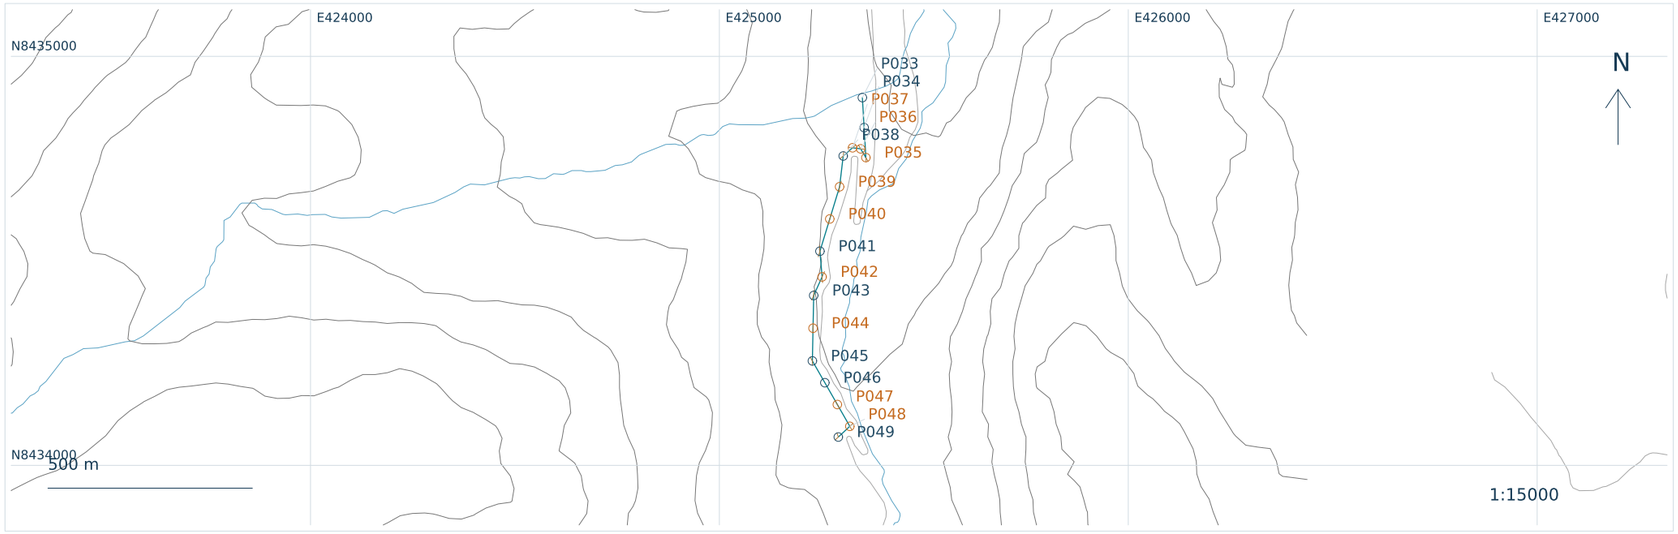

H 1:5000 | V 1:2000 | CALOR_FINAL75C + fluencia345 microstrain

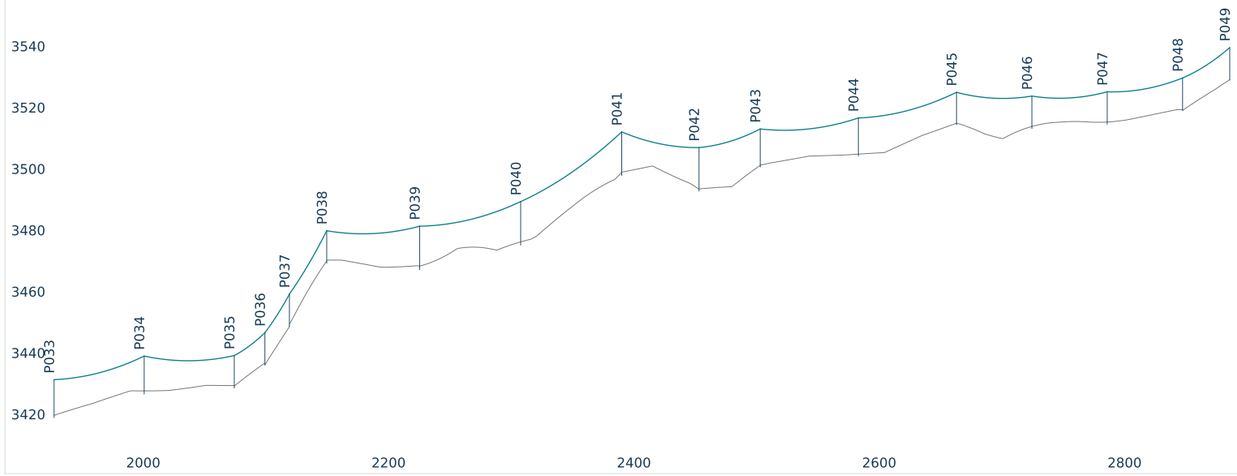

Progresiva 1941.3–2899.7 m. Un solo eje representa tres conductores.

Naranja: carga ascendente en algún estado. Retenidas dibujadas como posiciones ideales pendientes.

Terreno gris: perfil DEM heredado. Conductor verde: cálculo por vano; no es medición ni gálibo certificado.

Las cotas DEM tienen resolución~30 m. Topografía lateral y de cruces pendiente.

Vanos de esta lámina:

V033: L73.5 m, f1.62 m

V034: L73.5 m, f1.60 m

V035: L24.9 m, f0.54 m

V036: L20.0 m, f0.52 m

V037: L30.4 m, f0.84 m

V038: L75.7 m, f1.66 m

V039: L82.4 m, f1.84 m

V040: L82.4 m, f1.94 m

V041: L63.0 m, f1.36 m

V042: L49.9 m, f1.06 m

V043: L80.0 m, f1.77 m

V044: L80.0 m, f1.78 m

V045: L61.4 m, f1.31 m

V046: L61.4 m, f1.31 m

V047: L61.4 m, f1.32 m

V048: L38.4 m, f0.83 m

INSTALACIONES ELÉCTRICAS II | Aquiles Taylor Ramos Yapo | 227368

REVISIÓN ACADÉMICA · CAMPO, EQUIPOS Y PREDIOS PENDIENTES

UTM WGS84 / 19S · EPSG:32719 | Modelo CAD en metros

Escala al imprimir A3: S/E