
LÍNEA PRIMARIA LIMBANI – HUANCASAYANI


LP-09

LP-R02 | 18/10/2026

Planta y perfil de gabinete: P065 – P081

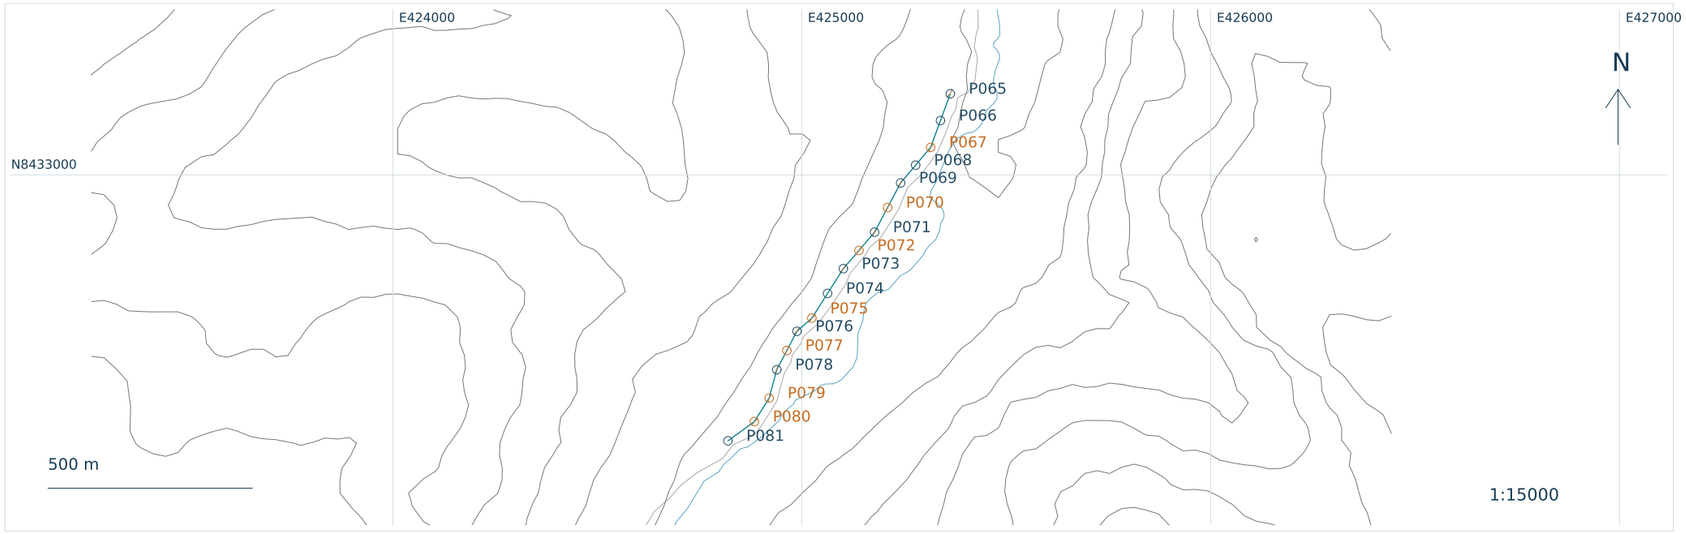

H 1:5000 | V 1:2000 | CALOR_FINAL75C + fluencia345 microstrain

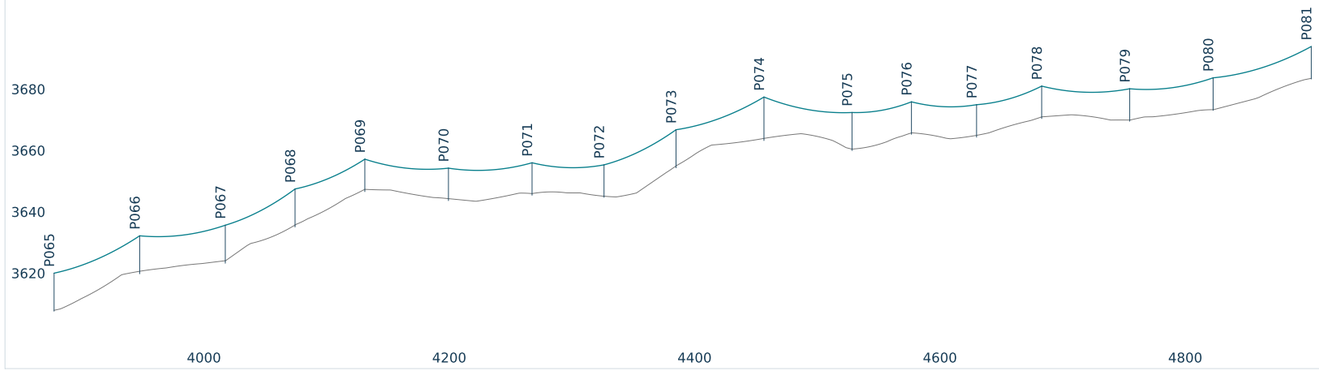

Progresiva 3891.8–4916.7 m. Un solo eje representa tres conductores.

Naranja: carga ascendente en algún estado. Retenidas dibujadas como posiciones ideales pendientes.

Terreno gris: perfil DEM heredado. Conductor verde: cálculo por vano; no es medición ni gálibo certificado.

Las cotas DEM tienen resolución~30 m. Topografía lateral y de cruces pendiente.

Vanos de esta lámina:

V065: L69.8 m, f1.55 m

V066: L69.8 m, f1.52 m

V067: L56.9 m, f1.25 m

V068: L56.9 m, f1.24 m

V069: L68.1 m, f1.48 m

V070: L68.1 m, f1.47 m

V071: L58.7 m, f1.25 m

V072: L58.7 m, f1.29 m

V073: L71.7 m, f1.59 m

V074: L71.7 m, f1.57 m

V075: L48.5 m, f1.02 m

V076: L53.1 m, f1.12 m

V077: L53.1 m, f1.13 m

V078: L71.8 m, f1.56 m

V079: L68.0 m, f1.47 m

V080: L80.0 m, f1.79 m

INSTALACIONES ELÉCTRICAS II | Aquiles Taylor Ramos Yapo | 227368

REVISIÓN ACADÉMICA · CAMPO, EQUIPOS Y PREDIOS PENDIENTES

UTM WGS84 / 19S · EPSG:32719 | Modelo CAD en metros

Escala al imprimir A3: S/E