
LÍNEA PRIMARIA LIMBANI – HUANCASAYANI


LP-10

LP-R02 | 18/10/2026

Planta y perfil de gabinete: P081 – P096

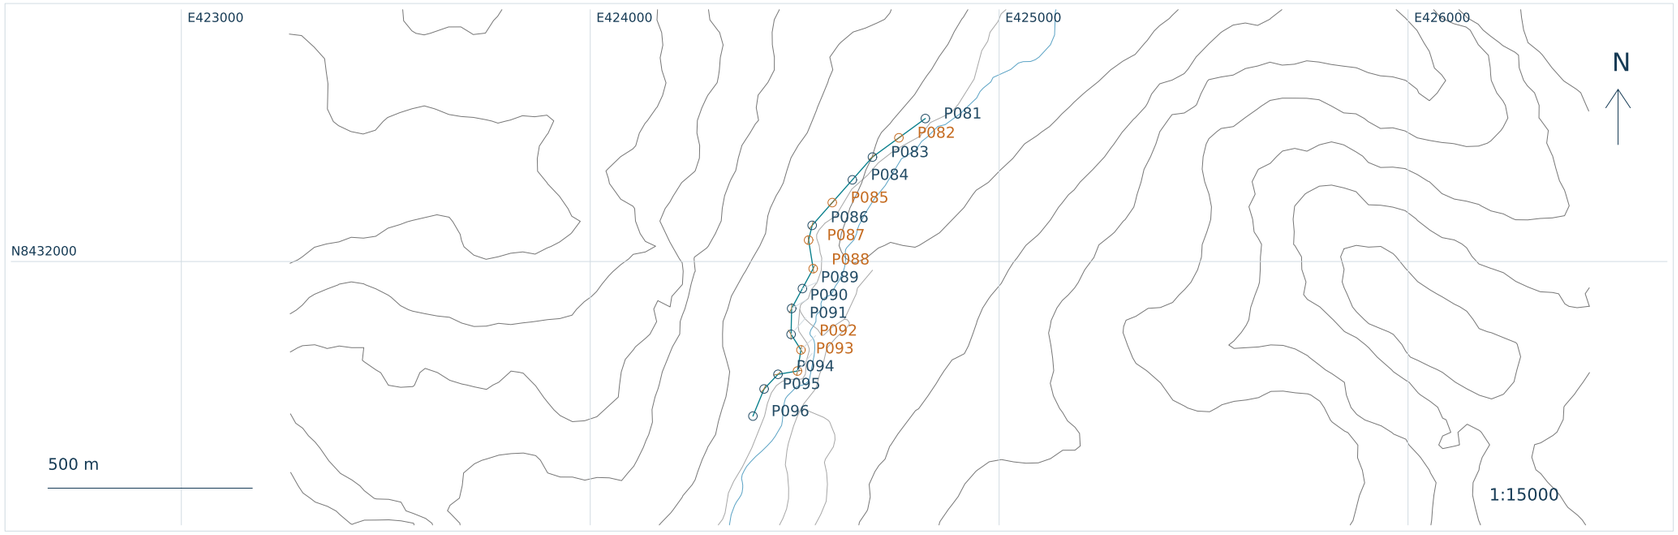

H 1:5000 | V 1:2000 | CALOR_FINAL75C + fluencia345 microstrain

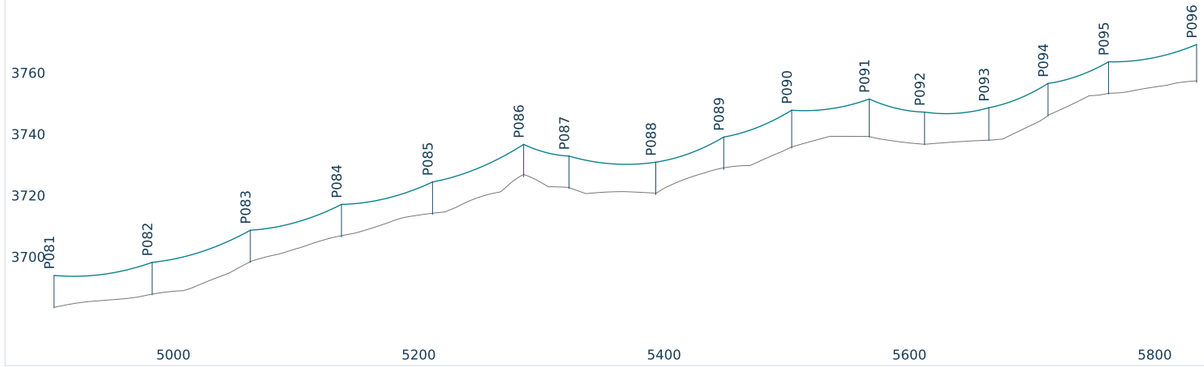

Progresiva 4916.7–5848.1 m. Un solo eje representa tres conductores.

Naranja: carga ascendente en algún estado. Retenidas dibujadas como posiciones ideales pendientes.

Terreno gris: perfil DEM heredado. Conductor verde: cálculo por vano; no es medición ni gálibo certificado.

Las cotas DEM tienen resolución~30 m. Topografía lateral y de cruces pendiente.

Vanos de esta lámina:

V081: L80.0 m, f1.77 m

V082: L80.0 m, f1.79 m

V083: L74.3 m, f1.64 m

V084: L74.3 m, f1.64 m

V085: L74.3 m, f1.66 m

V086: L37.0 m, f0.77 m

V087: L70.7 m, f1.54 m

V088: L55.4 m, f1.19 m

V089: L55.4 m, f1.20 m

V090: L63.2 m, f1.36 m

V091: L45.1 m, f0.94 m

V092: L52.4 m, f1.10 m

V093: L48.3 m, f1.03 m

V094: L49.4 m, f1.05 m

V095: L71.8 m, f1.57 m

INSTALACIONES ELÉCTRICAS II | Aquiles Taylor Ramos Yapo | 227368

REVISIÓN ACADÉMICA · CAMPO, EQUIPOS Y PREDIOS PENDIENTES

UTM WGS84 / 19S · EPSG:32719 | Modelo CAD en metros

Escala al imprimir A3: S/E