
LÍNEA PRIMARIA LIMBANI – HUANCASAYANI


LP-11

LP-R02 | 18/10/2026

Planta y perfil de gabinete: P096 – P111

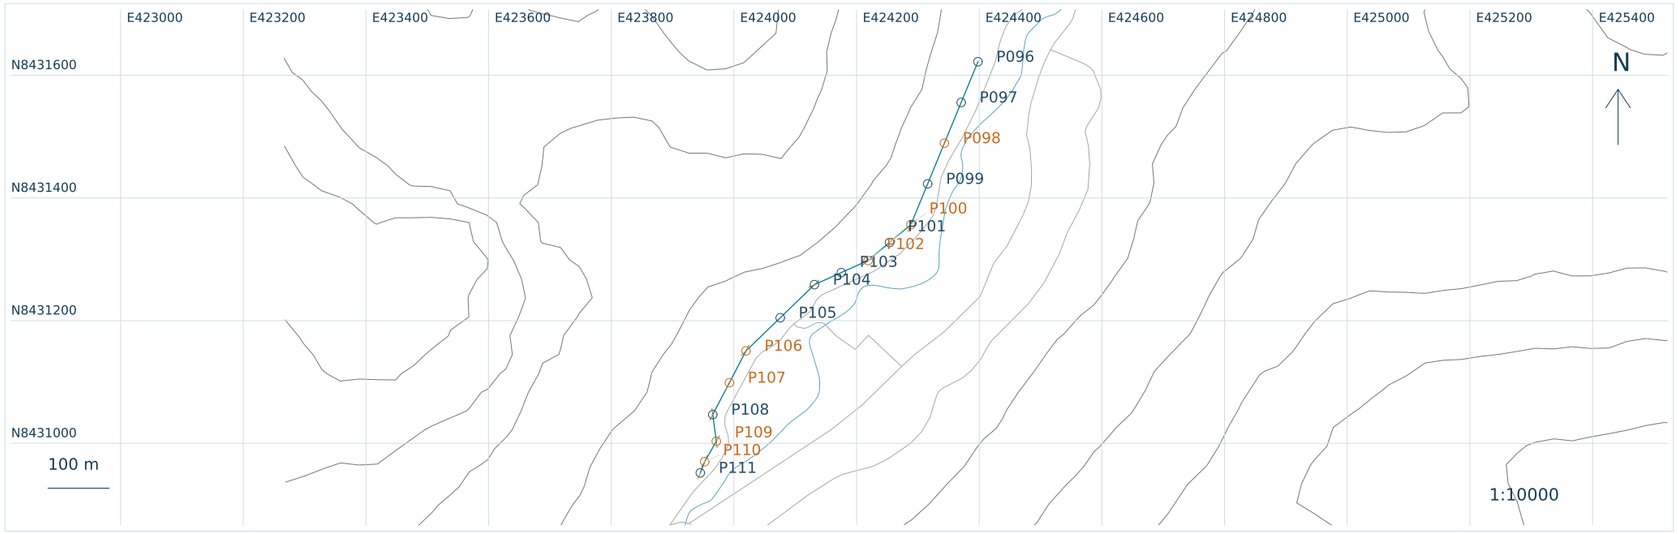

H 1:5000 | V 1:500 | CALOR_FINAL75C + fluencia345 microstrain

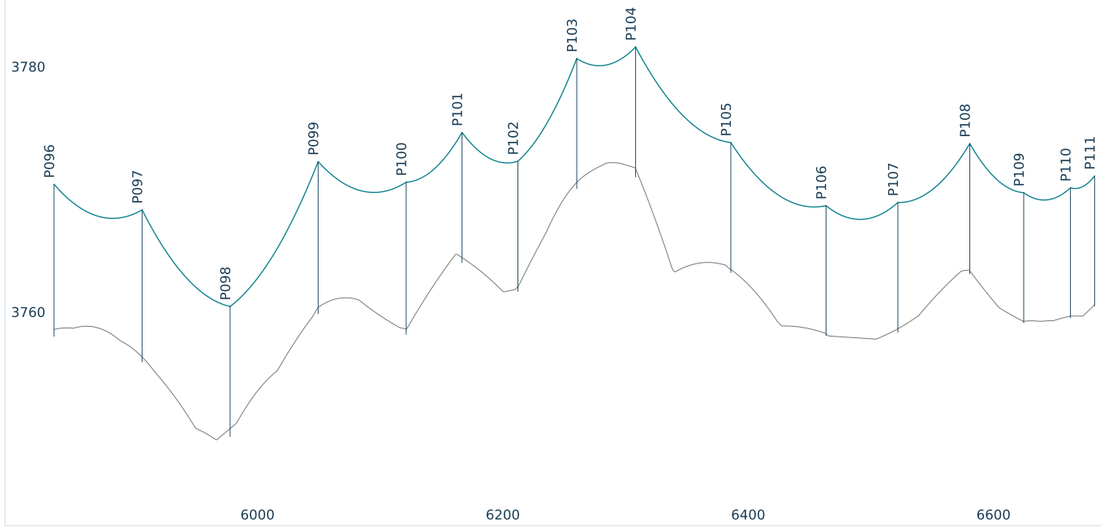

Progresiva 5848.1–6696.4 m. Un solo eje representa tres conductores.

Naranja: carga ascendente en algún estado. Retenidas dibujadas como posiciones ideales pendientes.

Terreno gris: perfil DEM heredado. Conductor verde: cálculo por vano; no es medición ni gálibo certificado.

Las cotas DEM tienen resolución~30 m. Topografía lateral y de cruces pendiente.

Vanos de esta lámina:

V096: L71.8 m, f1.56 m

V097: L71.8 m, f1.58 m

V098: L71.8 m, f1.60 m

V099: L71.8 m, f1.56 m

V100: L45.5 m, f0.95 m

V101: L45.5 m, f0.95 m

V102: L48.0 m, f1.03 m

V103: L48.0 m, f1.00 m

V104: L77.6 m, f1.72 m

V105: L77.6 m, f1.71 m

V106: L58.6 m, f1.25 m

V107: L58.6 m, f1.25 m

V108: L44.0 m, f0.92 m

V109: L38.1 m, f0.78 m

V110: L19.7 m, f0.39 m

INSTALACIONES ELÉCTRICAS II | Aquiles Taylor Ramos Yapo | 227368

REVISIÓN ACADÉMICA · CAMPO, EQUIPOS Y PREDIOS PENDIENTES

UTM WGS84 / 19S · EPSG:32719 | Modelo CAD en metros

Escala al imprimir A3: S/E