

NOTAS: Dimensiones según Anexo 5 (método de Sulzberger). Capacidad lateral asumida 2,1 daN/cm² – confirmar con EMS.
Volúmenes por poste: 12 m: excav. 0,955 m³, ciclópeo 0,75 m³; 13 m: excav. 1,272 m³, ciclópeo 1,02 m³.

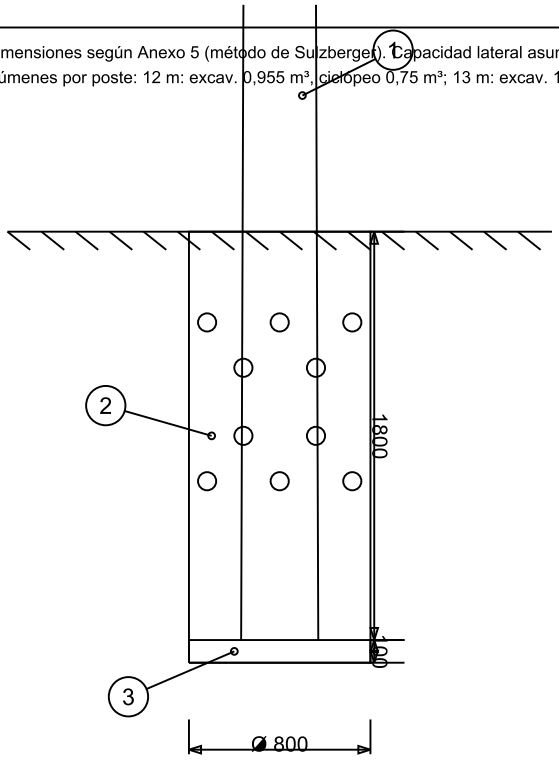

POSTE 12/300 – 12/400

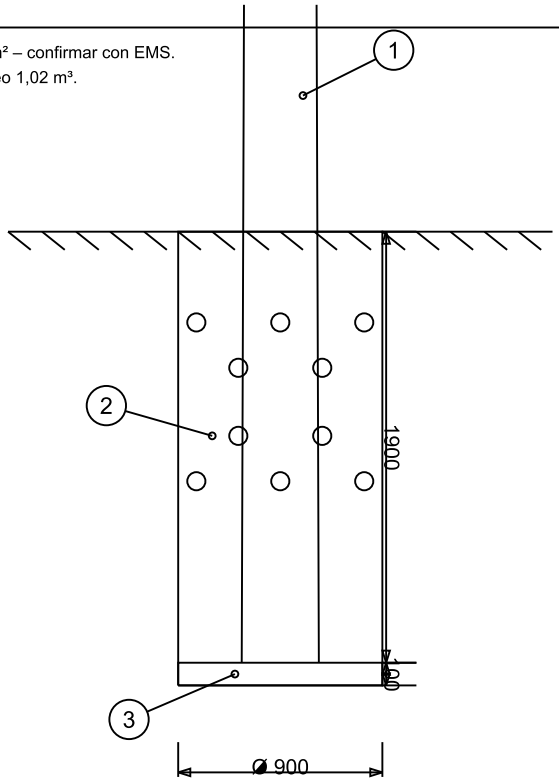

POSTE 13/400

1. Poste de C.A.C. 2. Concreto ciclópeo f'c = 100 kg/cm² + 30 % P.M. 3. Solado f'c = 100 kg/cm², e = 0,10 m

DISEÑO : R.G.M.G.	PROYECTISTA: RENZO GABRIEL MAMANI GALINDO	ESCALA : 1:35
REVISÓ : L.V.C.	LÍNEA PRIMARIA 22,9 kV TRIFÁSICA CAPACHICA – LLACHÓN	LÁMINA N.°
FECHA : OCTUBRE 2026	CIMENTACIÓN DE POSTES TIPO CM (CONCRETO CICLÓPEO)	LD-LP-11