




RECTOR:
DR. PAULINO MACHACA ARI
VICERECTOR ACADEMICO:
DR. MARIO S. CUENTAS ALVARADO
VICERECTOR DE INVESTIGACION:
DR. ARIEL VELAZCO CARDENAS

U.E.I
UNIDAD EJECUTORA
DE INVERSIONES

**SUB-UNIDAD
DE ESTUDIOS**

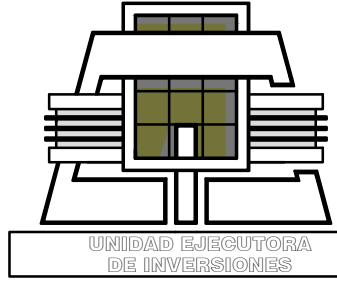

APRE. LÍNEA EJECUTIVA DE INVERSIÓN
ING. WILBER F. CAYRO ROJAS
APRE. SUB-UNIDAD DE ESTUDIOS
ING. ANDRÉS A. QUIZA AÑAZCO

PROYECTO:
INSTALACIONES
ELECTRICAS

PLANO:
**ALIMENTACIÓN
PRIMER NIVEL**

PROYECTO:
"MEJORAMIENTO DE LA
GESTIÓN INSTITUCIONAL EN
EDUCACIÓN UNIVERSITARIA
DE LOS SERVICIOS
ADMINISTRATIVOS DE LA
UNIVERSIDAD NACIONAL DEL
ALTIPLANO, DISTRITO DE
PUNO -PROVINCIA DE PUNO -
DEPARTAMENTO DE PUNO"

OBJETIVO:
"ADECUADA Y SUFICIENTE
INFRAESTRUCTURA PARA
LABOR ADMINISTRATIVA
EN LA UNIVERSIDAD"

DESARROLLADO POR: INSTALACIONES ELECTRICAS

ING. ANTERO NEFTALI AJROTA MAQUERA

UBICACIÓN:
BARRIO BELLAVISTA

AV. EL SOL N° 329

UBICACIÓN:
DPTO. PUNO

PROV. PUNO


DISTR. PUNO

PROYECTO:
SUB-UNIDAD DE
ESTUDIOS

FECHA:
FEBRERO 2023

INDICADA

IE-AL1

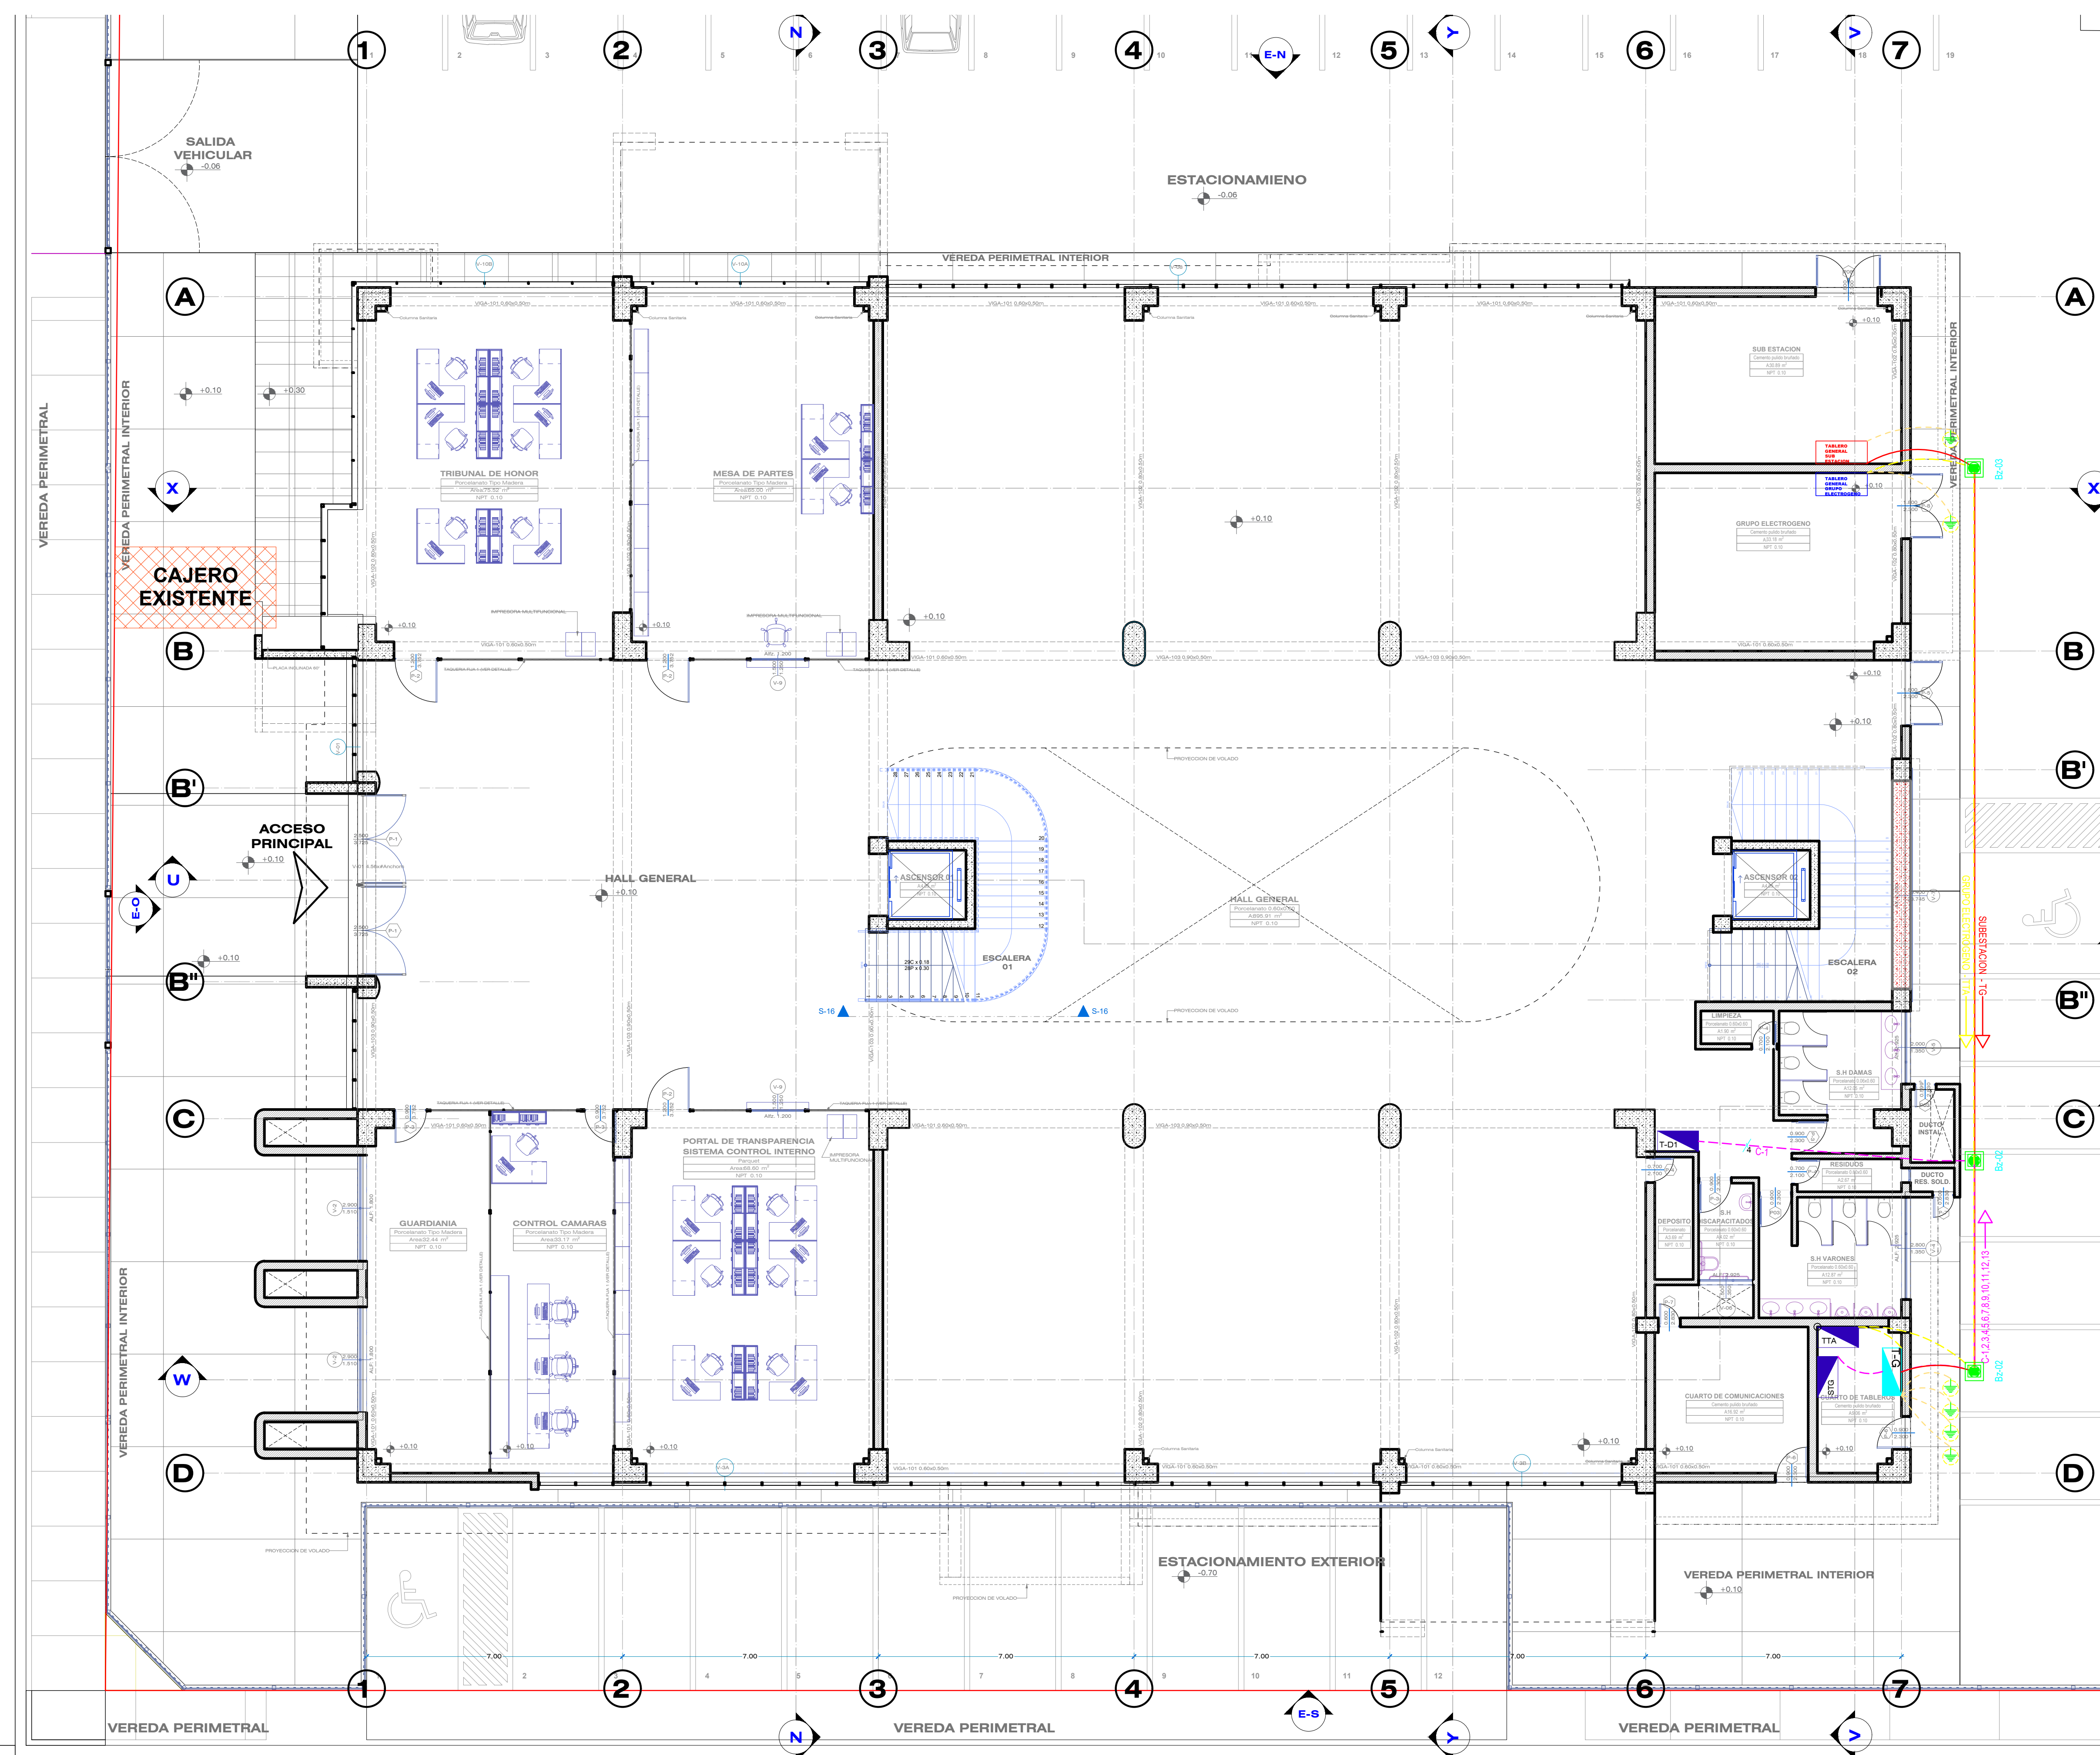

LEYENDA GENERAL			
SÍMBOLOS	DESCRIPCION	CAJAS (mm)	ALTURA s.n.p.t. (m)
	SUBESTACION COMPACTA TIPO PEDESTAL PROTEGIDA	—	—
	TABLERO GENERAL ELECTRICA PARA SALIDAS NORMALES DE USO GENERAL EN LOS EDIFICIOS EMPOTRADO TIPO MODULAR	ESPECIAL	1.80m
	TABLERO DE DISTRIBUCION ELECTRICA PARA SALIDAS NORMALES DE USO GENERAL EN PISO Y/O SUBPISO Y/O COMERCIAL	ESPECIAL	1.80m
	TABLERO DE TRANSFERENCIA PARA UNICION ENTRE EL GRUPO ELECTROGENO Y EL T.O.	ESPECIAL	1.80m
	SUB TABLERO GENERAL (T.O.)	ESPECIAL	1.80m
	TABLERO DE FUERZA CONTROL DE ELECTROIMPULSOS	ESPECIAL	1.80m
	BANCA DE BAJA TENSION, SEGUN ESPECIFICACIONES TECNICAS	—	—
	BANCA ELECTRONICA DE CONTROL SEGUN ESPECIFICACIONES TECNICAS	—	—
	PUNTO DE PUESTA A TIERRA CONVENCIONAL	—	—
	CIRCUITO DE ALUMINADORES	—	—
	CIRCUITO DE PUESTA A TIERRA DE PROTECCION	—	—
	REPRESENTACION DEL NUMERO DE CONDUCTORES QUE TIEN UN CIRCUITO	—	—
	GRUPO ELECTROGENO TRIFASICO 380V/220V	—	—
	CIRCUITO DERIVADO DE TABLERO GENERAL A SUB TABLERO DE DISTRIBUCION ELECTRICA POR DE D. EMPOTRADO EN PISO O PARED	—	—
	CABLE DE PUESTA A TIERRA DE 70mm ESPESOR 1.20mm DE 1000/1000mm PARA EMPOTRAR EN MURO	—	—
	CABLE DERIVADO DE 25 mm2 CORRE DE 7 ALIS PARA PUESTA A TIERRA	—	—

PRIMER NIVEL
Escala 1:75