



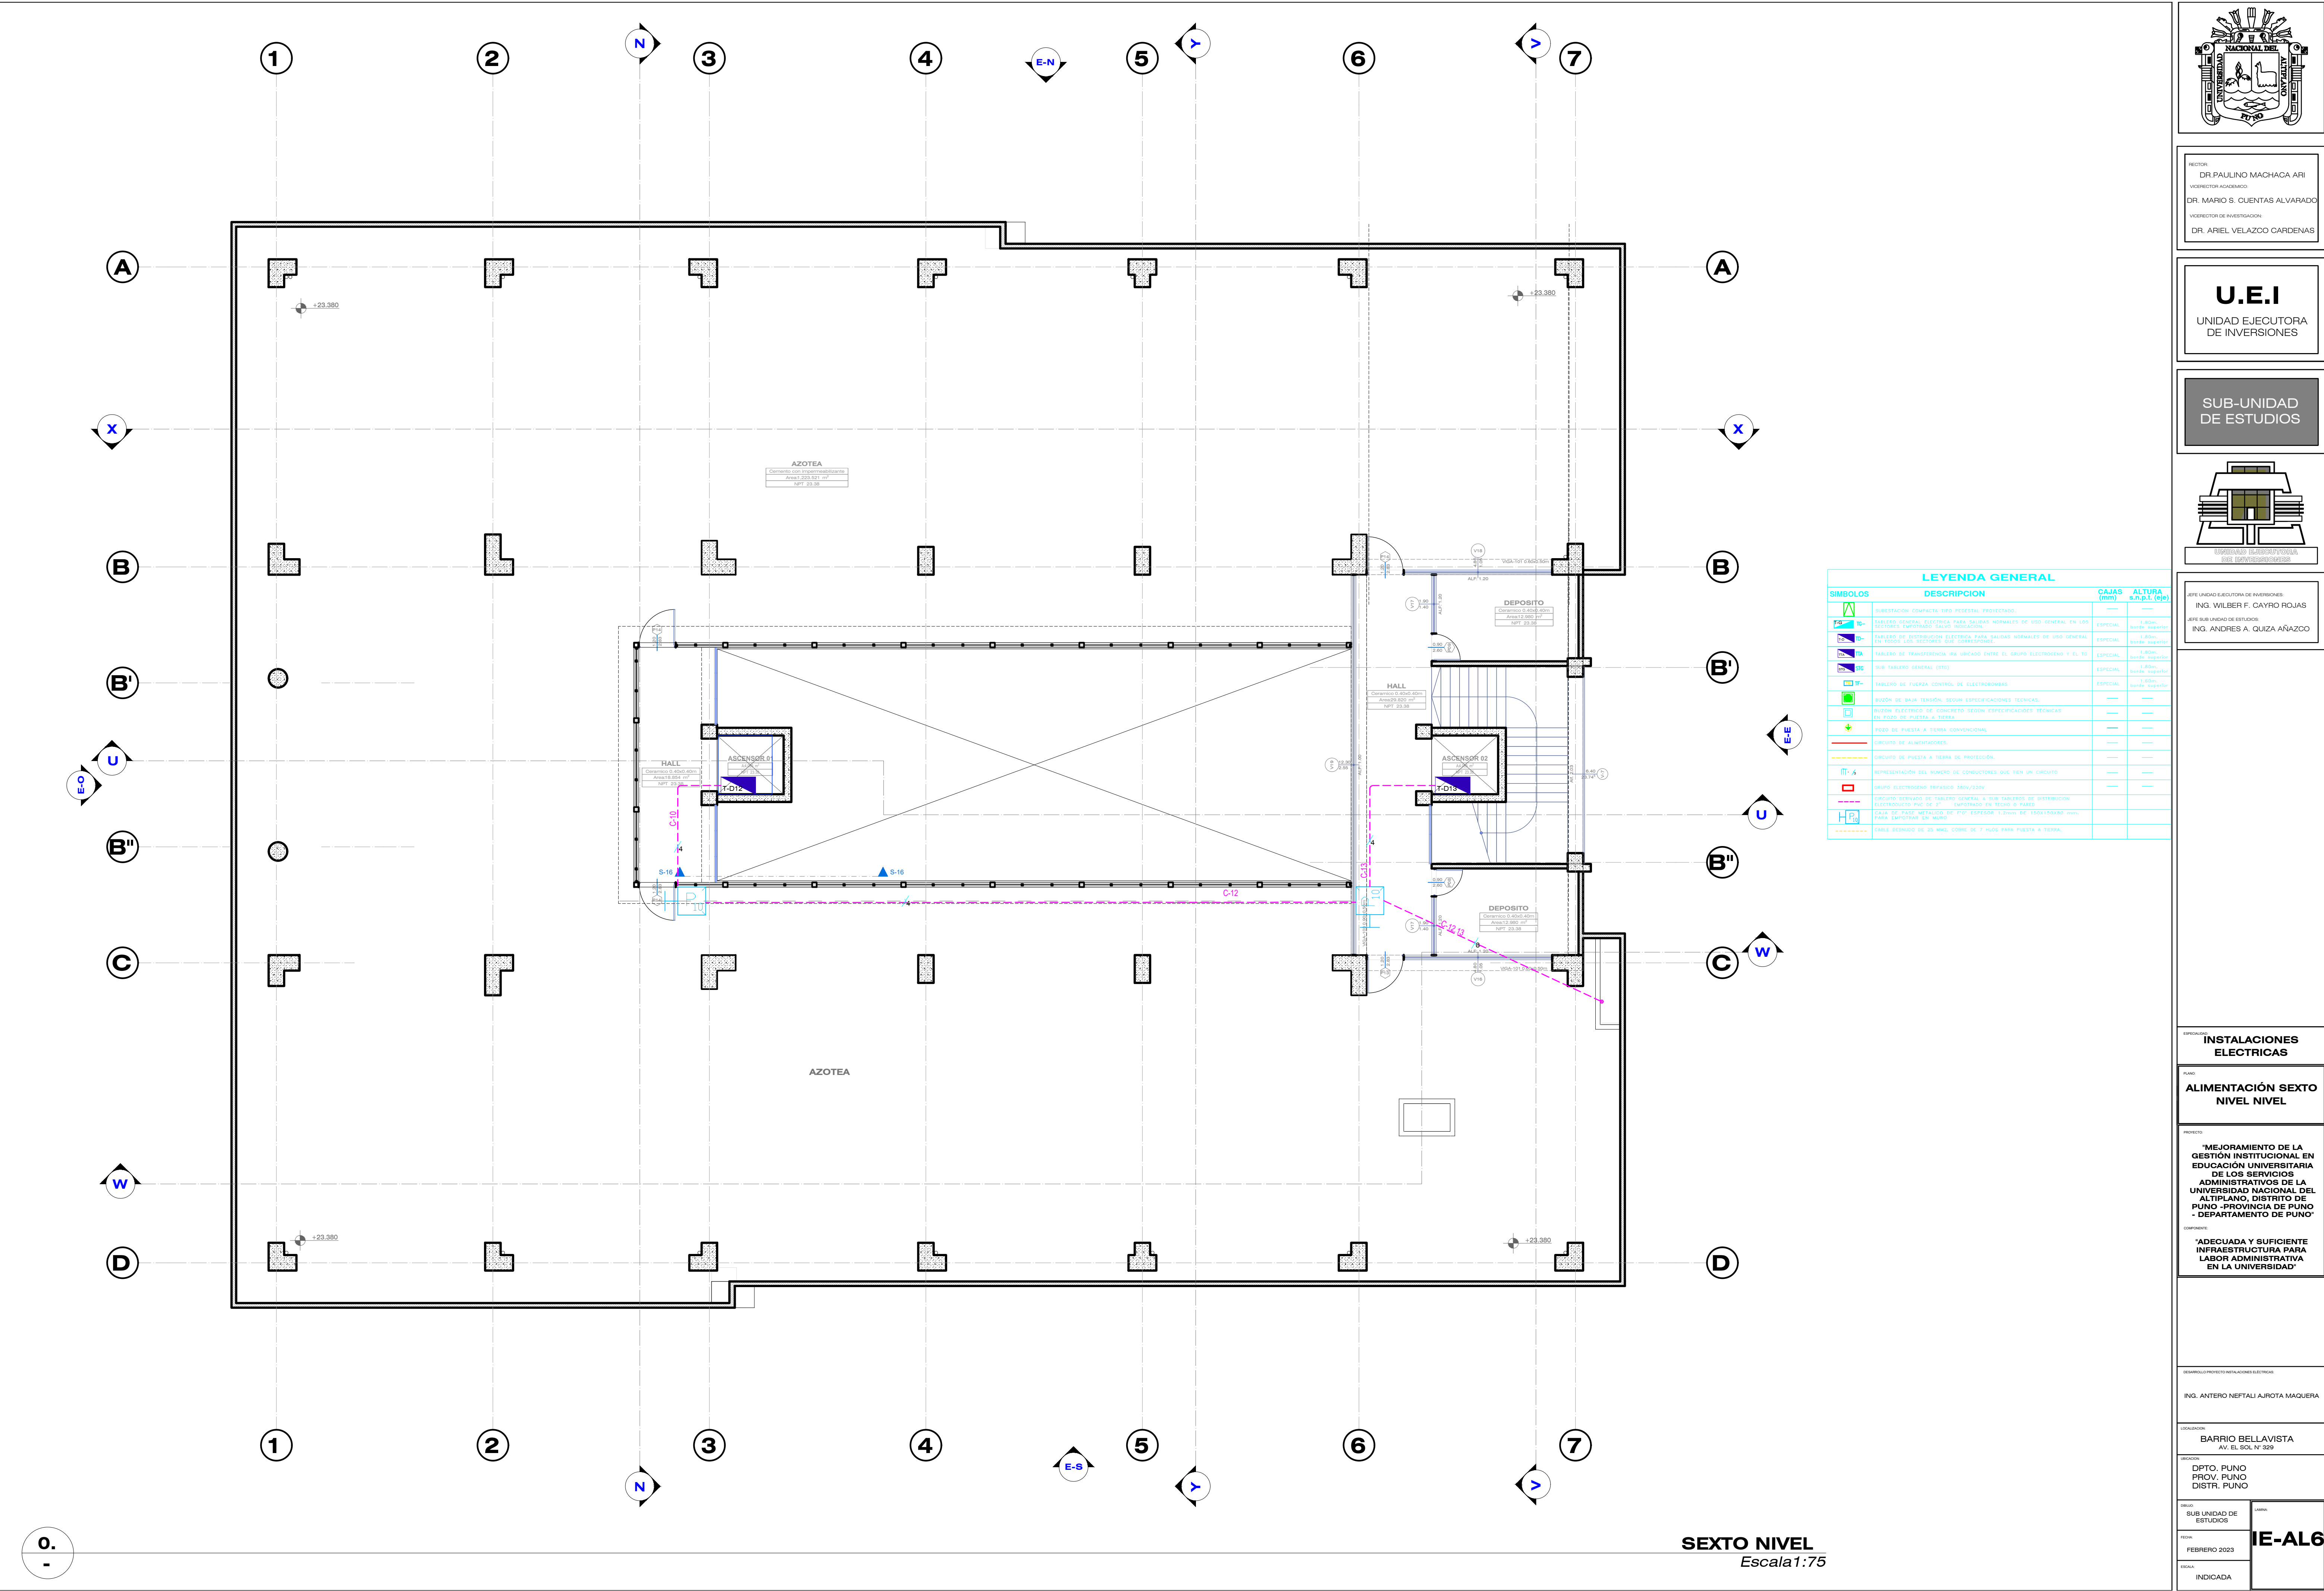

RECTOR:
DR. PAULINO MACHACA ARI
VICE-RECTOR ACADEMICO:
DR. MARIO S. CUENTAS ALVARADO
VICE-RECTOR DE INVESTIGACION:
DR. ARIEL VELAZCO CARDENAS

U.E.I
UNIDAD EJECUTORA
DE INVERSIONES

**SUB-UNIDAD
DE ESTUDIOS**

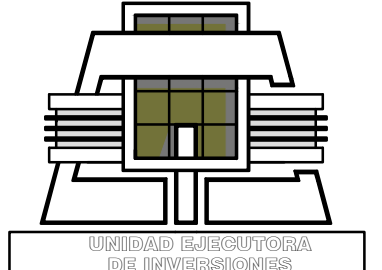

APRE. UNIDAD EJECUTORA DE INVERSIONES
ING. WILBER F. CAYRO ROJAS
APRE. SUB-UNIDAD DE ESTUDIOS
ING. ANDRES A. QUIZA ANAZCO

DISEÑADOR:
**INSTALACIONES
ELECTRICAS**

PLANO:
**ALIMENTACIÓN SEXTO
NIVEL NIVEL**

PROYECTO:
**"MEJORAMIENTO DE LA
GESTIÓN INSTITUCIONAL EN
EDUCACIÓN UNIVERSITARIA
DE LOS SERVICIOS
ADMINISTRATIVOS DE LA
UNIVERSIDAD NACIONAL DEL
ALTIPLANO, DISTRITO DE
PUNO -PROVINCIA DE PUNO
- DEPARTAMENTO DE PUNO"**

CONTRATANTE:
**"ADECUADA Y SUFICIENTE
INFRAESTRUCTURA PARA
LABOR ADMINISTRATIVA
EN LA UNIVERSIDAD"**

DISEÑADOR/PROYECTO/INSTALACIONES ELECTRICAS
ING. ANTERO NEFTALI AJIOTA MAQUERA

UBICACION:
**BARRIO BELLAVISTA
AV. EL SOL N° 329**

UBICACION:
**DPTO. PUNO
PROV. PUNO
DISTR. PUNO**

FECHA:
SUB-UNIDAD DE
ESTUDIOS
FECHA:
FEBRERO 2023
FECHA:
INDICADA

IE-AL6