


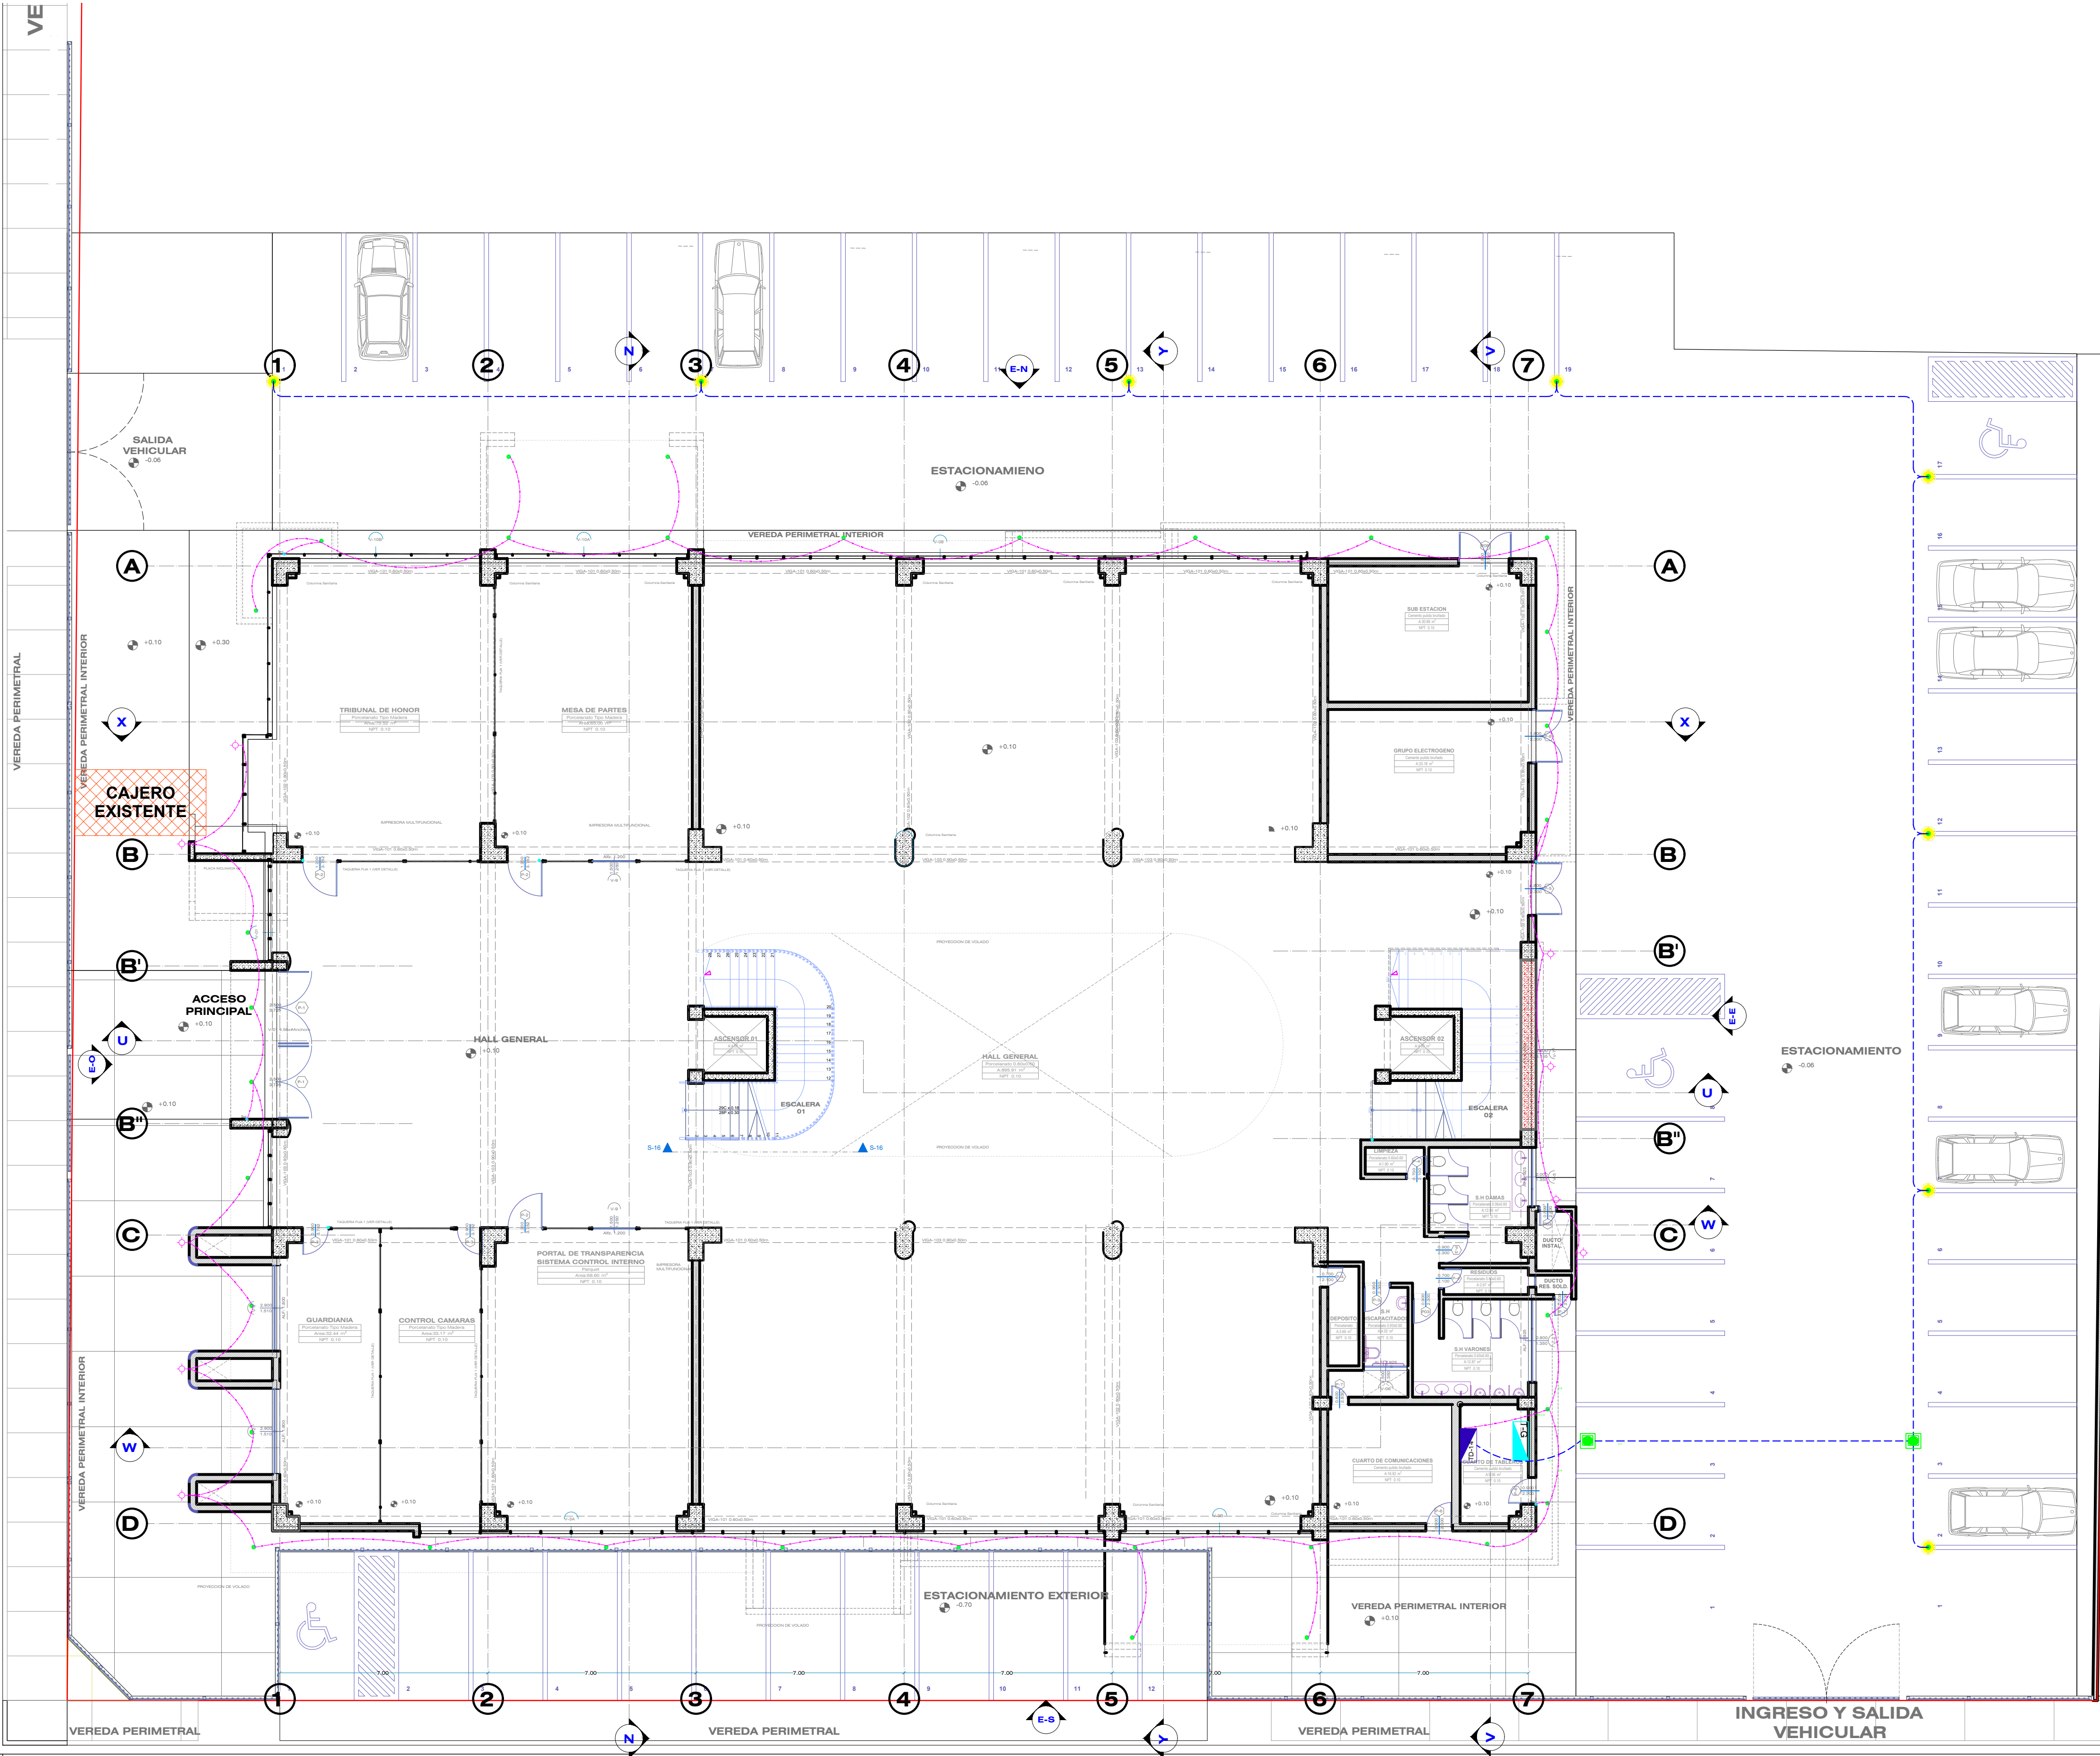

LEYENDA		
SEÑALIZACION	DESCRIPCION	NOTAS
	TABLERO GENERAL EMPOTRADO, CON BARRA DE COBRE PARA NEUTRO Y TIERRA - (T.D.)	1.00 Banda superior
	TABLERO DE DISTRIBUCION EMPOTRADO, CON BARRA DE COBRE PARA NEUTRO Y TIERRA - (T.D.)	1.00 Banda superior
	INDICADOR DE NUMERO DE CONDUCTORES EN EL DUCTO (FASE, NEUTRO, RETORNOS Y TIERRA)	...
	CIRCUITO DERIVADO CON CONDUCTOR LIBRE, DE SECCION INDICADA, EN ELECTRODUCTO PVC-P EMPOTRADO EN TECHO Y/O PARED	...
	CONDUCTO PVC DE 25mm	...
	PULSADOR SIMPLE	...
	LUMINARIA LED TIPO UNIMIGHT 15W	...
	REFLECTOR LED 1xLED3055W40 C P 200 W DE POTENCIA	...
	LUMINARIA LED TIPO ISLA 1xLED5491 T35 1xCG40-45/740 A C P 32 W DE POTENCIA	...
	ARTIFACTO LED EMPOTRABLE TIPO PANTALLA DE LUZ DIRECTA CON SISTEMA OPTICO FORMADO POR CUBIERTA DE ACRILICO SPAL, MODELO	...
	LED DE 40W DE 3000LM	...

JR. CANDELARIA


PRIMER NIVEL
Escala 1:75



RECTOR:
DR. PAULINO MACHACA ARI
VICERECTOR ACADEMICO:
DR. MARIO S. CUENTAS ALVARADO
VICERECTOR DE INVESTIGACION:
DR. ARIEL VELAZCO CARDENAS

U.E.I
UNIDAD EJECUTORA
DE INVERSIONES

SUB-UNIDAD
DE ESTUDIOS

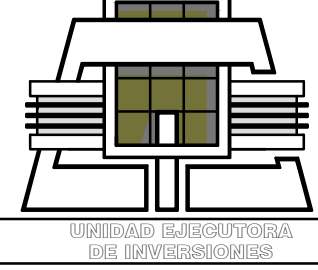

JEFE LA UNIDAD EJECUTIVA DE INVERSIONES
ING. WILBER F. CAYRO ROJAS
JEFE SUB-UNIDAD DE ESTUDIOS
ING. ANDRES A. QUIZA ANAZCO

INSTALACIONES
ELECTRICAS

PRIMER NIVEL

PROYECTO
"MEJORAMIENTO DE LA
GESTION INSTITUCIONAL EN
EDUCACION UNIVERSITARIA
DE LOS SERVICIOS
ADMINISTRATIVOS DE LA
UNIVERSIDAD NACIONAL DEL
ALTIPLANO, DISTRITO DE
PUNO -PROVINCIA DE PUNO
- DEPARTAMENTO DE PUNO"

CONTRATANTE
"ADECUADA Y SUFICIENTE
INFRAESTRUCTURA PARA
LABOR ADMINISTRATIVA
EN LA UNIVERSIDAD"

DISEÑADOR
ING. ANTERO NEFTALI AJROTA MAQUERA

UBICACION
BARRIO BELLAVISTA
AV. EL SOL N° 329

REGION
DPTO. PUNO
PROV. PUNO
DISTR. PUNO

FECHA
FEBRERO 2023

INDICADA

IE-EXT 1