


PLANO ELECTRICO PRELIMINAR - PISO 2

Casa de Aquiles - sobre base arquitectonica piso2_v3.dxf

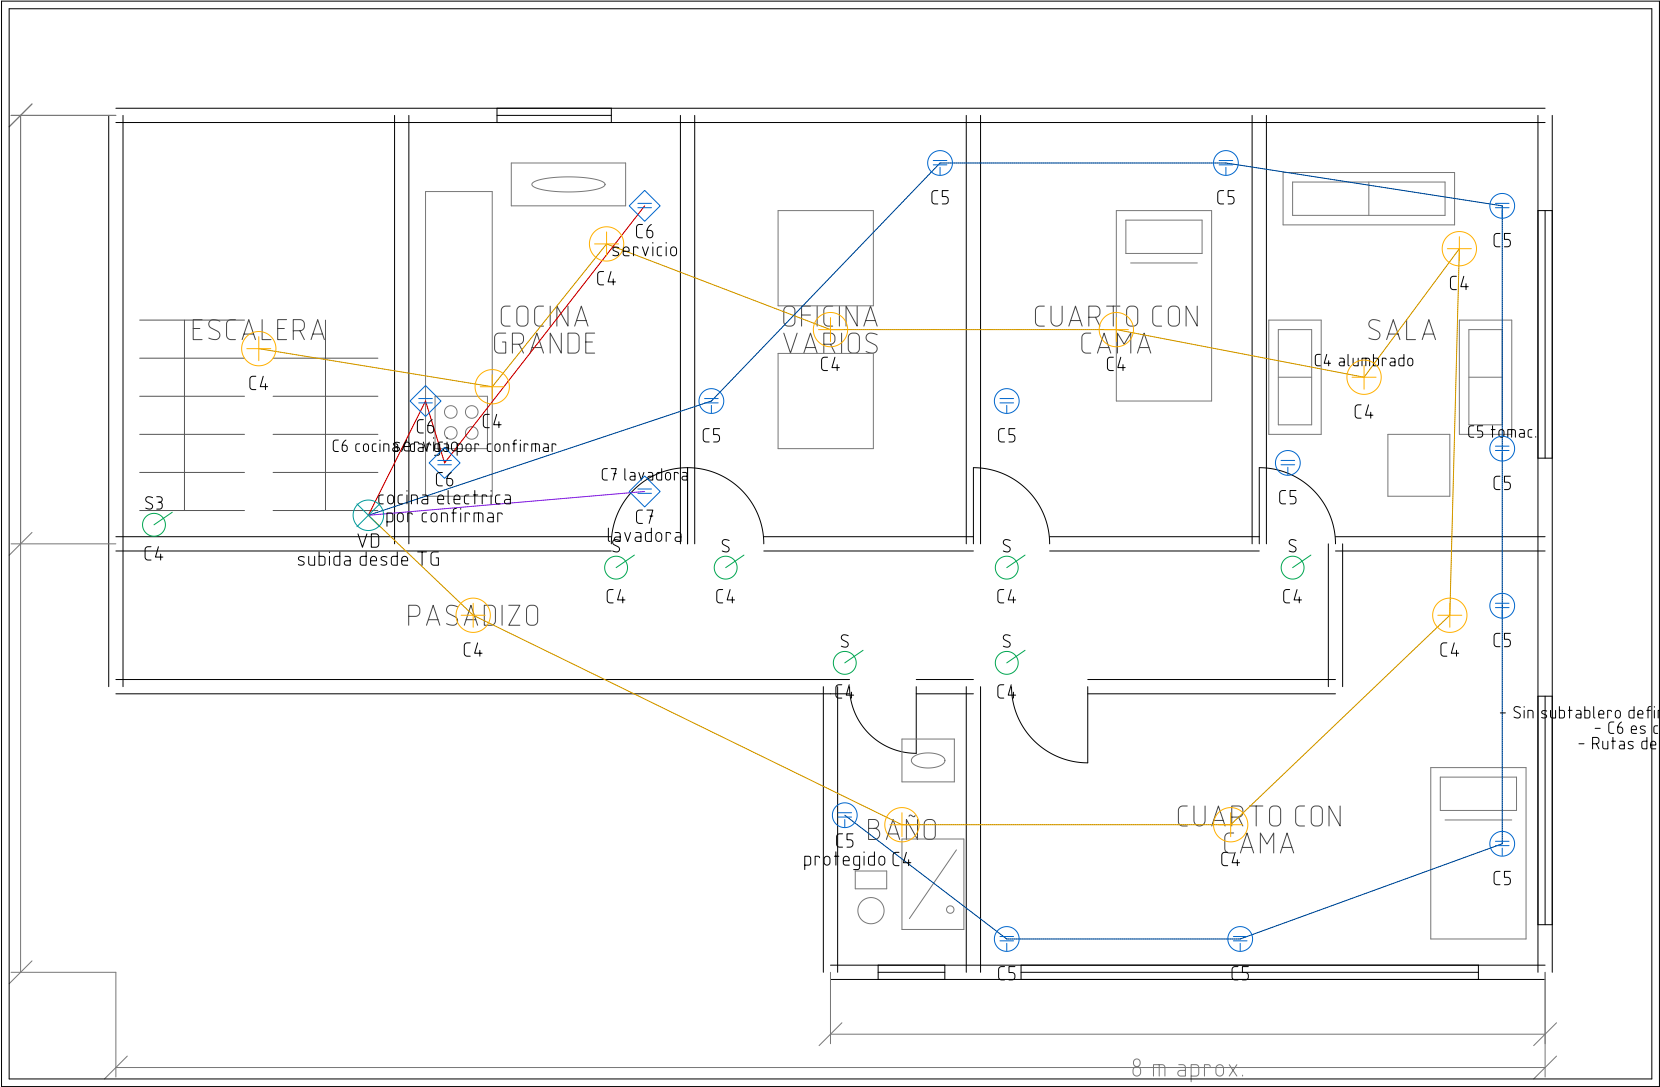

LEYENDA ELECTRICA

- Luminaria de techo
- Interruptor simple
- Tomacorriente
- Tomacorriente especial
- Tablero general
- Medidor

Circuitos:

- C4: Alumbrado segundo piso
- C5: Tomacorrientes segundo piso
- C6: Cocina/carga especial por confirmar
- C7: Lavadora segundo piso
- VD: Subida referencial desde TG

Notas:
- Sin subtablero definido; se grafica VD como subida desde TG.
- C6 es carga de cocina por confirmar.
- Rutas de canalizacion son referenciales.