CL-07-S4 | Planta del segmento 4: referencias y sitios a verificar

Eje KML en azul; PC: estructura GIS de referencia; PN: sitio por replantear; CV: alerta OSM

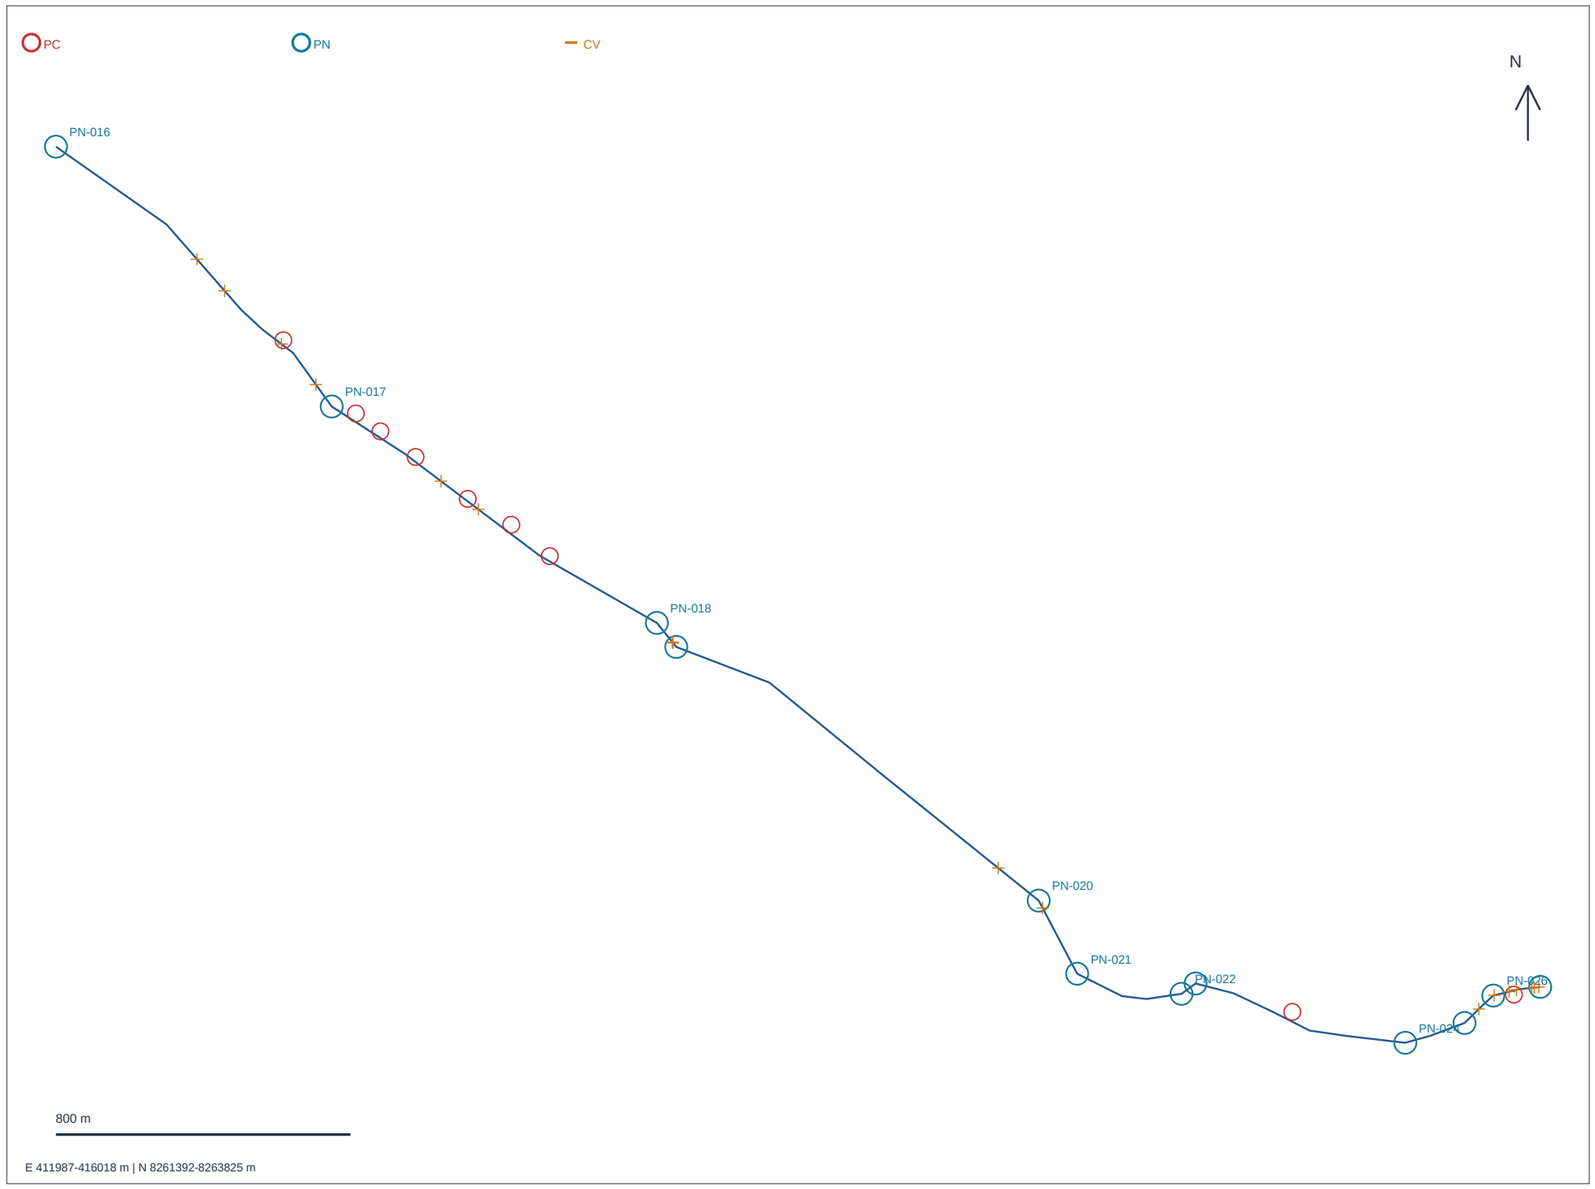

E 411987-416018 m | N 8261392-8263825 m

Marcas PC/PN son cartograficas; PN no representa poste aprobado.

CUADRO DE PUNTOS | progresiva según cada fuente

PC | 9 referencias GIS; PK acumulado GIS; validar existencia

ID / GISEM o funcion	PK m	E	N
PC-032 NMT000027976	9783	412604	8263299
PC-033 NMT000508204	10070	412801	8263100
PC-034 NMT000488510	10152	412868	8263052
PC-035 NMT000027453	10270	412964	8262982
PC-036 NMT000027452	10451	413105	8262868
PC-037 NMT000027977	10588	413223	8262798
PC-038 NMT000027470	10724	413328	8262713
PC-039 NMT000027972	13205	415345	8261476
PC-040 NMT000027964	13865	415946	8261522

PN | 12 sitios candidatos; PK acumulado KML; NO instalar

ID / GISEM o funcion	PK m	E	N
PN-016 extremo de segment	8967	411987	8263825
PN-017 cambio de direcció	10005	412736	8263119
PN-018 cambio de direcció	11067	413619	8262532
PN-019 cambio de direcció	11151	413671	8262466
PN-020 cambio de direcció	12362	414656	8261778
PN-021 cambio de direcció	12587	414760	8261579
PN-022 cambio de direcció	12886	415044	8261525
PN-023 cambio de direcció	12933	415082	8261553
PN-024 cambio de direcció	13532	415651	8261392
PN-025 cambio de direcció	13702	415812	8261445
PN-026 cambio de direcció	13810	415890	8261520
PN-027 fin de corredor; t	13940	416018	8261543

UTM EPSG:32719 (m); lat/lon y fuente en CSV PC/PN.

PC: PK GIS. PN: PK acumulado KML sin sumar brechas.

ANTEPROYECTO ACADEMICO - NO APTO PARA CONSTRUCCION

WGS84 / UTM 19S EPSG:32719 | Modelo DXF en metros | Presentacion A3 en milimetros