PERFIL TOPOGRÁFICO LONGITUDINAL, DISTRIBUCIÓN DE ESTRUCTURAS Y CATENARIAS — LÍNEA PRIMARIA 22.9 kV

CONDUCCIÓN: CONDUCTOR AAAC 35 mm² | LÍNEA VERDE: DISTANCIA MÍNIMA DE SEGURIDAD CNE (6.50 m SOBRE SUELO)

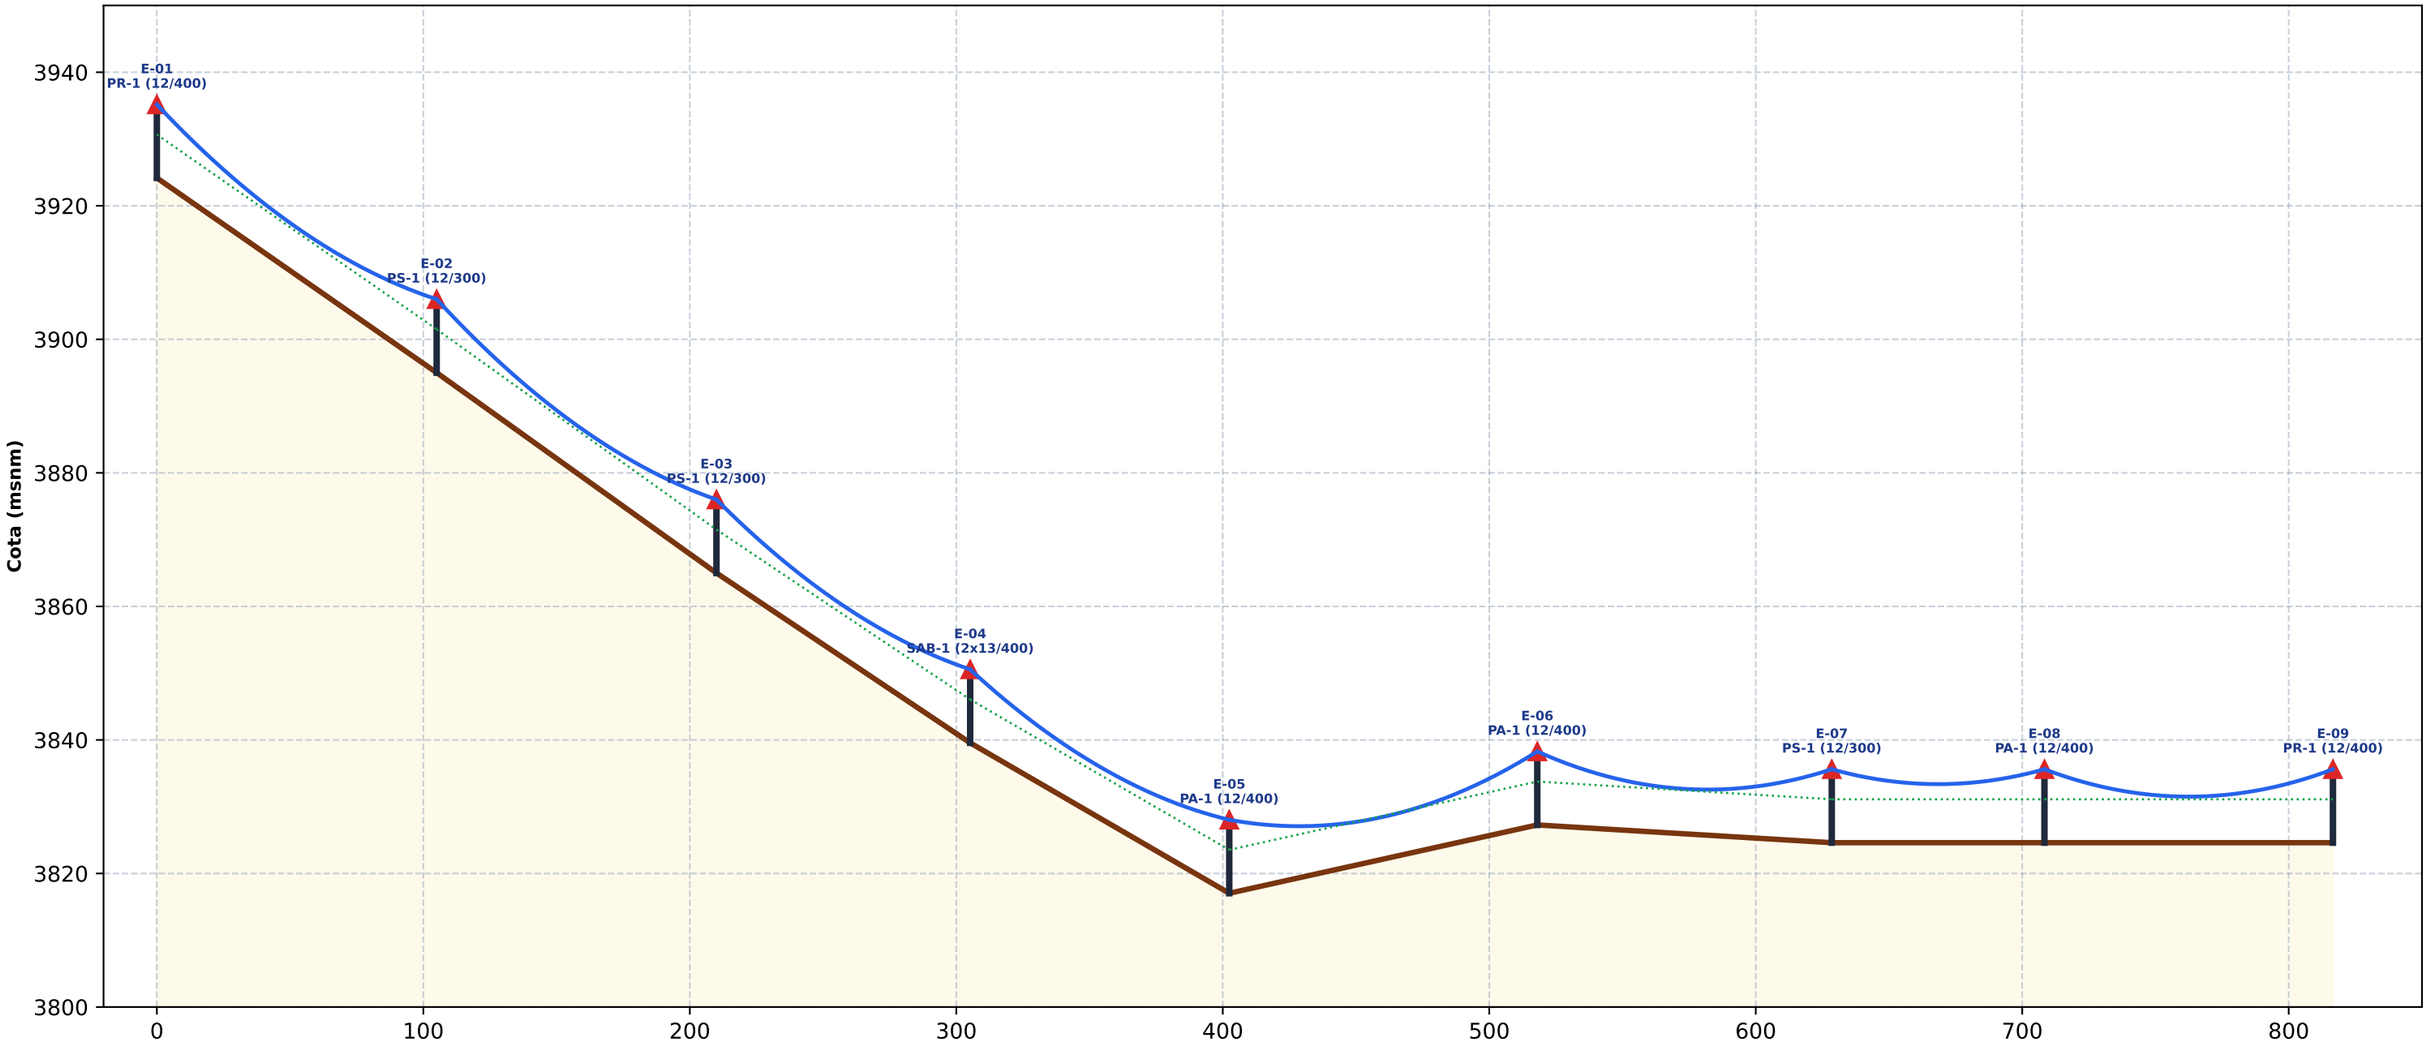

ESTRUCTURA	E-01	E-02	E-03	E-04	E-05	E-06	E-07	E-08	E-09
ARMADO DGE	PR-1	PS-1	PS-1	SAB-1	PA-1	PA-1	PS-1	PA-1	PR-1
POSTE C.A.C.	12/400	12/300	12/300	2x13/400	12/400	12/400	12/300	12/400	12/400
COTA TERRENO (m)	3924.2	3895.0	3865.0	3839.6	3817.0	3827.3	3824.6	3824.6	3824.6
VANO PARCIAL (m)	0.0	105.0	105.0	95.2	97.2	115.6	110.5	79.8	108.3
PROGRESIVA (m)	0.0	105.0	210.0	305.2	402.4	518.0	628.5	708.3	816.6
RETENIDA / PAT	RET / PAT	---	---	RET / PAT	RET	RET	---	RET	RET / PAT

UNIVERSIDAD NACIONAL DEL ALTIPLANO — PUNO
FACULTAD DE INGENIERÍA MECÁNICA ELÉCTRICA, ELECTRÓNICA Y SISTEMAS

ESCUELA PROFESIONAL DE INGENIERÍA MECÁNICA ELÉCTRICA
CURSO: MEC330 — INSTALACIONES ELÉCTRICAS II (SEMESTRE 2026-II)

PROYECTO: LP 22.9 kV Y RED SECUNDARIA SED 100 kVA SECTOR CHIFRÓN
DISTRITO DE CAPACHICA — PROVINCIA Y DEPARTAMENTO DE PUNO

PLANO: PERFIL LONGITUDINAL TOPOGRÁFICO Y DISTRIBUCIÓN DE ESTRUCTURAS LP 22.9 kV

RESPONSABLE: Br. Renzo Gabriel Mamani Galindo (Cód. 228447)
DOCENTES: Ing. Leonidas Vilca Callata / Ing. Marcos José Villanueva Cornejo

FECHA:	ESCALA:	LÁMINA:
Octubre 2026	H: 1/2000 | V: 1/500	PL-01