

NOTAS: Cotas en mm. Ferretería de acero galvanizado en caliente (ASTM A153/A123).
Fase superior a 0,30 m sobre la cabeza; cruceta a 1,40 m bajo la cabeza (conductores inferiores a 1,10 m).
La numeración de los globos corresponde al orden de la lista de materiales.

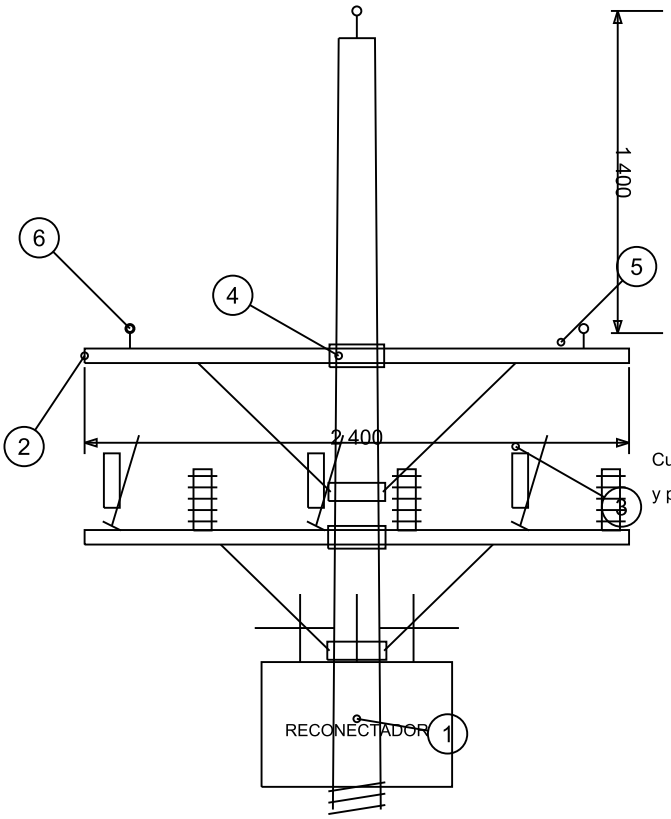

VISTA FRONTAL

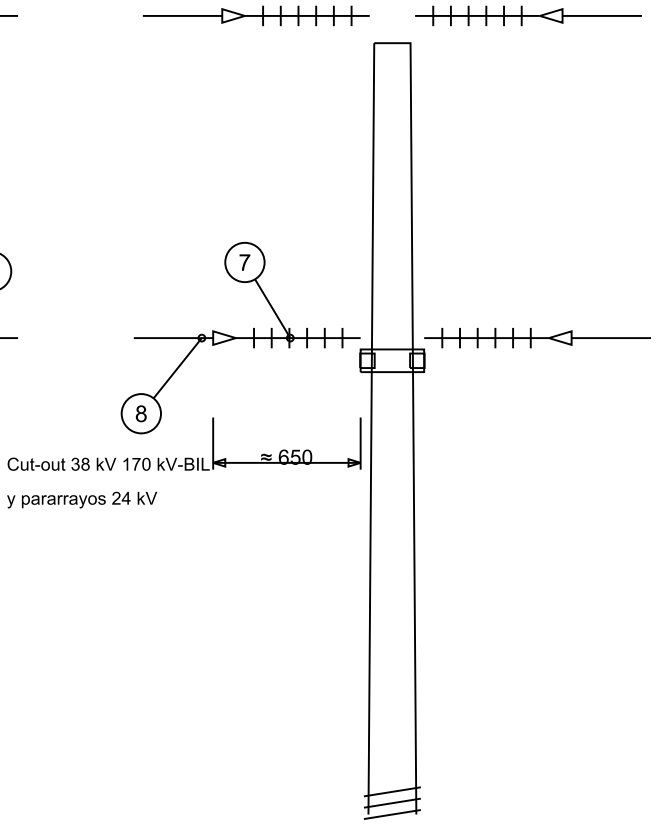

VISTA LATERAL (EN EL SENTIDO DE LA LÍNEA)

LISTA DE MATERIALES

ITEM	DESCRIPCIÓN	UND.	CANT.
1	Poste de C.A.C. 12/400 daN, con perilla	u	1
2	Cruceta de perfil angular FºGº de 64 x 64 x 2400 mm, E = 6,4 mm, con 02 dados. TIPO I	u	3
3	Riostra de perfil angular FºGº de 64 x 64 x 1000 mm, E = 6,4 mm	u	5
4	Abrazadera tipo CAS doble de 75 mm, E = 6,4 mm, D = 206 mm	u	1
5	Perno de doble armado de AºGº de 16 mm ⌀ x 508 mm, c/4 tuercas y arandelas	u	4
6	Perno maquinado de AºGº L = 50 mm, D = 13 mm, c/T/C/2A/AP	u	4
7	Arandela cuadrada plana de AºGº 57 x 57 x 5 mm, agujero 18 mm ⌀	u	16
8	Soporte metálico de FºGº para montaje de reconectador en poste, con accesorios	u	1
9	Tuerca ojo de AºGº para perno de 16 mm ⌀	u	3
10	Perno ojo de AºGº de 16 mm ⌀ x 254 mm, con tuerca y contratuerca	u	1
11	Perno de AºGº de 16 mm ⌀ x 254 mm, con tuerca y contratuerca	u	2
12	Aislador polimérico tipo suspensión 36 kV, conexión horquilla-lengüeta (línea de fuga ≥ 720 mm)	u	3
13	Grillete de AºGº tipo lira de 16 mm ⌀, con pasador de seguridad	u	3
14	Grapa de anclaje tipo pistola de 3 pernos para conductor AAAC 35–70 mm²	u	3
15	Conector doble vía Al/Al para conductor 35–70 mm², tres pernos	u	6
16	Conector bimetálico Al/Cu para conexión de equipos	u	6
17	Seccionador fusible unipolar tipo expulsión (cut-out) de 38 kV, 100 A, 170 kV-BIL	u	3
18	Fusible tipo expulsión tipo K para el seccionamiento del reconectador (calibre según Vol. IX)	u	3
19	Pararrayos de óxido metálico 24 kV, 10 kA, clase 1, MCOV 19,5 kV, línea de fuga ≥ 780 mm	u	3
20	Reconectador automático trifásico 38 kV, 170 kV-BIL, 630 A, 12,5 kA, con control electrónico y TT auxiliar	u	1
21	Conductor AAAC 70 mm² para puentes y conexión a equipos	m	15

DISEÑO : —	PROYECTISTA: RENZO GABRIEL MAMANI GALINDO	ESCALA : 1:30
REVISÓ : —	LÍNEA PRIMARIA 22,9 kV TRIFÁSICA CAPACHICA – LLACHÓN	LÁMINA N.°
FECHA : OCTUBRE 2026	ARMADO CON RECONECTADOR (ARRANQUE) TIPO PSER-3	LD-LP-06