
NOTAS: Tiro máximo de trabajo por retenida 15,15 kN; FS cable ≥ 2,0; FS bloque ≥ 2,0 (Anexo 7).
La retenida se instalará en la bisectriz del ángulo o en la prolongación del alineamiento (anclajes y terminales).

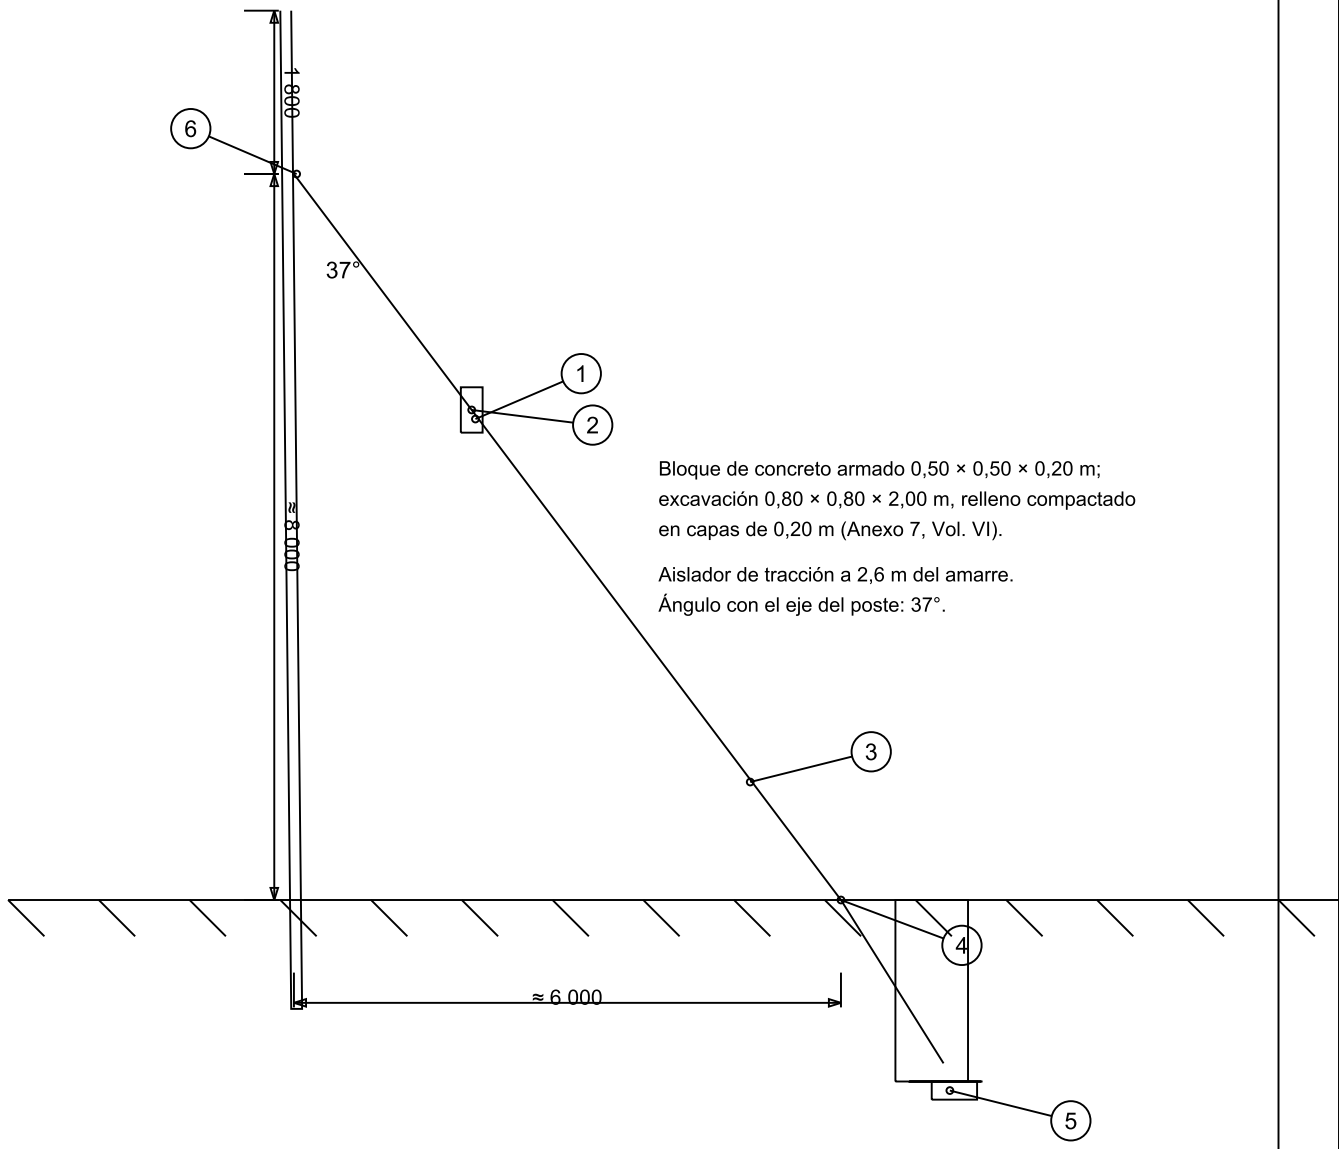

RETENIDA INCLINADA – ELEVACIÓN

LISTA DE MATERIALES

ITEM	DESCRIPCIÓN	UND.	CANT.
1	Varilla de anclaje de AºGº de 16 mm ⌀ x 2,40 m, con ojal guardacabo, tuerca y contratuerca	u	1
2	Grapa paralela de doble vía de FºGº de tres pernos	u	2
3	Abrazadera de FºGº 185 mm ⌀ x 64 mm x 6,4 mm, tipo partida, c/3 pernos 16 mm ⌀	u	1
4	Aislador polimérico de tracción para retenida 36 kV	u	1
5	Arandela de anclaje cuadrada plana de FºGº 102 x 102 x 6,4 mm, agujero 20 mm	u	1
6	Guardacabo de FºGº de 16 mm para cable de 10 mm	u	2
7	Guardacable de FºGº de 1,80 mm x 2,40 m, incluye accesorios de fijación	u	1
8	Bloque de concreto armado 0,50 x 0,50 x 0,20 m	u	1
9	Alambre galvanizado de entorche N.° 14 para amarre	m	1,5
10	Cable de acero 10 mm ⌀, 7 hilos, grado Siemens-Martin (poste 12 m / 13 m)	m	14,0 / 15,1

DISEÑO : —	PROYECTISTA: RENZO GABRIEL MAMANI GALINDO	ESCALA : 1:80
REVISÓ : —	LÍNEA PRIMARIA 22,9 kV TRIFÁSICA CAPACHICA – LLACHÓN	LÁMINA N.°
FECHA : OCTUBRE 2026	RETENIDA INCLINADA TIPO RI	LD-LP-08