

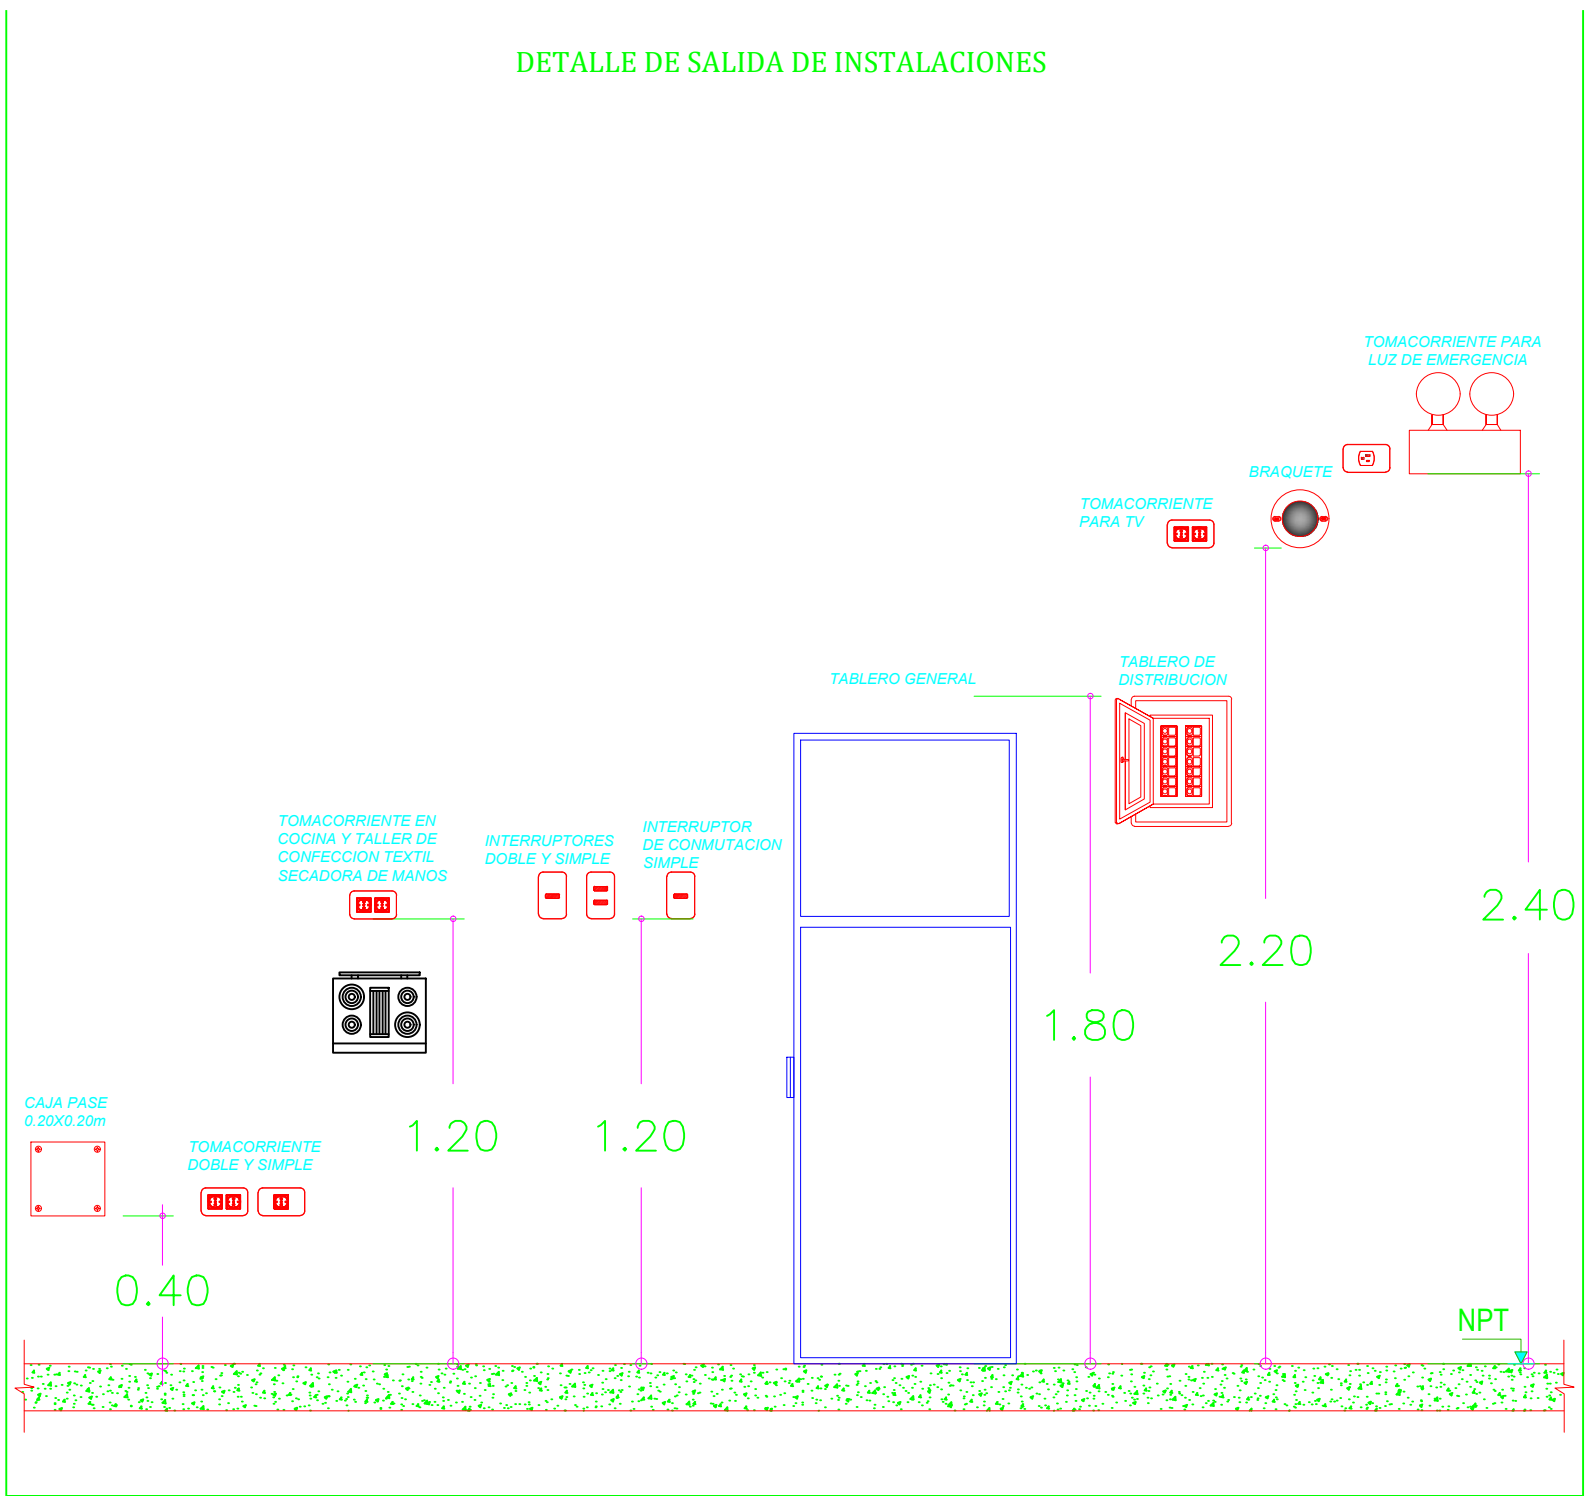
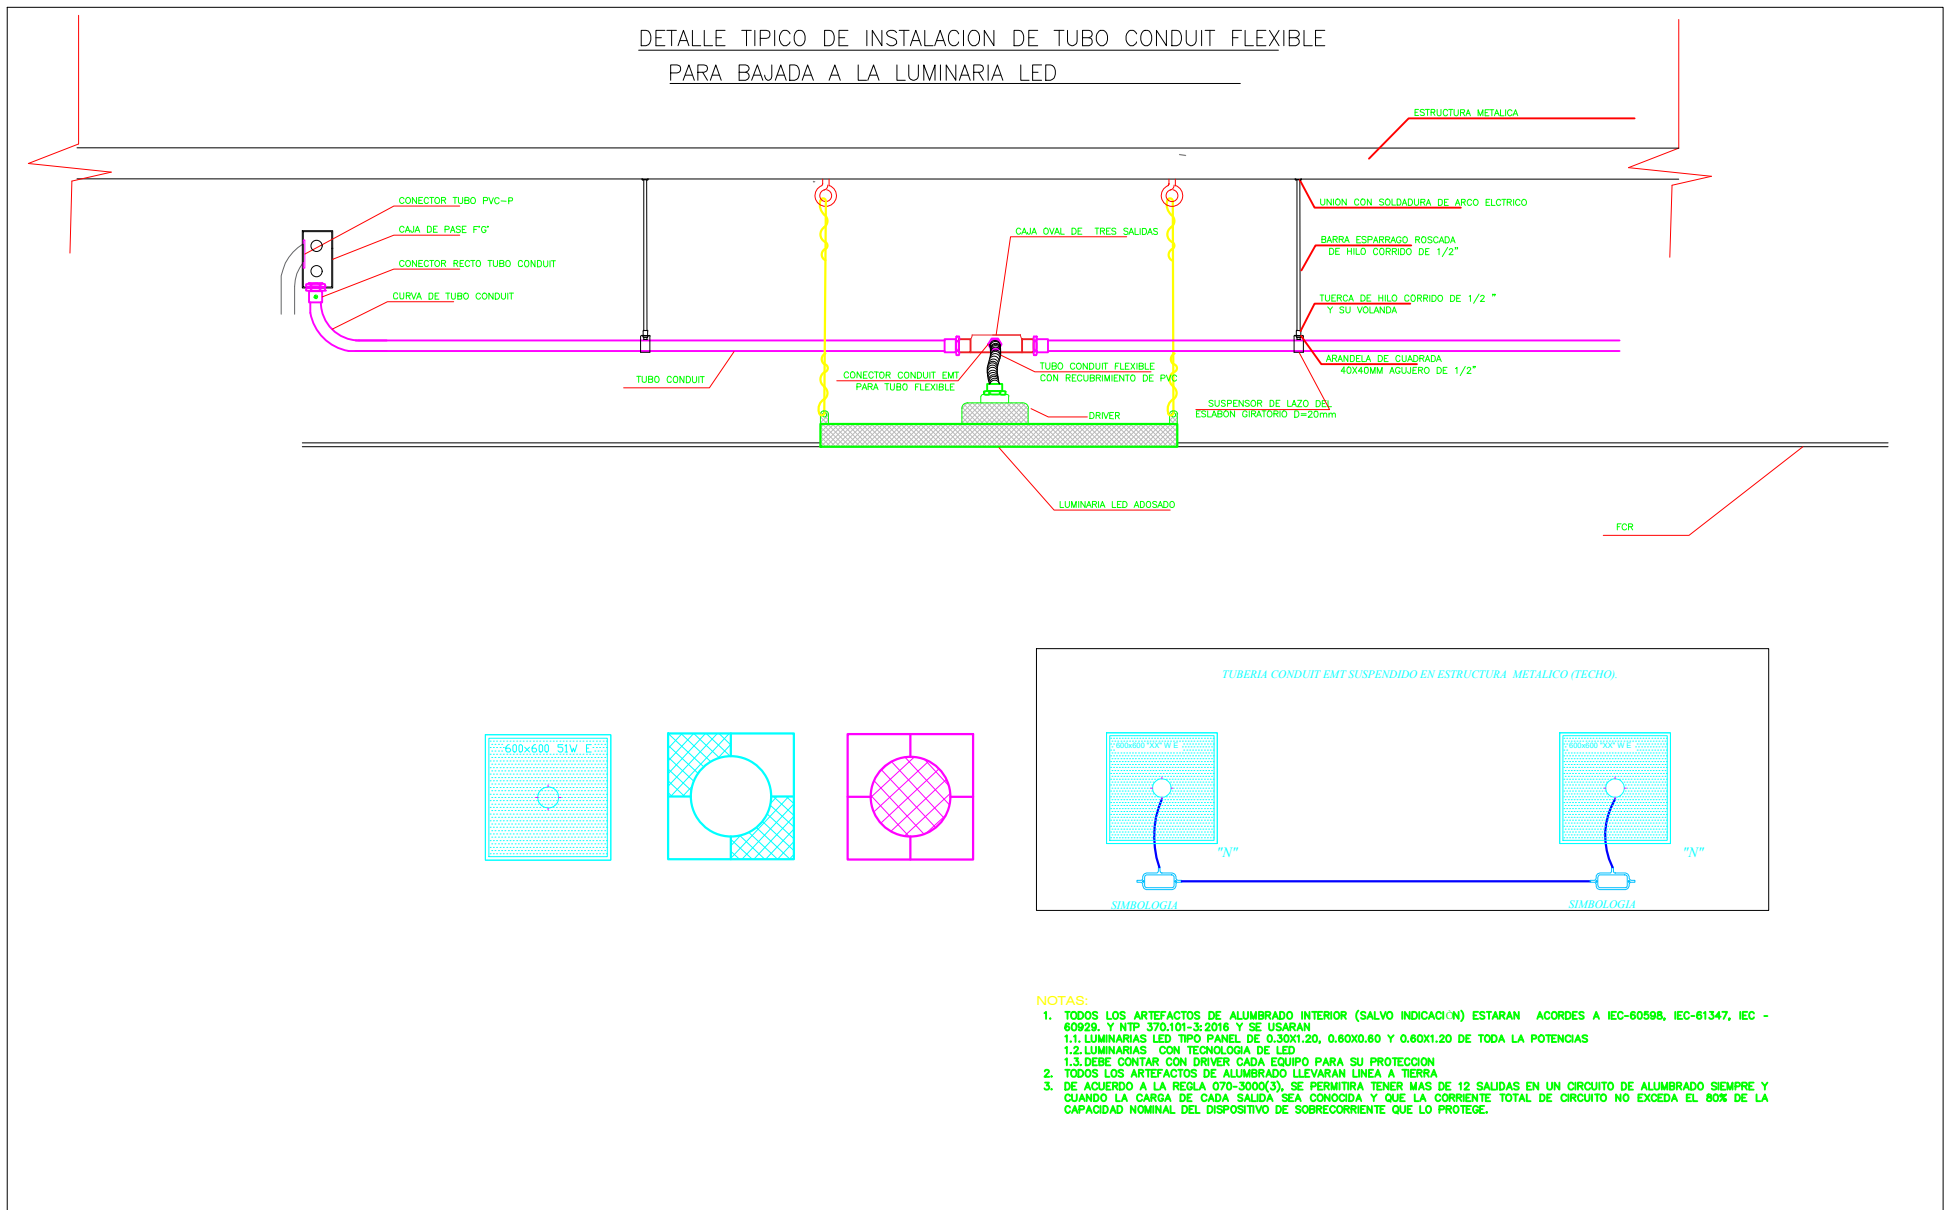
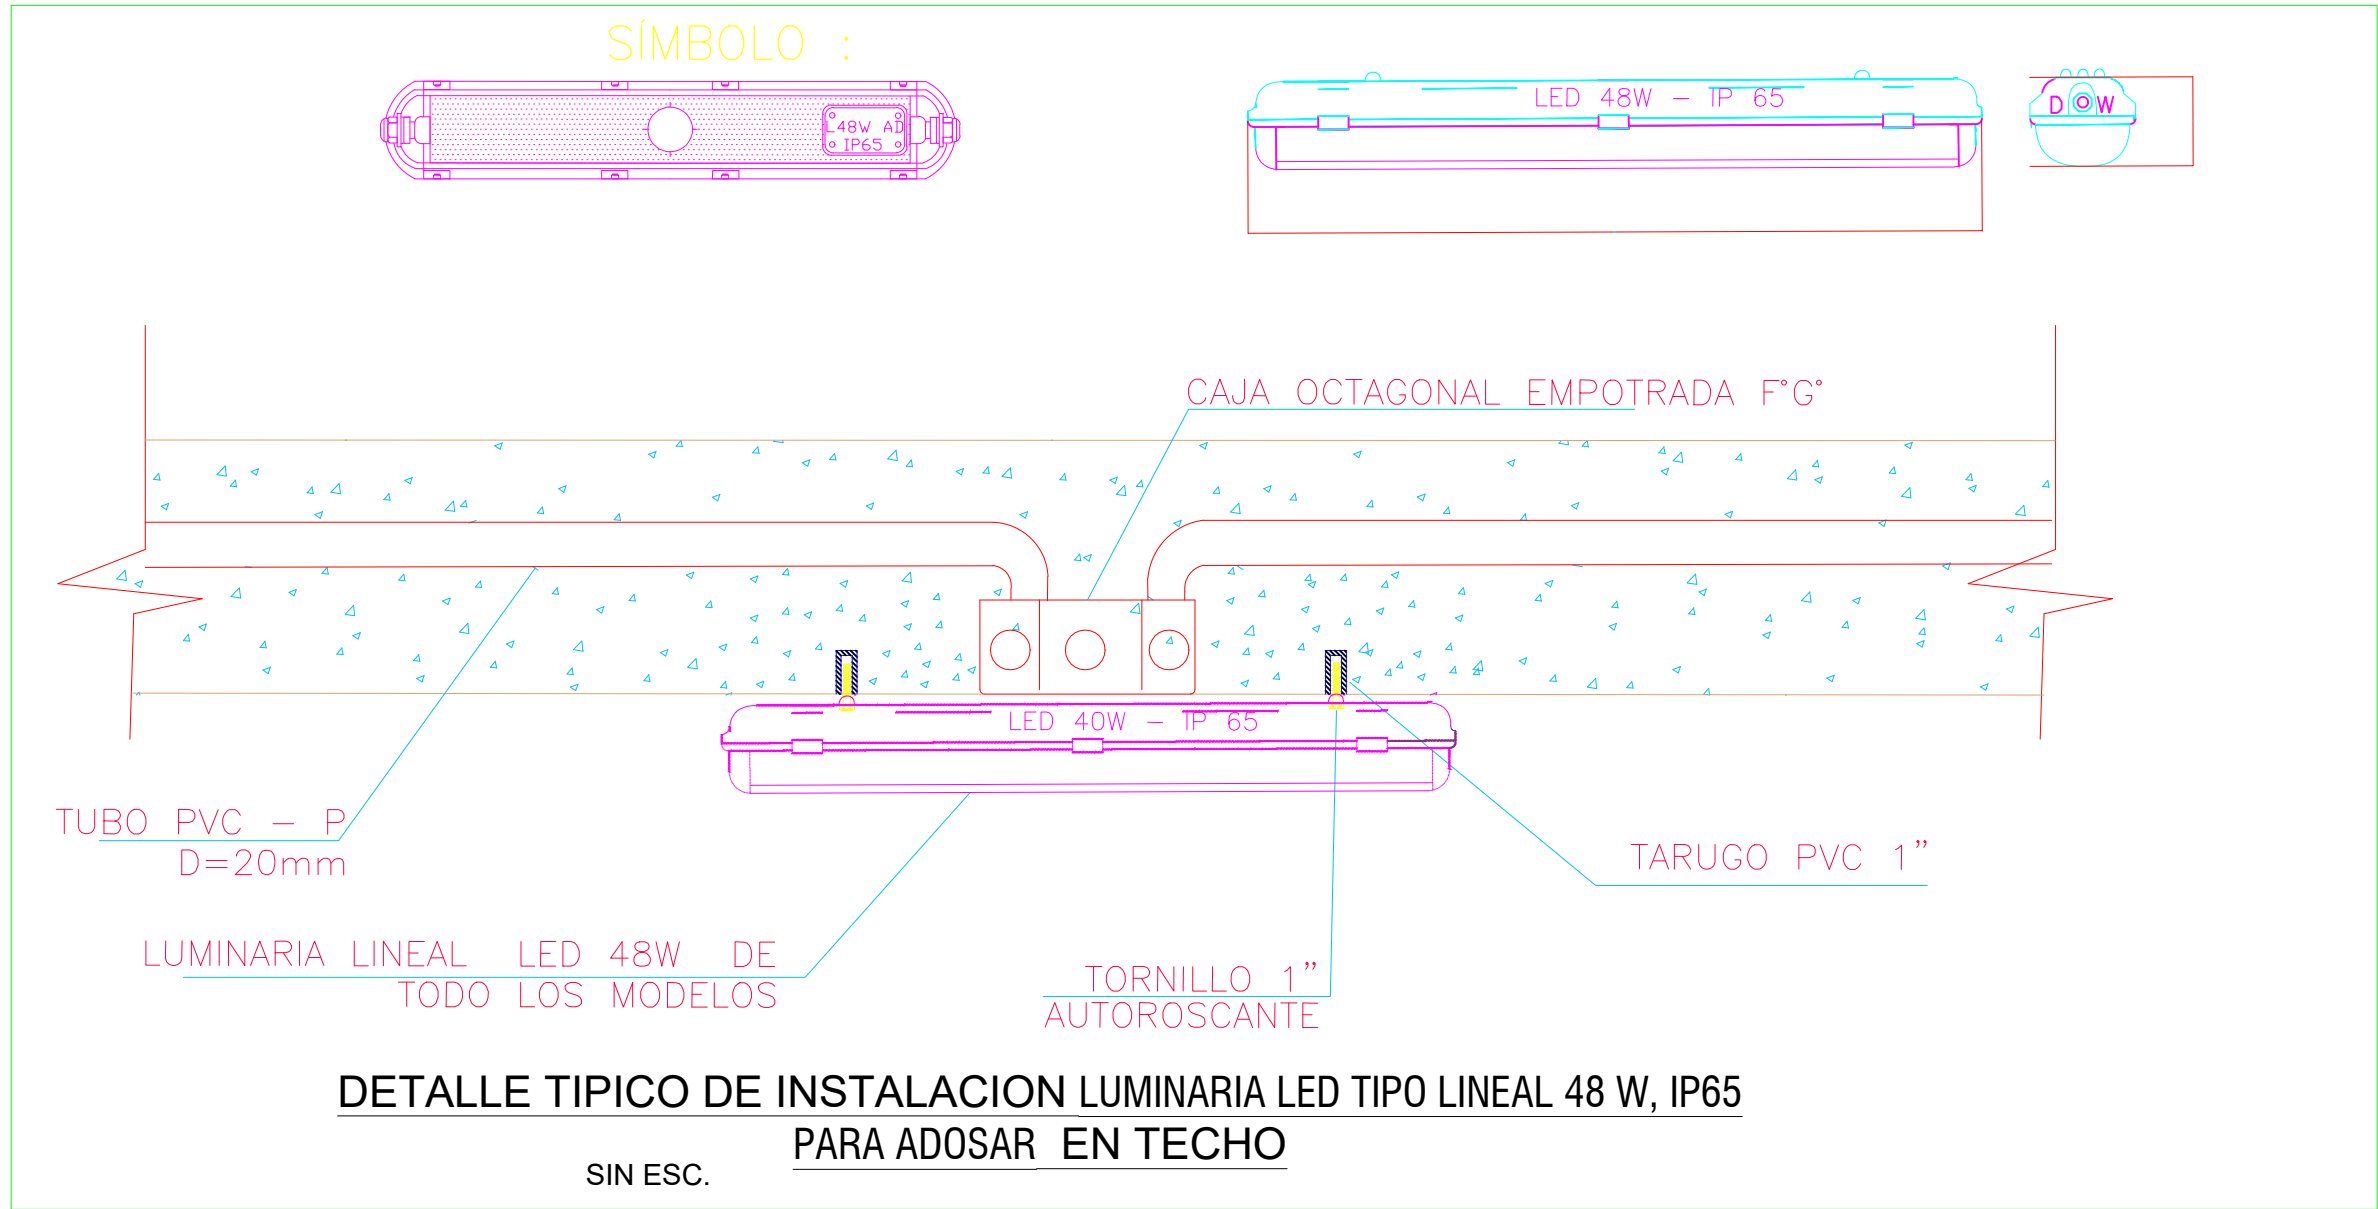
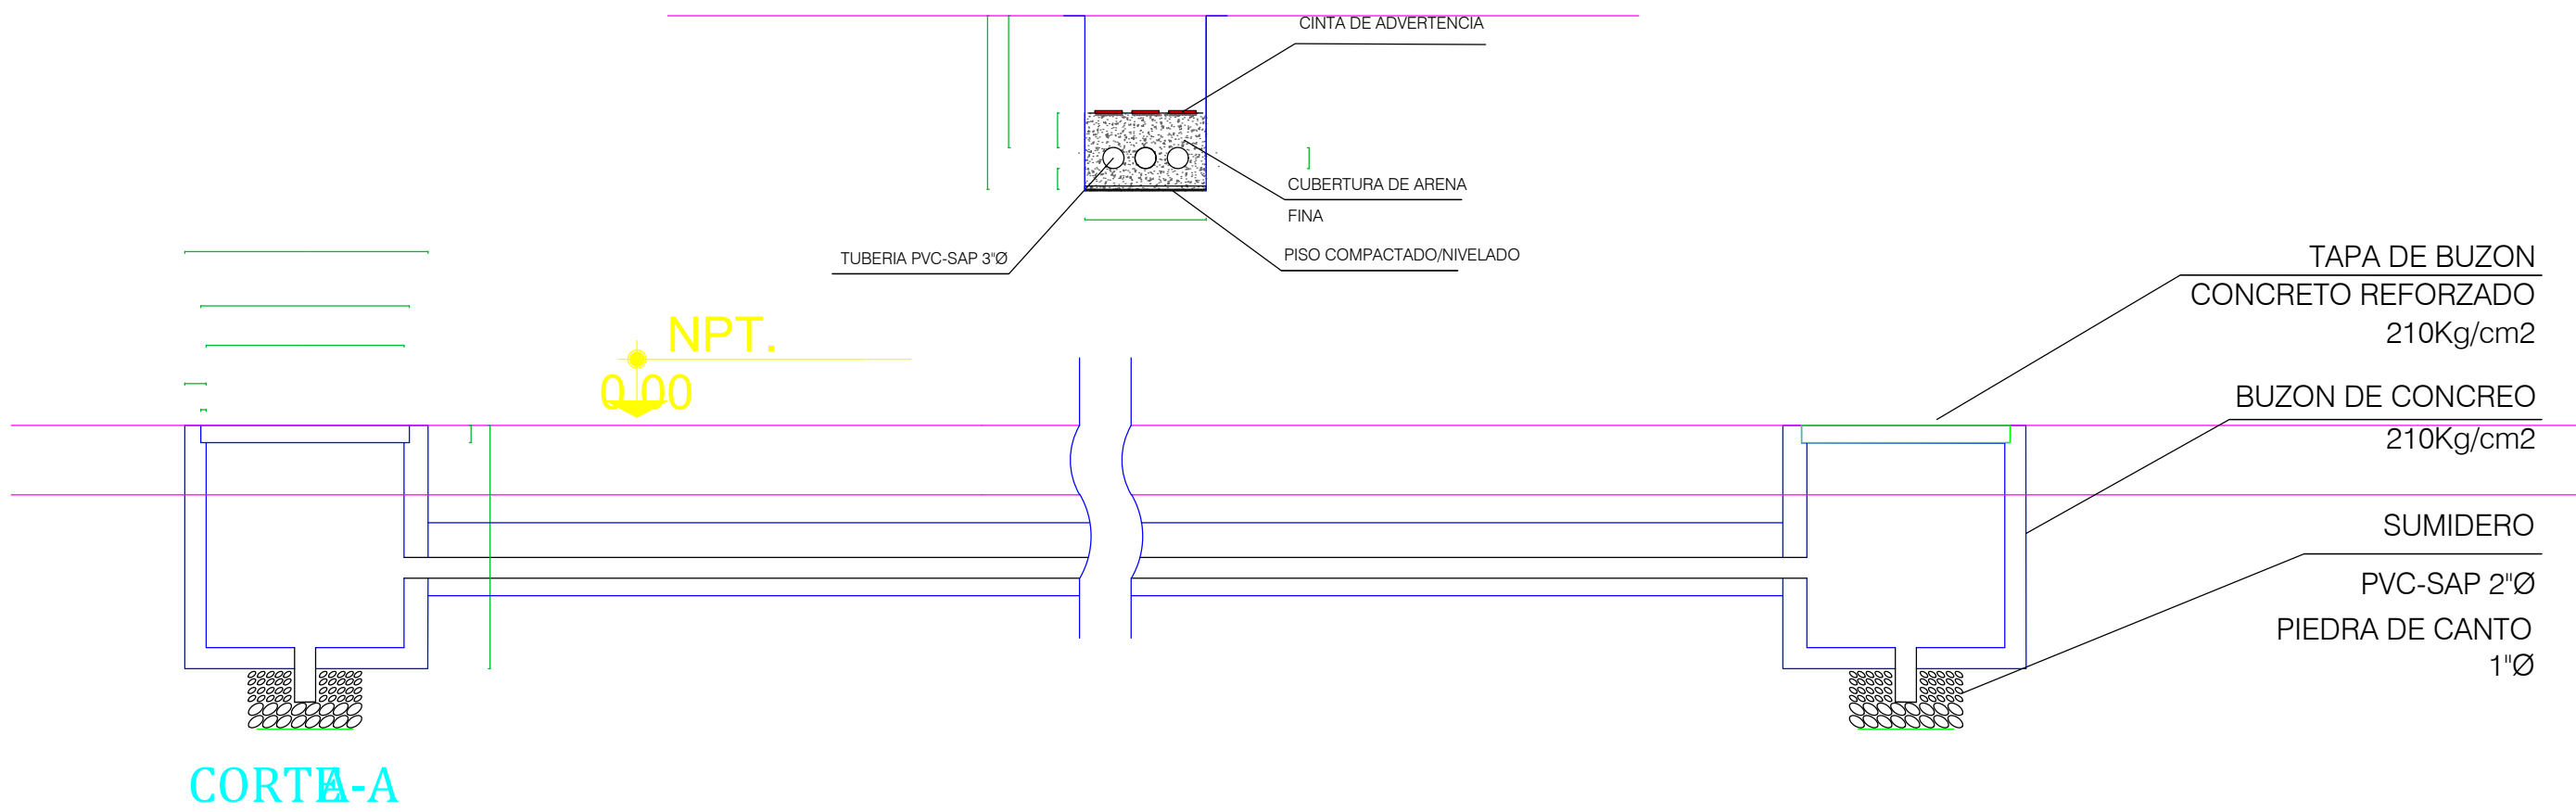


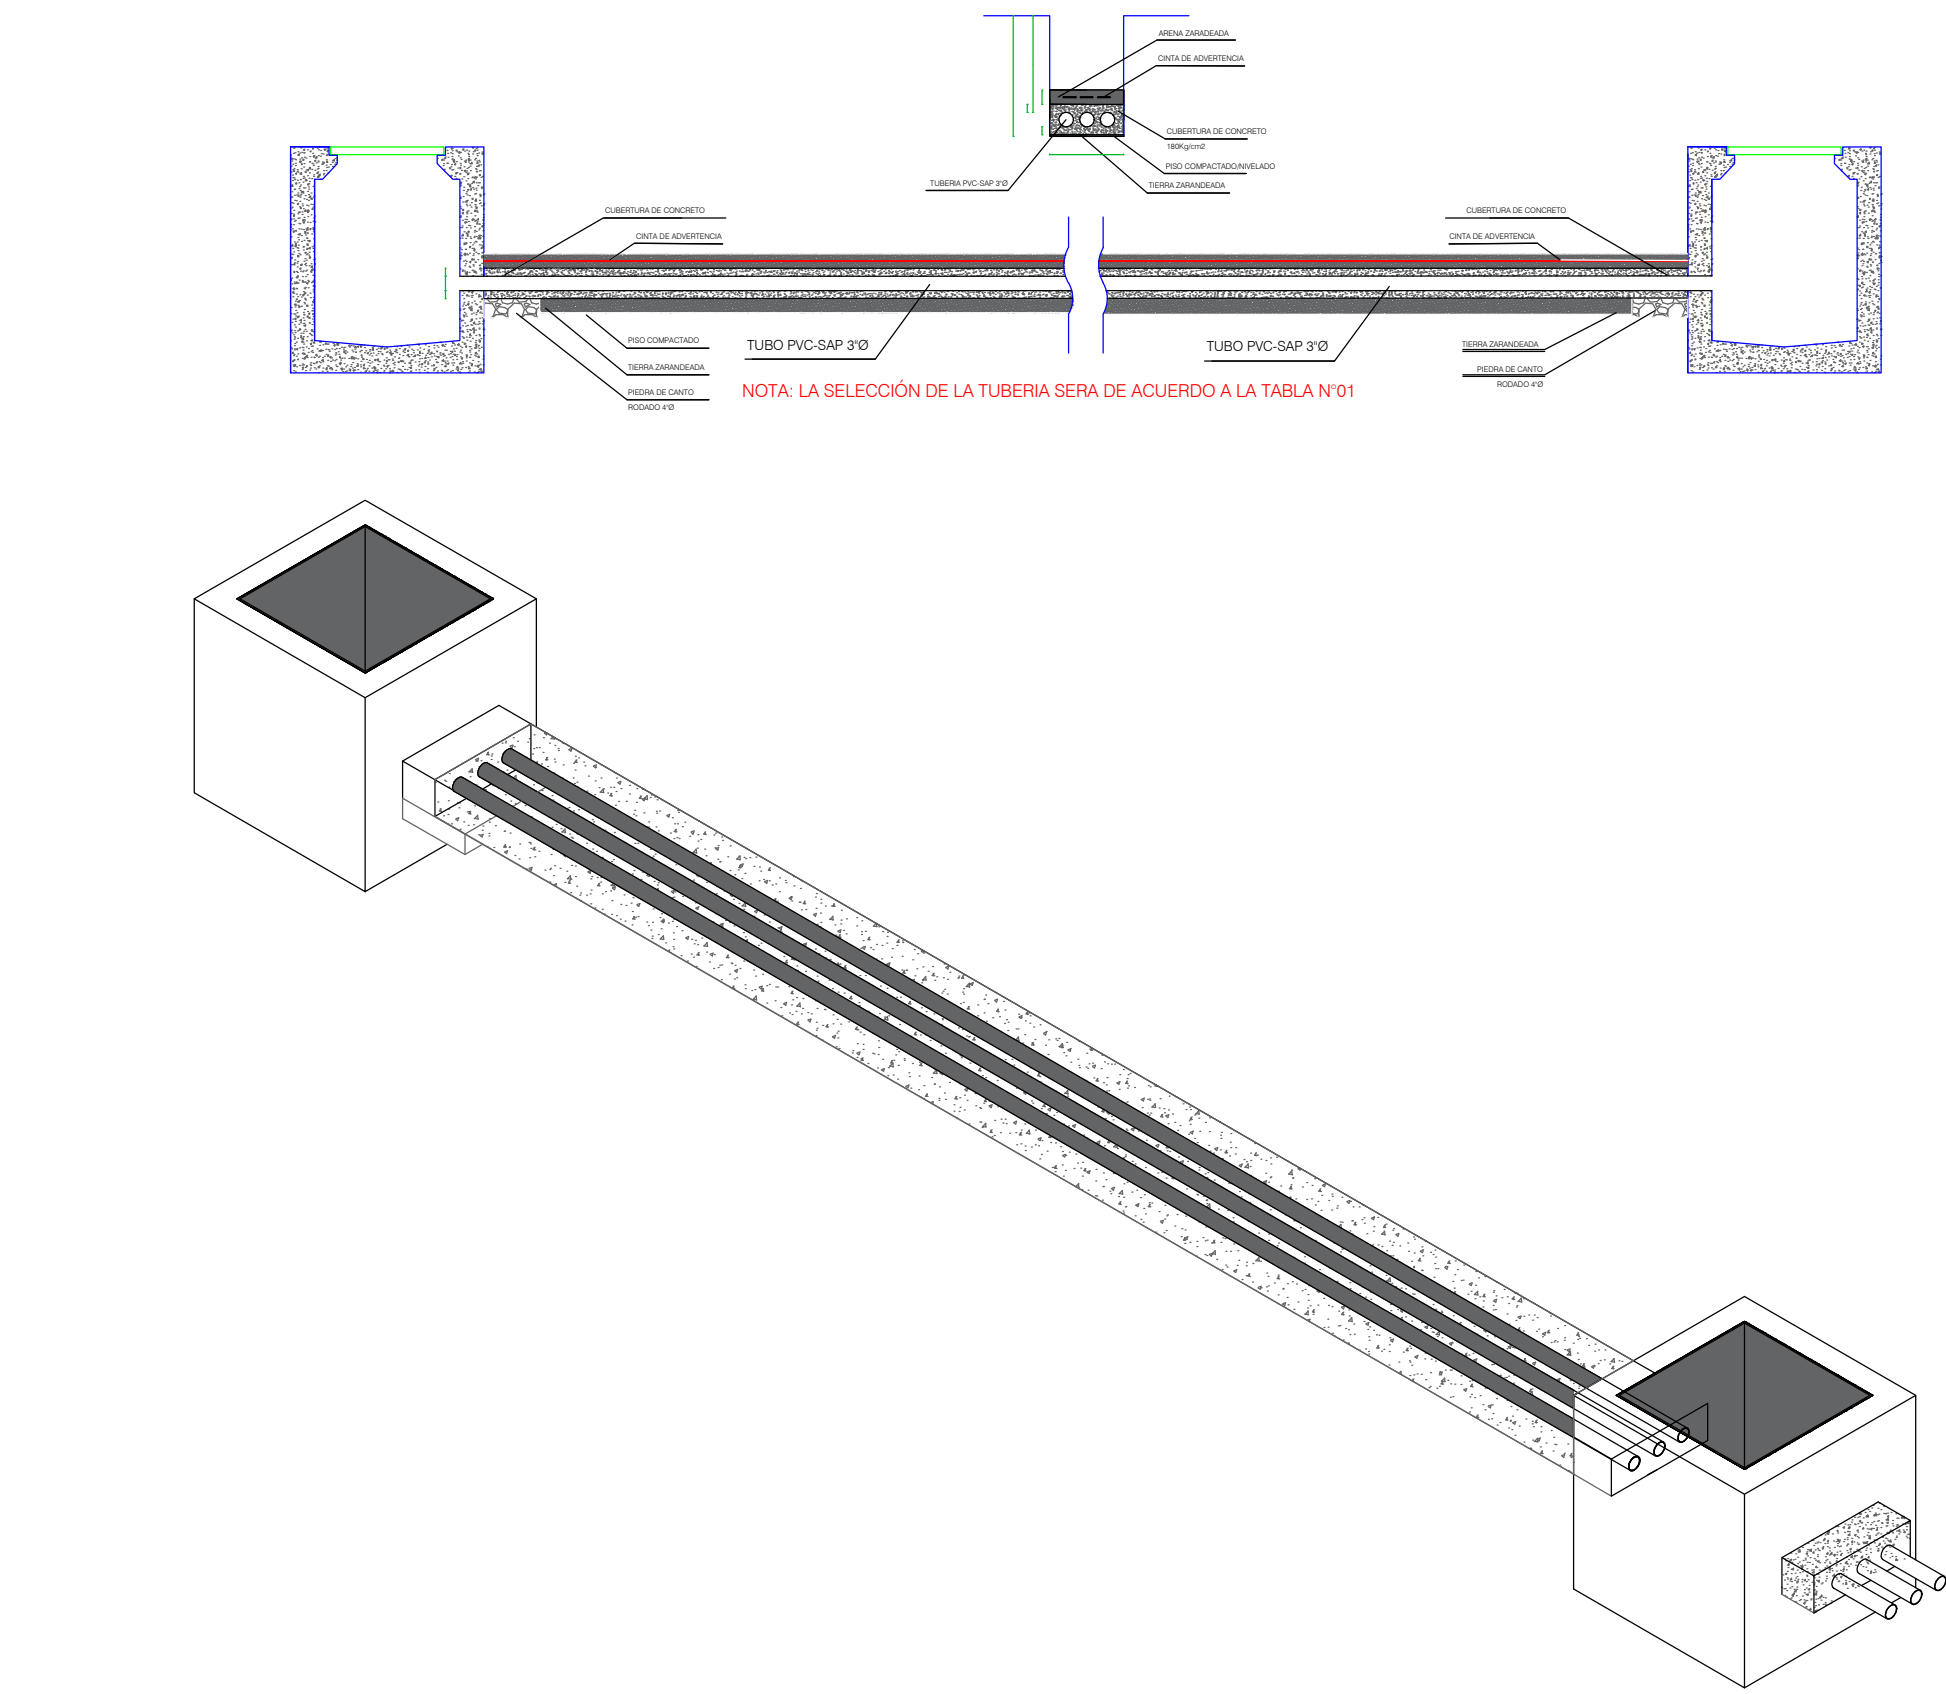

RECTOR:
DR. PAULINO MACHACA ARI
VICERECTOR ACADEMICO:
DR. MARIO S. CUENTAS ALVARADO
VICERECTOR DE INVESTIGACION:
DR. ARIEL VELAZCO CARDENAS

U.E.I
UNIDAD EJECUTORA
DE INVERSIONES

SUB-UNIDAD
DE ESTUDIOS

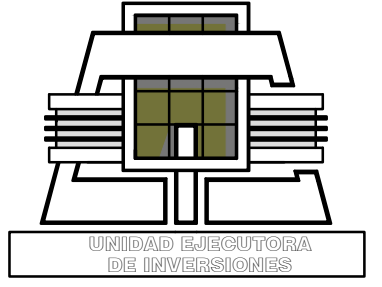

JEFE UNIDAD EJECUTIVA DE INVERSIONES:
ING. WILBER F. CAYRO ROJAS
JEFE SUB-UNIDAD DE ESTUDIOS:
ING. ANDRES A. QUIZA AÑAZCO

DIRECCION:
INSTALACIONES
ELECTRICAS

PLANO:
PRIMER NIVEL

PROYECTO:
**"MEJORAMIENTO DE LA
GESTIÓN INSTITUCIONAL EN
EDUCACIÓN UNIVERSITARIA
DE LOS SERVICIOS
ADMINISTRATIVOS DE LA
UNIVERSIDAD NACIONAL DEL
ALTIPLANO, DISTRITO DE
PUNO -PROVINCIA DE PUNO
- DEPARTAMENTO DE PUNO"**

CONTRATO:
**"ADECUADA Y SUFICIENTE
INFRAESTRUCTURA PARA
LABOR ADMINISTRATIVA
EN LA UNIVERSIDAD"**

DISEÑO DEL PROYECTO: INGENIEROS TÉCNICOS
ING. ANTONIO NETAU ARISTA MAQUERA

UBICACION:
BARRIO BELLAVISTA
AV. EL SOL N° 329

SECCION:
DPTO. PUNO
PROV. PUNO
DISTR. PUNO

FECHA:
SUB UNIDAD DE
ESTUDIOS
FECHA:
FEBRERO 2023
FECHA:
INDICADA

IE-DT1