


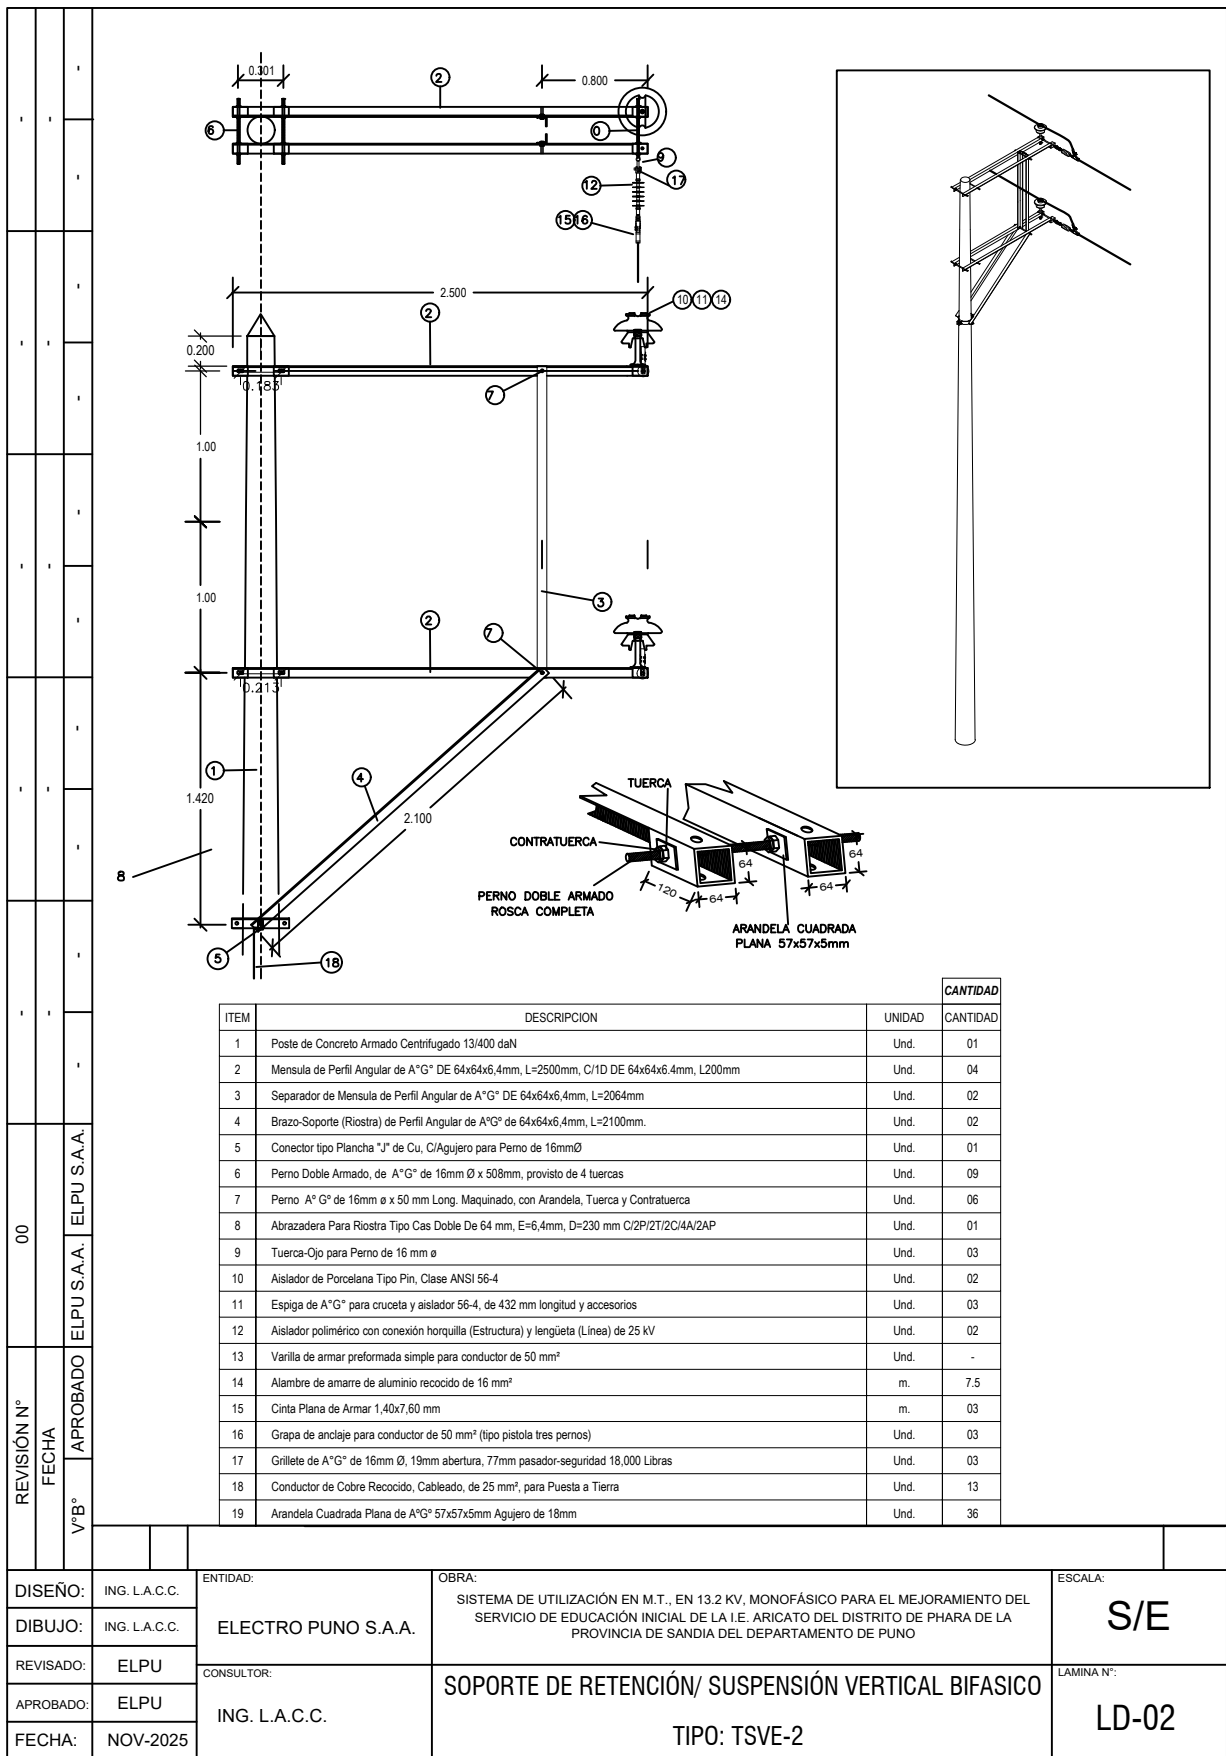

			CANTIDAD
ITEM	DESCRIPCION	UNIDAD	CANTIDAD
1	Poste de Concreto Armado Centrifugado 13/400 daN	Und.	01
2	Mensula de Perfil Angular de A*G* DE 64x64x6,4mm, L=2500mm, C/1D DE 64x64x6,4mm, L200mm	Und.	04
3	Separador de Mensula de Perfil Angular de A*G* DE 64x64x6,4mm, L=2064mm	Und.	02
4	Brazo-Soporte (Riostra) de Perfil Angular de A*G* de 64x64x6,4mm, L=2100mm.	Und.	02
5	Conector tipo Plancha "J" de Cu, C/Agujero para Perno de 16mmØ	Und.	01
6	Perno Doble Armado, de A*G* de 16mm Ø x 508mm, provisto de 4 tuercas	Und.	09
7	Perno A* G* de 16mm ø x 50 mm Long. Maquinado, con Arandela, Tuerca y Contratuerca	Und.	06
8	Abrazadera Para Riostra Tipo Cas Doble De 64 mm, E=6,4mm, D=230 mm C/2P/2T/2C/4A/2AP	Und.	01
9	Tuerca-Ojo para Perno de 16 mm ø	Und.	03
10	Aislador de Porcelana Tipo Pin, Clase ANSI 56-4	Und.	02
11	Espiga de A*G* para cruceta y aislador 56-4, de 432 mm longitud y accesorios	Und.	03
12	Aislador polimérico con conexión horquilla (Estructura) y lengüeta (Linea) de 25 kV	Und.	02
13	Varilla de armar preformada simple para conductor de 50 mm²	Und.	-
14	Alambre de amarre de aluminio recocido de 16 mm²	m.	7.5
15	Cinta Plana de Armar 1,40x7,60 mm	m.	03
16	Grapa de anclaje para conductor de 50 mm² (tipo pistola tres pernos)	Und.	03
17	Grillete de A*G* de 16mm Ø, 19mm abertura, 77mm pasador-seguridad 18,000 Libras	Und.	03
18	Conductor de Cobre Recocido, Cableado, de 25 mm², para Puesta a Tierra	Und.	13
19	Arandela Cuadrada Plana de A*G* 57x57x5mm Agujero de 18mm	Und.	36