PROYECTO DE INGENIERÍA DE DETALLE — LÍNEA PRIMARIA 22.9 kV CAPACHICA A CHIFRÓN

DETALLES CONSTRUCTIVOS DE ARMADOS NORMALIZADOS DGE PS-1 (SUSPENSIÓN) Y PA-1 (ÁNGULO)

ARMADO NORMALIZADO DGE PS-1: SUSPENSIÓN 22.9 kV

Estructuras E-02, E-03, E-07 | Poste C.A.C. 12/300 daN (Escala 1:25)

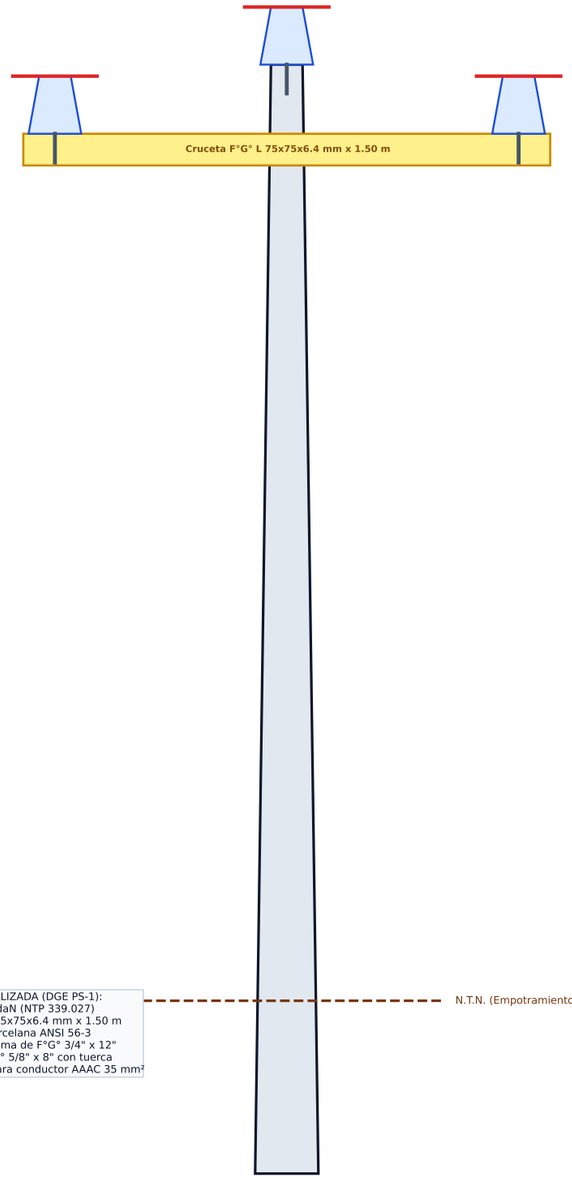

LISTA DE MATERIALES NORMALIZADA (DGE PS-1):
- 01 Poste C.A.C. 12 m / 300 daN (NTP 339.027)
- 01 Cruceta angular F°G° L 75x75x6.4 mm x 1.50 m
- 03 Aisladores tipo Pin de porcelana ANSI 56-3
- 03 Espigas para cruceta y cima de F°G° 3/4" x 12"
- 01 Perno maquinado de F°G° 5/8" x 8" con tuerca
- 03 Ataduras preformadas para conductor AAAC 35 mm²

ARMADO NORMALIZADO DGE PA-1: ÁNGULO 22.9 kV

Estructuras E-05, E-06, E-08 | Poste C.A.C. 12/400 daN + Retenida R-1

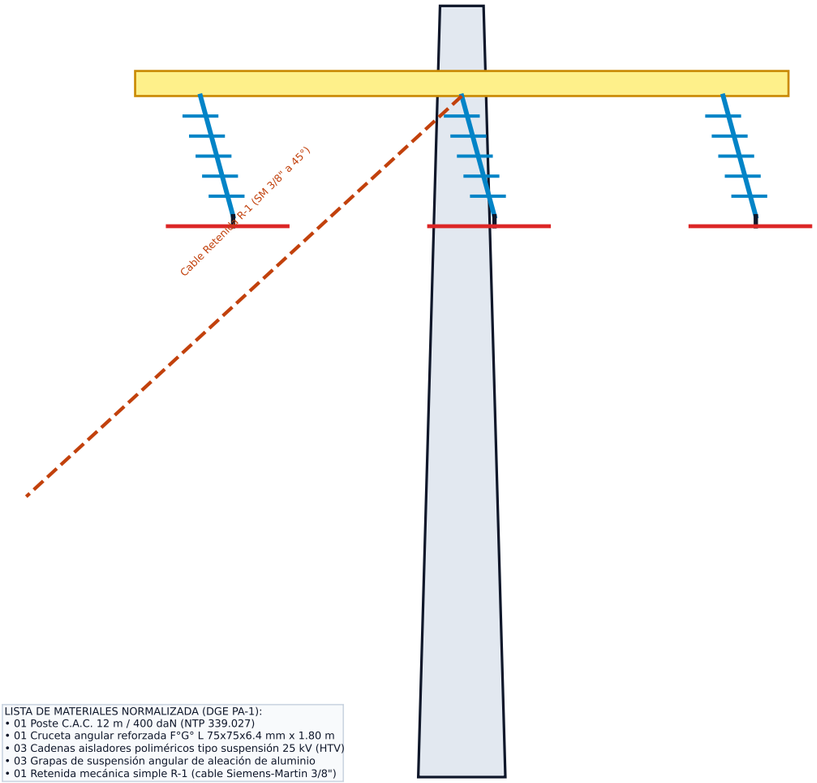

LISTA DE MATERIALES NORMALIZADA (DGE PA-1):
- 01 Poste C.A.C. 12 m / 400 daN (NTP 339.027)
- 01 Cruceta angular reforzada F°G° L 75x75x6.4 mm x 1.80 m
- 03 Cadenas aisladores poliméricos tipo suspensión 25 kV (HTV)
- 03 Grapas de suspensión angular de aleación de aluminio
- 01 Retenida mecánica simple R-1 (cable Siemens-Martin 3/8")

UNIVERSIDAD NACIONAL DEL ALTIPLANO — PUNO

FACULTAD DE INGENIERÍA MECÁNICA ELÉCTRICA, ELECTRÓNICA Y SISTEMAS

ESCUELA PROFESIONAL DE INGENIERÍA MECÁNICA ELÉCTRICA

PROYECTO: LÍNEA PRIMARIA 22.9 kV Y SUBESTACIÓN SAB-1 100 kVA

SECTOR CHIFRÓN — DISTRITO DE CAPACHICA — PUNO

PLANO: DETALLES DE ARMADOS NORMALIZADOS DGE

PS-1 (SUSPENSIÓN) Y PA-1 (ÁNGULO) 22.9 kV

PROYECTISTA: Br. Renzo Gabriel Mamani Galindo (Cód. 228447)
DOCENTES: Ing. Leonidas Vilca Callata / Ing. Marcos José Villanueva Cornejo

FECHA:	ESCALA:	LÁMINA:
Octubre 2026	1 : 25	**D-01**