PROYECTO DE INGENIERÍA DE DETALLE — LÍNEA PRIMARIA 22.9 kV CAPACHICA A CHIFRÓN

DETALLES DE ARMADO DGE PR-1 (RETENCIÓN) Y SUBESTACIÓN AÉREA BIPOSTE SAB-1 100 kVA

SUBESTACIÓN AÉREA BIPOSTE SAB-1 100 kVA (22.9 kV)

Estructura E-04 | 2x Postes C.A.C. 13/400 | Intereje = 2.00 m (Escala 1:30)

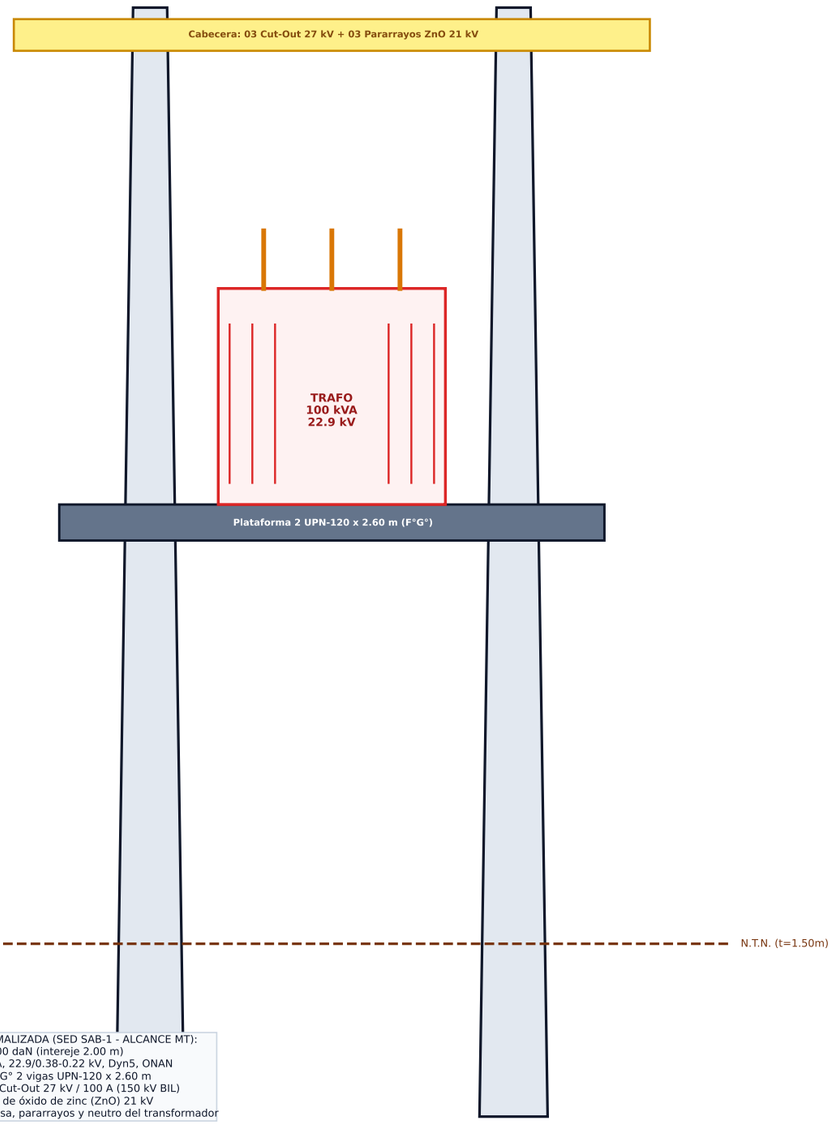

LISTA DE MATERIALES NORMALIZADA (SED SAB-1 - ALCANCE MT):
- 02 Postes C.A.C. 13 m / 400 daN (intereje 2.00 m)
- 01 Transformador 100 kVA, 22.9/0.38-0.22 kV, Dyn5, ONAN
- 01 Plataforma metálica F°G° 2 vigas UPN-120 x 2.60 m
- 03 Cortacircuitos fusibles Cut-Out 27 kV / 100 A (150 kV BIL)
- 03 Pararrayos poliméricos de óxido de zinc (ZnO) 21 kV
- 01 Sistema PAT-3 para masa, pararrayos y neutro del transformador

ARMADO NORMALIZADO DGE PR-1: RETENCIÓN 22.9 kV

Estructuras E-01 (Derivación) y E-09 (Terminal) | Poste C.A.C. 12/400 daN

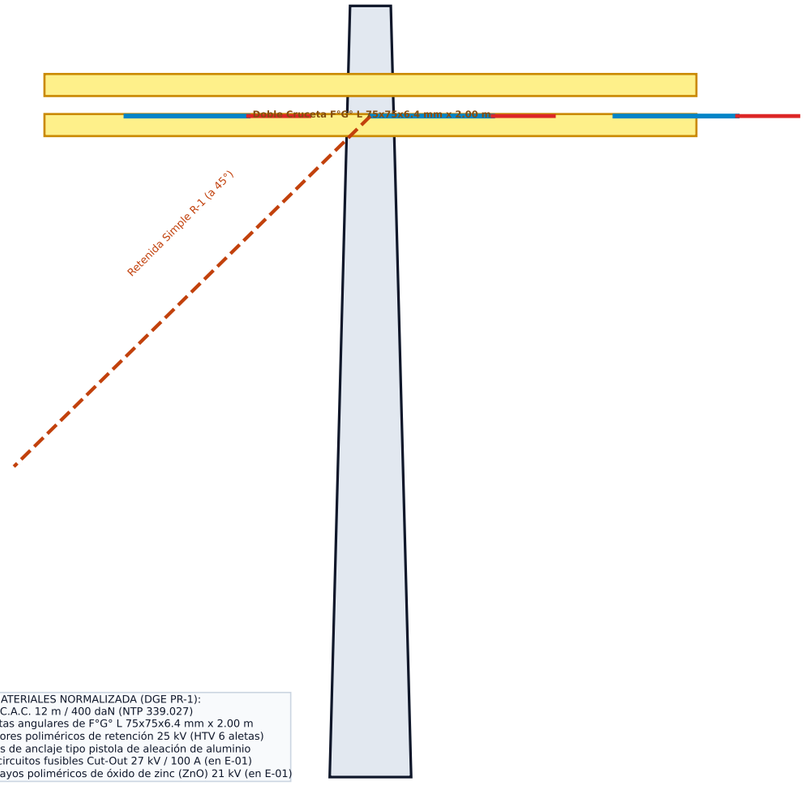

LISTA DE MATERIALES NORMALIZADA (DGE PR-1):
- 01 Poste C.A.C. 12 m / 400 daN (NTP 339.027)
- 02 Crucetas angulares de F°G° L 75x75x6.4 mm x 2.00 m
- 03 Aisladores poliméricos de retención 25 kV (HTV 6 aletas)
- 03 Grapas de anclaje tipo pistola de aleación de aluminio
- 03 Cortacircuitos fusibles Cut-Out 27 kV / 100 A (en E-01)
- 03 Pararrayos poliméricos de óxido de zinc (ZnO) 21 kV (en E-01)

UNIVERSIDAD NACIONAL DEL ALTIPLANO — PUNO

FACULTAD DE INGENIERÍA MECÁNICA ELÉCTRICA, ELECTRÓNICA Y SISTEMAS

ESCUELA PROFESIONAL DE INGENIERÍA MECÁNICA ELÉCTRICA

PROYECTO: LÍNEA PRIMARIA 22.9 kV Y SUBESTACIÓN SAB-1 100 kVA

SECTOR CHIFRÓN — DISTRITO DE CAPACHICA — PUNO

PLANO: DETALLES DE ARMADO NORMALIZADO DGE PR-1

Y SUBESTACIÓN AÉREA BIPOSTE SAB-1 100 kVA

PROYECTISTA: Br. Renzo Gabriel Mamani Galindo (Cód. 228447)
DOCENTES: Ing. Leonidas Vilca Callata / Ing. Marcos José Villanueva Cornejo

FECHA:	ESCALA:	LÁMINA:
Octubre 2026	1 : 30	**D-02**