PROYECTO DE INGENIERÍA DE DETALLE — LÍNEA PRIMARIA 22.9 kV CAPACHICA A CHIFRÓN

PLANO DE TRAZA, REPLANTEO TOPOGRÁFICO, SERVIDUMBRE Y ESTRUCTURAS EN MEDIA TENSIÓN

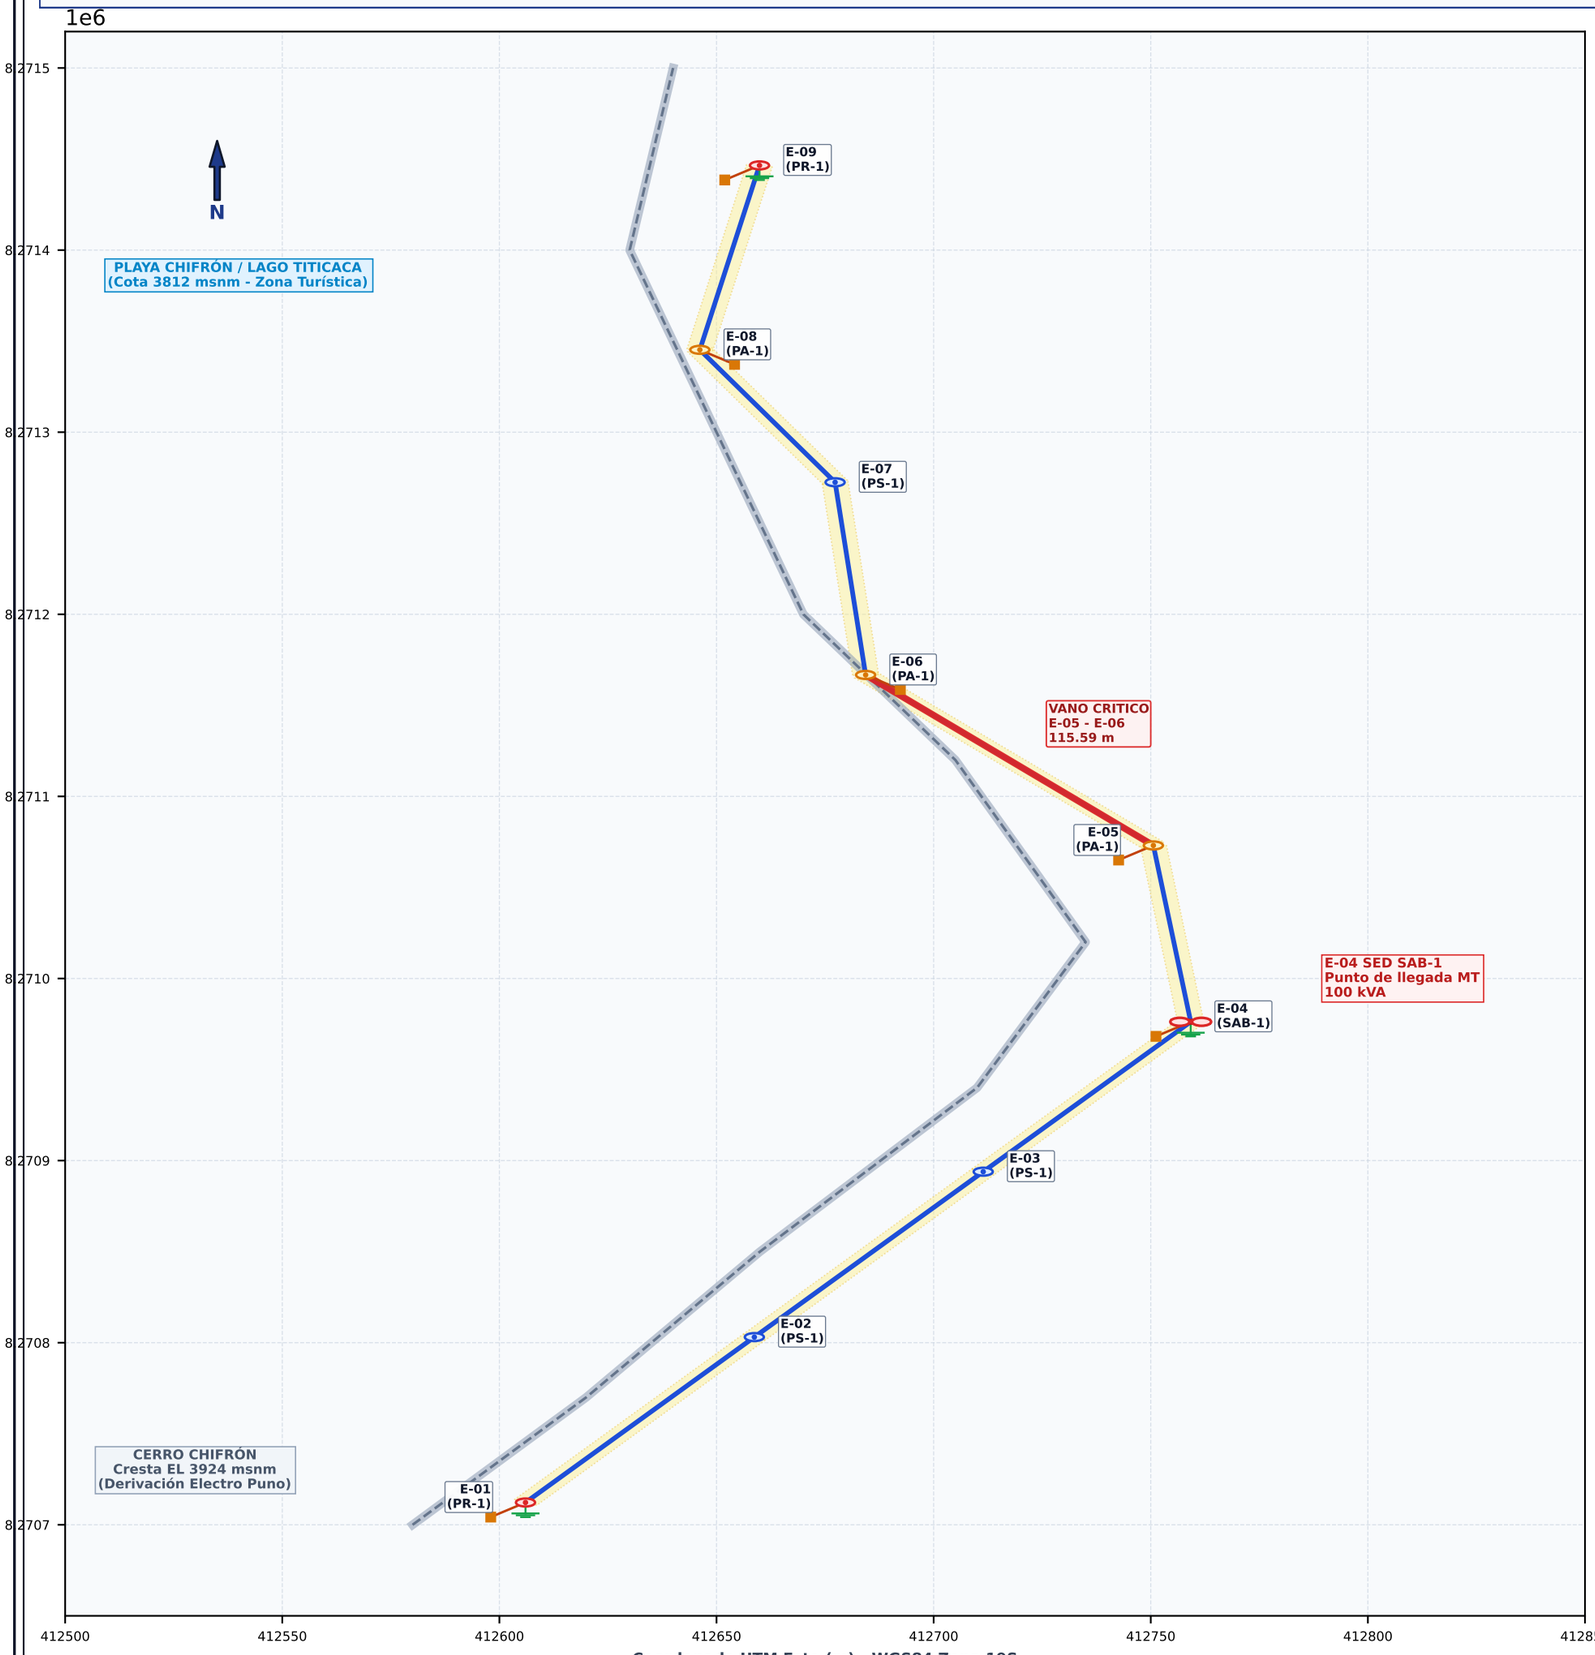

CUADRO TÉCNICO DE ESTRUCTURAS LP 22.9 kV

ID	Prog(m)	Cota	Poste	Arm	Ang(°)	Retenida	PAT
E-01	0.0	3924.2	12/400	PR-1	0.0	Inclinada	PAT-3
E-02	105.0	3895.0	12/300	PS-1	0.0	-	-
E-03	210.0	3865.0	12/300	PS-1	0.0	-	-
E-04	305.2	3839.6	2x 13/400 (Biposte)	SAB-1	-35.2	Contravientox2	PAT-3
E-05	402.4	3817.0	12/400	PA-1	-36.1	Biselar	-
E-06	518.0	3827.3	12/400	PA-1	+31.4	Biselar	-
E-07	628.5	3824.6	12/300	PS-1	-6.0	-	-
E-08	708.3	3824.6	12/400	PA-1	+33.0	Biselar	-
E-09	816.6	3824.6	12/400	PR-1	0.0	Terminal	PAT-3

NOTAS TÉCNICAS Y LEYENDA NORMALIZADA DGE

1. Tensión de Servicio: 22.9 kV trifásico, 3 hilos (3Ø), 60 Hz.
2. Conductor de Fase: AAAC 35 mm² (sección real 34.36 mm², 7 hilos).
3. Faja de Servidumbre Legal: 6.00 m (3.00 m a cada lado del eje de trazo).
4. CNE Suministro Regla 219 y R.D. 018-2003-EM/DGE: Gálibo mínimo 6.50 m.
5. Aislamiento Polimérico HTV 25 kV, línea de fuga mínima 810 mm.
6. Cimentaciones en concreto ciclópeo f'c=140 kg/cm² + 30% PM (Sulzberger).

UNIVERSIDAD NACIONAL DEL ALTIPLANO— PUNO

FACULTAD DE INGENIERÍA MECÁNICA ELÉCTRICA, ELECTRÓNICA Y SISTEMAS

ESCUELA PROFESIONAL DE INGENIERÍA MECÁNICA ELÉCTRICA

PROYECTO: LÍNEA PRIMARIA 22.9 kV Y SUBESTACIÓN SAB-1 100 kVA

SECTOR CHIFRÓN — DISTRITO DE CAPACHICA — PUNO

PLANO: PLANO DE TRAZA, PLANTA GENERAL Y SERVIDUMBRE DE LÍNEA PRIMARIA 22.9 kV

PROYECTISTA: Br. Renzo Gabriel Mamani Galindo (Cód. 228447)

DOCENTES: Ing. Leonidas Vilca Callata / Ing. Marcos José Villanueva Cornejo

FECHA:	ESCALA:	LÁMINA:
Octubre 2026	1 : 2000	LP-01