PROYECTO DE INGENIERÍA DE DETALLE — LÍNEA PRIMARIA 22.9 kV CAPACHICA A CHIFRÓN

PLANO DE PERFIL LONGITUDINAL TOPOGRÁFICO, SPOTTING Y CATENARIAS (CNE SUMINISTRO)

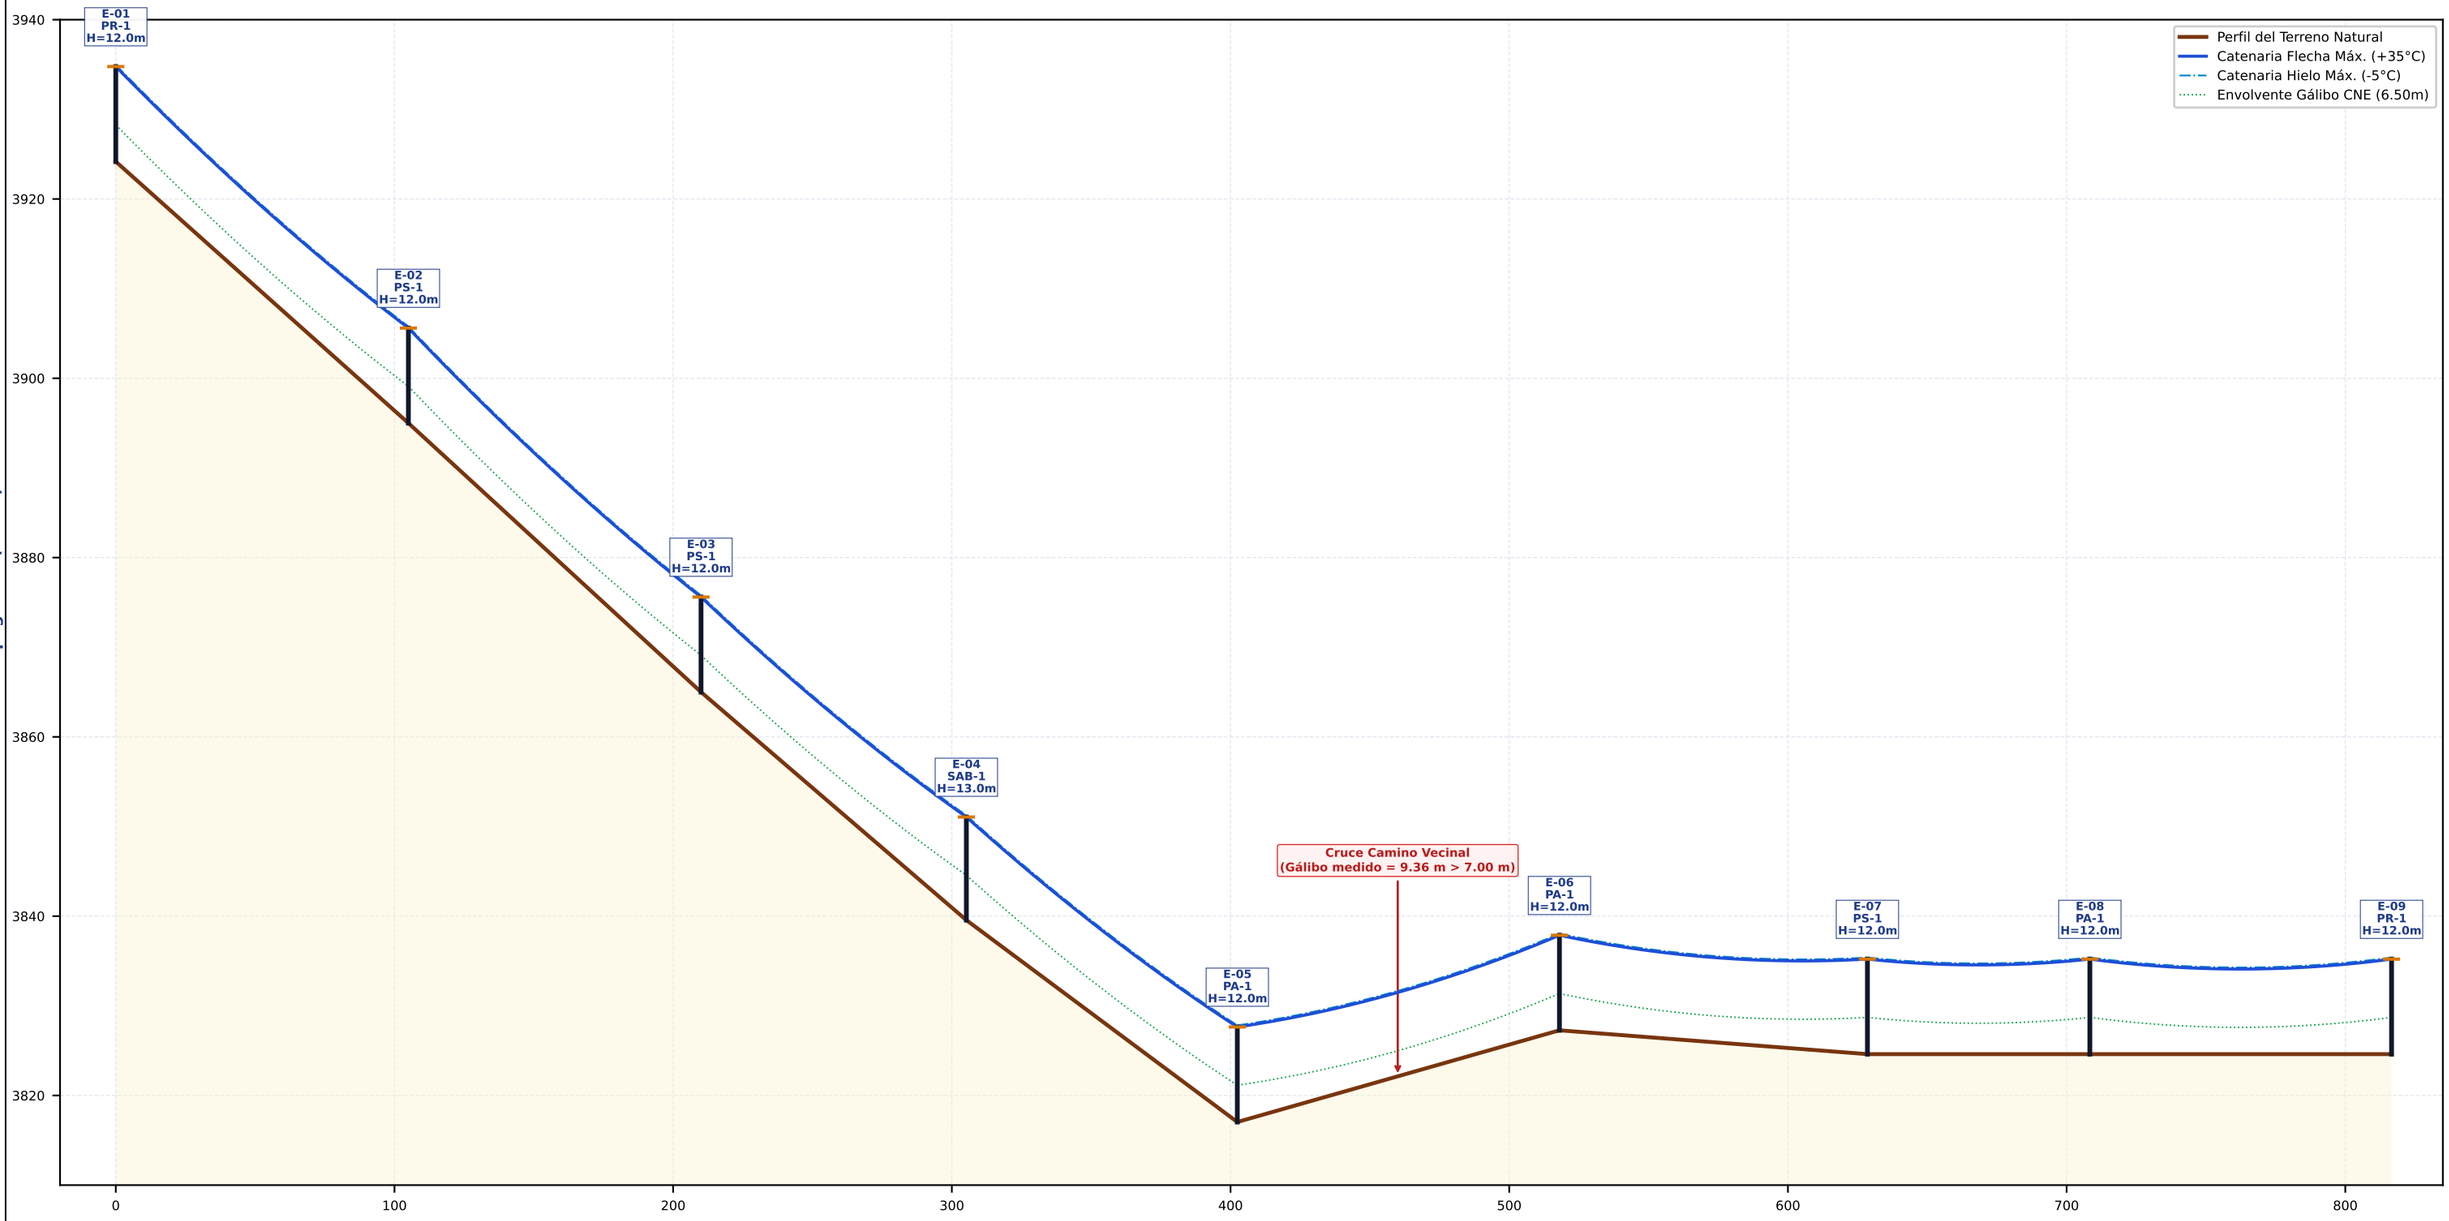

TABLA DE SPOTTING, VANOS Y VERIFICACIÓN DE GÁLIBOS (CNE REGLA 232)

PROGRESIVA (m):	0.0	105.0	210.0	305.2	402.4	518.0	628.5	708.3	816.6
COTA TERRENO (msnm):	3924.2	3895.0	3865.0	3839.6	3817.0	3827.3	3824.6	3824.6	3824.6
COTA CIMA (msnm):	3934.8	3905.6	3875.6	3851.1	3827.6	3837.9	3835.2	3835.2	3835.2
VANO HORIZ. (m):	-	105.0	105.0	95.2	97.2	115.6	110.5	79.8	108.3
FLECHA MÁX. (m):	-	1.05	1.05	0.89	0.92	1.24	1.15	0.65	1.11
GÁLIBO NORM. (m):	-	9.55	9.55	10.16	10.13	9.36	9.45	9.95	9.49
ESTRUCTURA C.A.C.:	12/400	12/300	12/300	2x 13/400 (Biposte)	12/400	12/400	12/300	12/400	12/400
ARMADO DGE:	PR-1	PS-1	PS-1	SAB-1	PA-1	PA-1	PS-1	PA-1	PR-1
CIMENTACIÓN:	Sulzb. 0.8m	Sulzb. 0.8m	Sulzb. 0.8m	Sulzb. 0.9m	Sulzb. 0.8m	Sulzb. 0.8m	Sulzb. 0.8m	Sulzb. 0.8m	Sulzb. 0.8m

UNIVERSIDAD NACIONAL DEL ALTIPLANO— PUNO

FACULTAD DE INGENIERÍA MECÁNICA ELÉCTRICA, ELECTRÓNICA Y SISTEMAS

ESCUELA PROFESIONAL DE INGENIERÍA MECÁNICA ELÉCTRICA

PROYECTO: LÍNEA PRIMARIA 22.9 kV Y SUBESTACIÓN SAB-1 100 kVA

SECTOR CHIFRÓN — DISTRITO DE CAPACHICA — PUNO

PLANO: PERFIL LONGITUDINAL TOPOGRÁFICO, SPOTTING Y CATENARIAS DE LÍNEA PRIMARIA 22.9 kV

PROYECTISTA: Br. Renzo Gabriel Mamani Galindo (Cód. 228447)

DOCENTES: Ing. Leonidas Vilca Callata / Ing. Marcos José Villanueva Cornejo

FECHA:	**ESCALA:**	**LÁMINA:**
Octubre 2026	H: 1/2000, V: 1/500	**PL-01**