
LÍNEA PRIMARIA LIMBANI – HUANCASAYANI

LP-01

LP-R02 | 18/10/2026

Planta general del corredor candidato

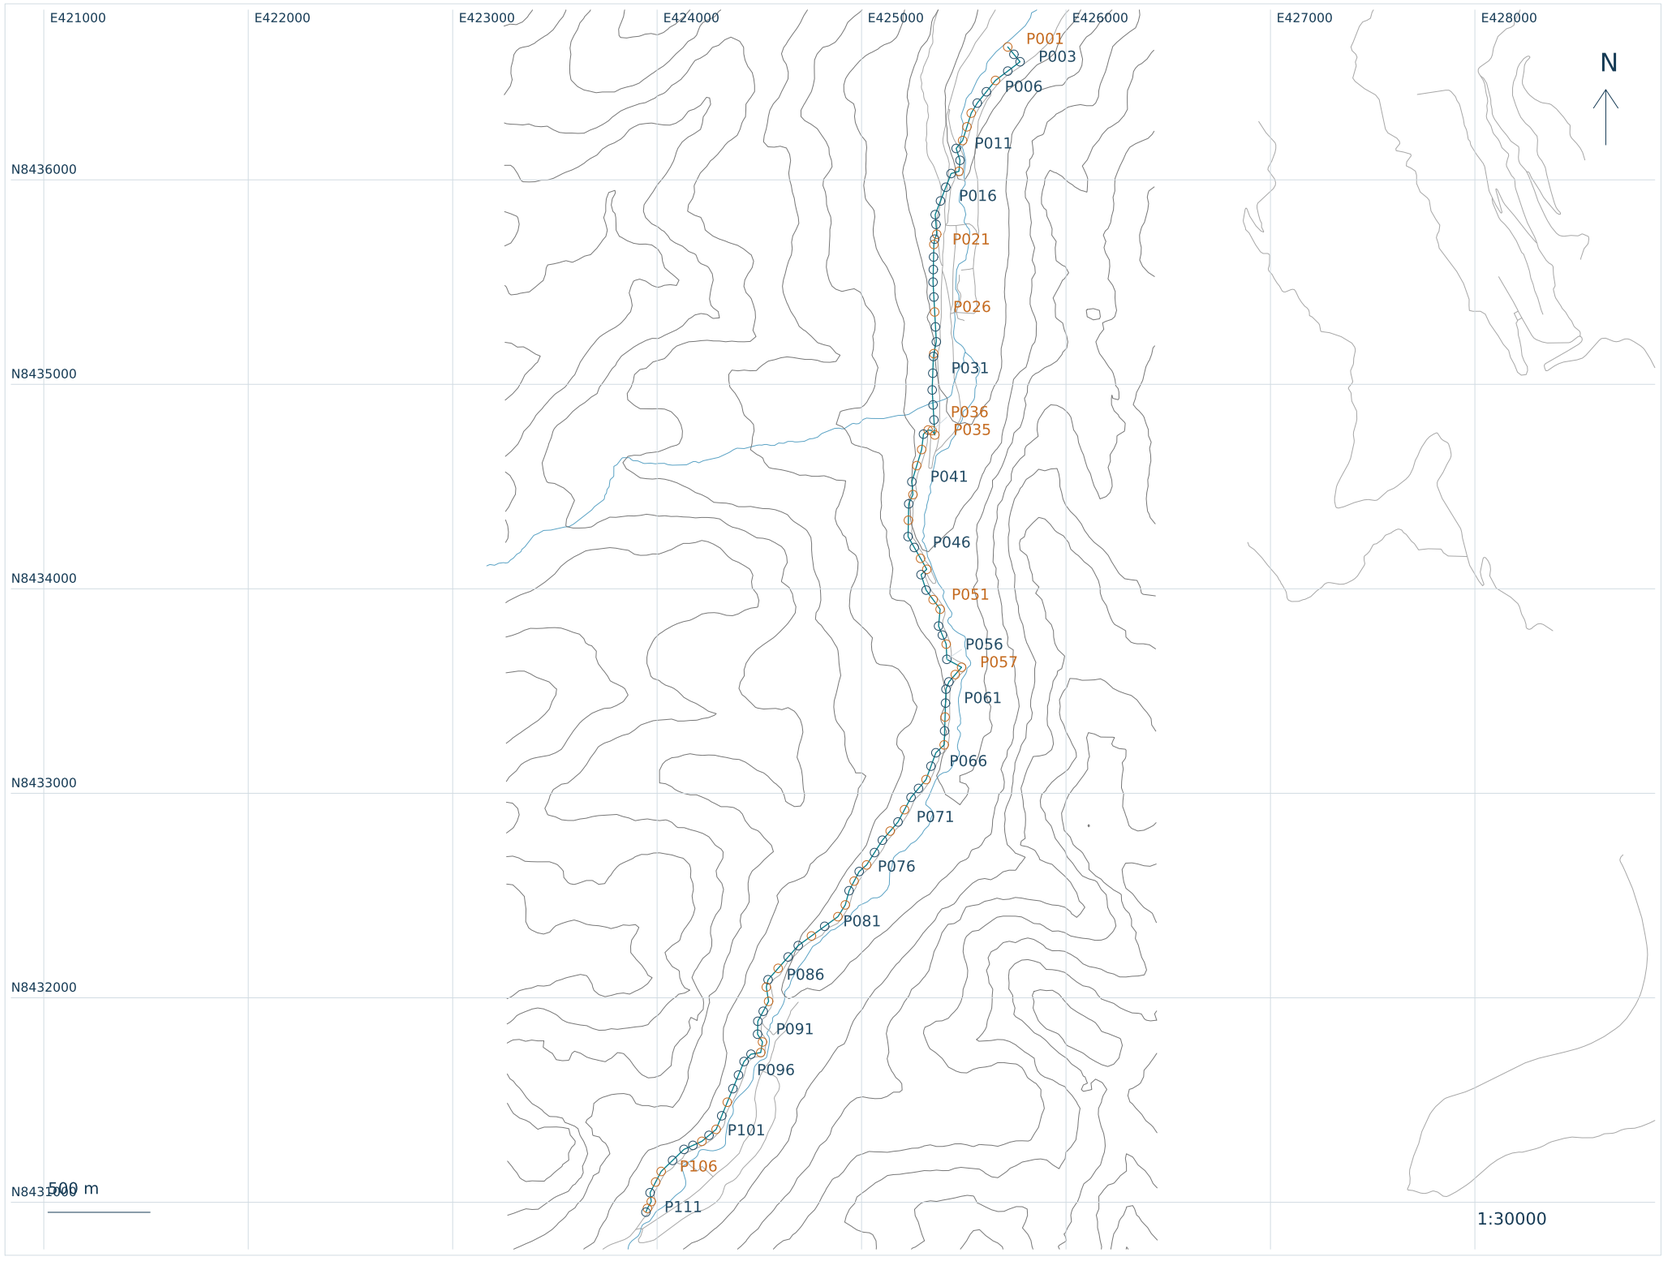

Un solo eje representa la terna: 3 x AAAC 50 mm2. Longitud horizontal 6696.37 m.

111 apoyos y 110 vanos. Las posiciones se conservan para revisar la propuesta R01.

Círculo naranja: apoyo con carga ascendente en algún estado. No indica aprobación o rechazo de la cimentación.

Cotas: DEM de gabinete heredado, resolución aproximada30 m. No certifica gálibos, cauces ni predios.

SE-LIM y SE-HUA: posiciones propuestas. La tensión real queda pendiente de placas y decisión10/22.9 kV.

Origen de cartografía: OSM, catastro aportado y DEM deR01. Fuente y hashes en 08-recursos.

INSTALACIONES ELÉCTRICAS II | Aquiles Taylor Ramos Yapo | 227368

REVISIÓN ACADÉMICA · CAMPO, EQUIPOS Y PREDIOS PENDIENTES

UTM WGS84 / 19S · EPSG:32719 | Modelo CAD en metros

Escala al imprimir A3: según barra