
LÍNEA PRIMARIA LIMBANI – HUANCASAYANI


LP-05

LP-R02 | 18/10/2026

Planta y perfil de gabinete: P001 – P017

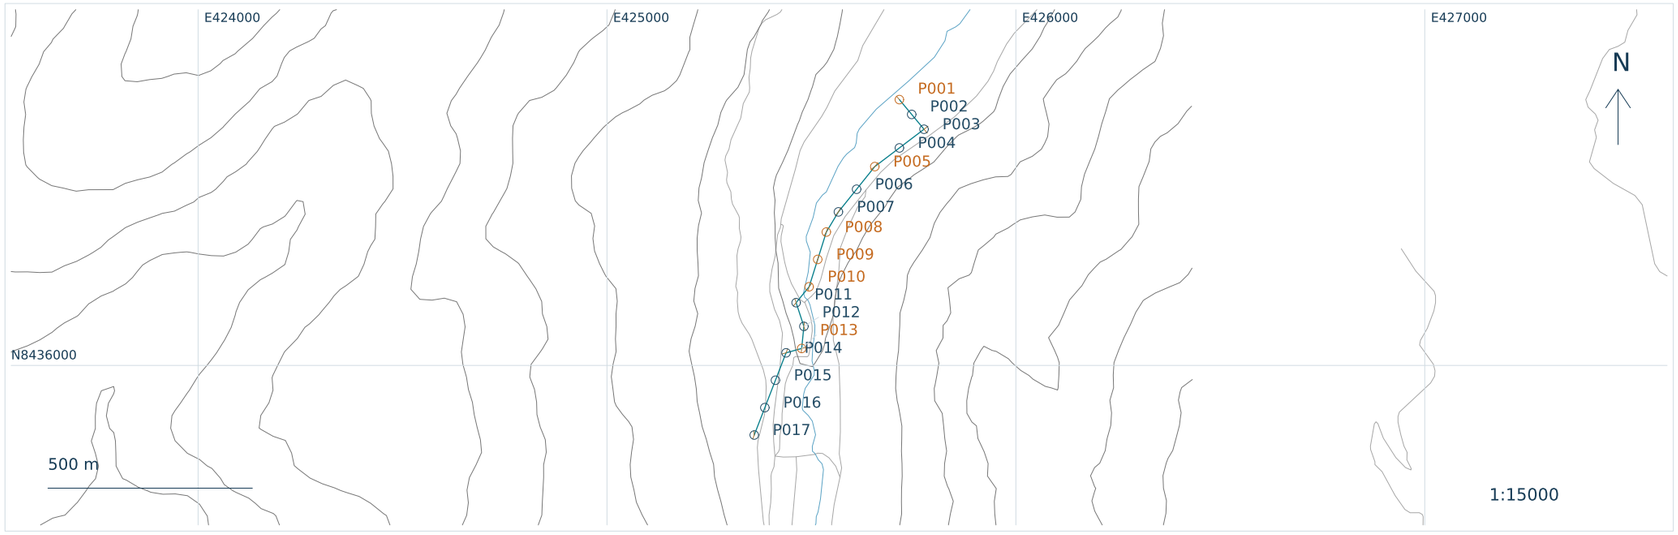

H 1:5000 | V 1:2000 | CALOR_FINAL75C + fluencia345 microstrain

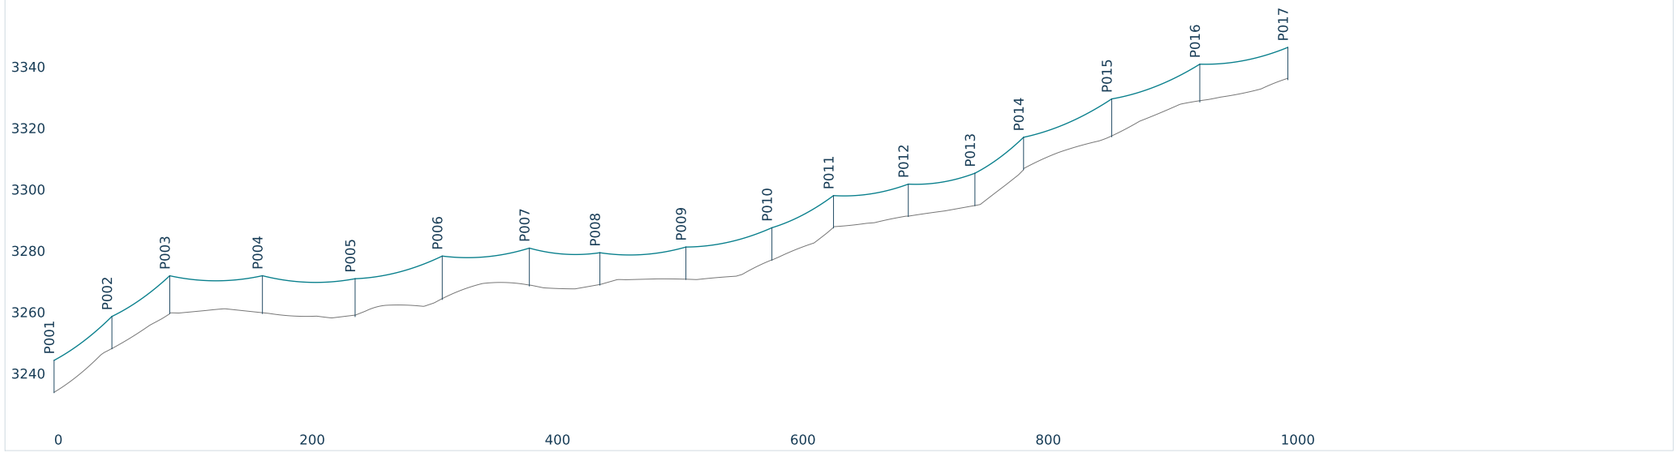

Progresiva 0.0–1005.8 m. Un solo eje representa tres conductores.

Naranja: carga ascendente en algún estado. Retenidas dibujadas como posiciones ideales pendientes.

Terreno gris: perfil DEM heredado. Conductor verde: cálculo por vano; no es medición ni gálibo certificado.

Las cotas DEM tienen resolución~30 m. Topografía lateral y de cruces pendiente.

Vanos de esta lámina:

V001: L47.1 m, f1.06 m

V002: L47.1 m, f1.05 m

V003: L75.6 m, f1.65 m

V004: L75.6 m, f1.66 m

V005: L71.0 m, f1.56 m

V006: L71.0 m, f1.54 m

V007: L57.5 m, f1.22 m

V008: L70.1 m, f1.52 m

V009: L70.1 m, f1.53 m

V010: L50.2 m, f1.09 m

V011: L61.0 m, f1.31 m

V012: L54.3 m, f1.15 m

V013: L39.7 m, f0.88 m

V014: L71.8 m, f1.60 m

V015: L71.8 m, f1.60 m

V016: L71.8 m, f1.57 m

INSTALACIONES ELÉCTRICAS II | Aquiles Taylor Ramos Yapo | 227368

REVISIÓN ACADÉMICA · CAMPO, EQUIPOS Y PREDIOS PENDIENTES

UTM WGS84 / 19S · EPSG:32719 | Modelo CAD en metros

Escala al imprimir A3: S/E