
LÍNEA PRIMARIA LIMBANI – HUANCASAYANI


LP-06

LP-R02 | 18/10/2026

Planta y perfil de gabinete: P017 – P033

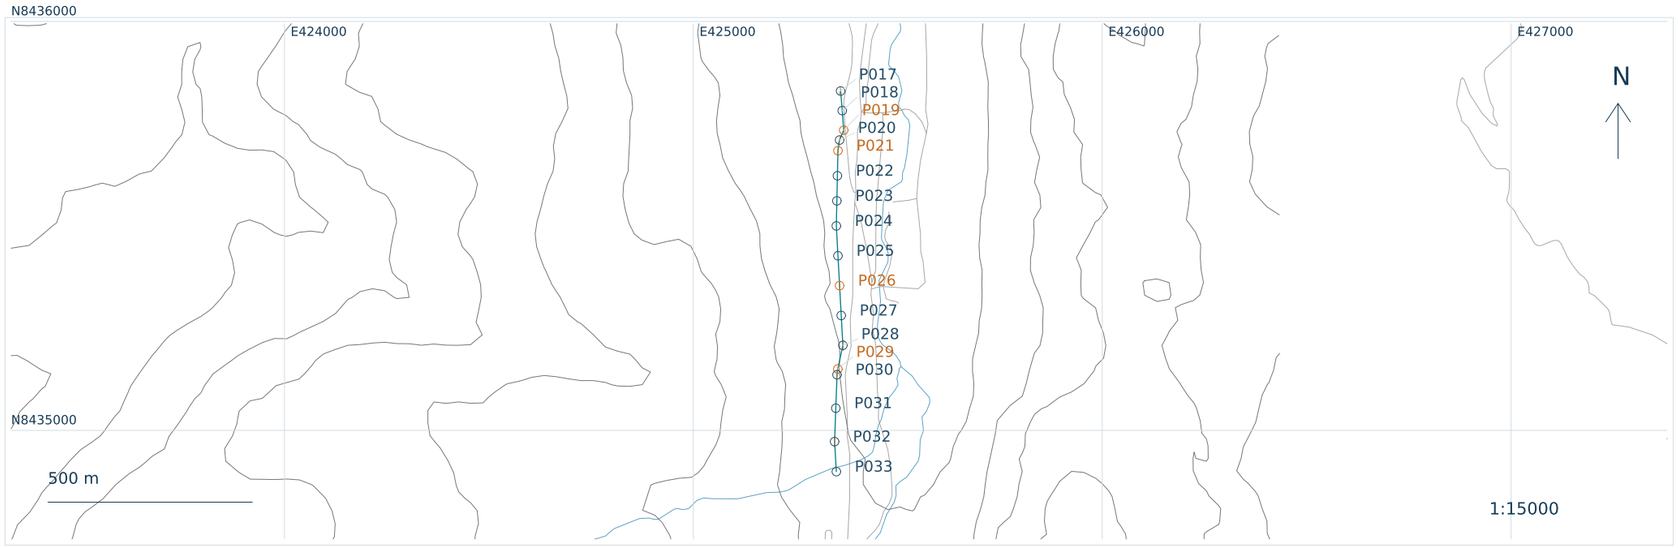

H 1:5000 | V 1:2000 | CALOR_FINAL75C + fluencia345 microstrain

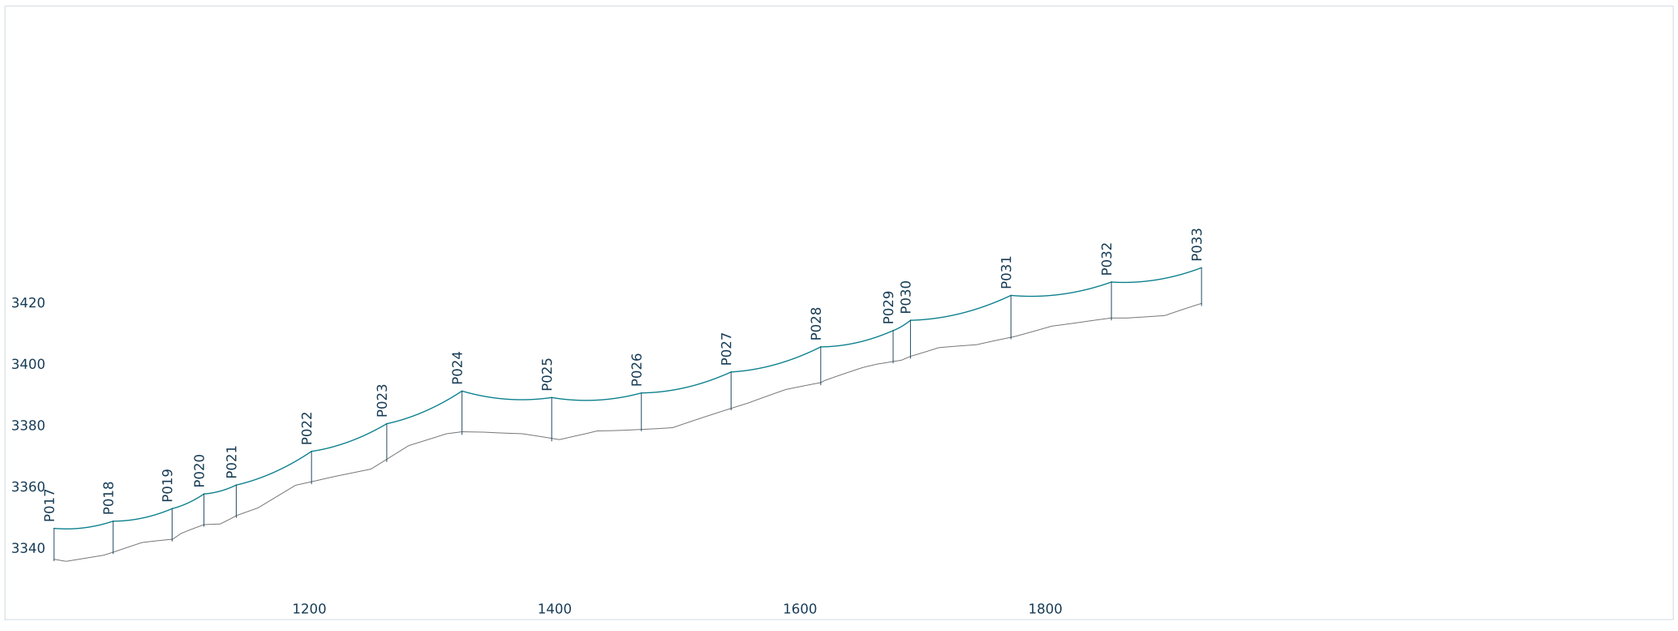

Progresiva 1005.8–1941.3 m. Un solo eje representa tres conductores.

Naranja: carga ascendente en algún estado. Retenidas dibujadas como posiciones ideales pendientes.

Terreno gris: perfil DEM heredado. Conductor verde: cálculo por vano; no es medición ni gálibo certificado.

Las cotas DEM tienen resolución~30 m. Topografía lateral y de cruces pendiente.

Vanos de esta lámina:

V017: L48.2 m, f1.01 m

V018: L48.0 m, f1.01 m

V019: L26.0 m, f0.54 m

V020: L26.3 m, f0.54 m

V021: L61.3 m, f1.35 m

V022: L61.3 m, f1.33 m

V023: L61.3 m, f1.34 m

V024: L73.1 m, f1.60 m

V025: L73.1 m, f1.59 m

V026: L73.1 m, f1.61 m

V027: L73.1 m, f1.61 m

V028: L59.0 m, f1.26 m

V029: L14.1 m, f0.29 m

V030: L81.9 m, f1.83 m

V031: L81.9 m, f1.82 m

V032: L73.5 m, f1.61 m

INSTALACIONES ELÉCTRICAS II | Aquiles Taylor Ramos Yapo | 227368

REVISIÓN ACADÉMICA · CAMPO, EQUIPOS Y PREDIOS PENDIENTES

UTM WGS84 / 19S · EPSG:32719 | Modelo CAD en metros

Escala al imprimir A3: S/E