
LÍNEA PRIMARIA LIMBANI – HUANCASAYANI


LP-08

LP-R02 | 18/10/2026

Planta y perfil de gabinete: P049 – P065

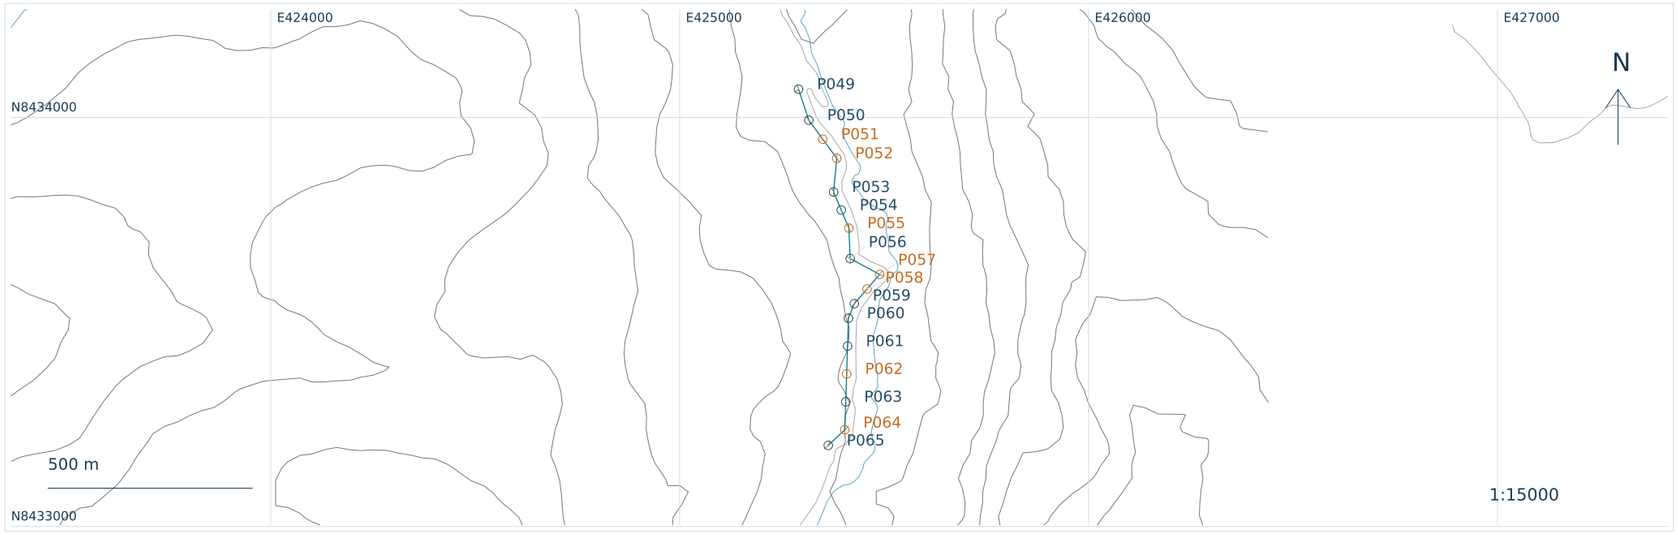

H 1:5000 | V 1:2000 | CALOR_FINAL75C + fluencia345 microstrain

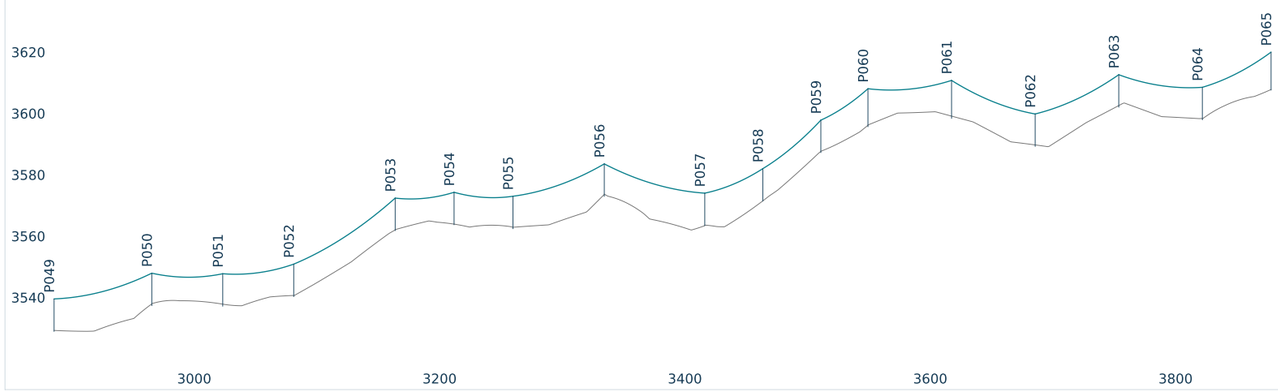

Progresiva 2899.7–3891.8 m. Un solo eje representa tres conductores.

Naranja: carga ascendente en algún estado. Retenidas dibujadas como posiciones ideales pendientes.

Terreno gris: perfil DEM heredado. Conductor verde: cálculo por vano; no es medición ni gálibo certificado.

Las cotas DEM tienen resolución~30 m. Topografía lateral y de cruces pendiente.

Vanos de esta lámina:

V049: L79.7 m, f1.77 m

V050: L57.9 m, f1.23 m

V051: L57.9 m, f1.23 m

V052: L82.7 m, f1.94 m

V053: L48.0 m, f1.00 m

V054: L48.0 m, f1.00 m

V055: L74.5 m, f1.65 m

V056: L81.9 m, f1.83 m

V057: L47.3 m, f1.01 m

V058: L47.3 m, f1.08 m

V059: L38.4 m, f0.84 m

V060: L68.2 m, f1.48 m

V061: L68.2 m, f1.51 m

V062: L68.2 m, f1.52 m

V063: L68.2 m, f1.48 m

V064: L56.0 m, f1.23 m

INSTALACIONES ELÉCTRICAS II | Aquiles Taylor Ramos Yapo | 227368

REVISIÓN ACADÉMICA · CAMPO, EQUIPOS Y PREDIOS PENDIENTES

UTM WGS84 / 19S · EPSG:32719 | Modelo CAD en metros

Escala al imprimir A3: S/E