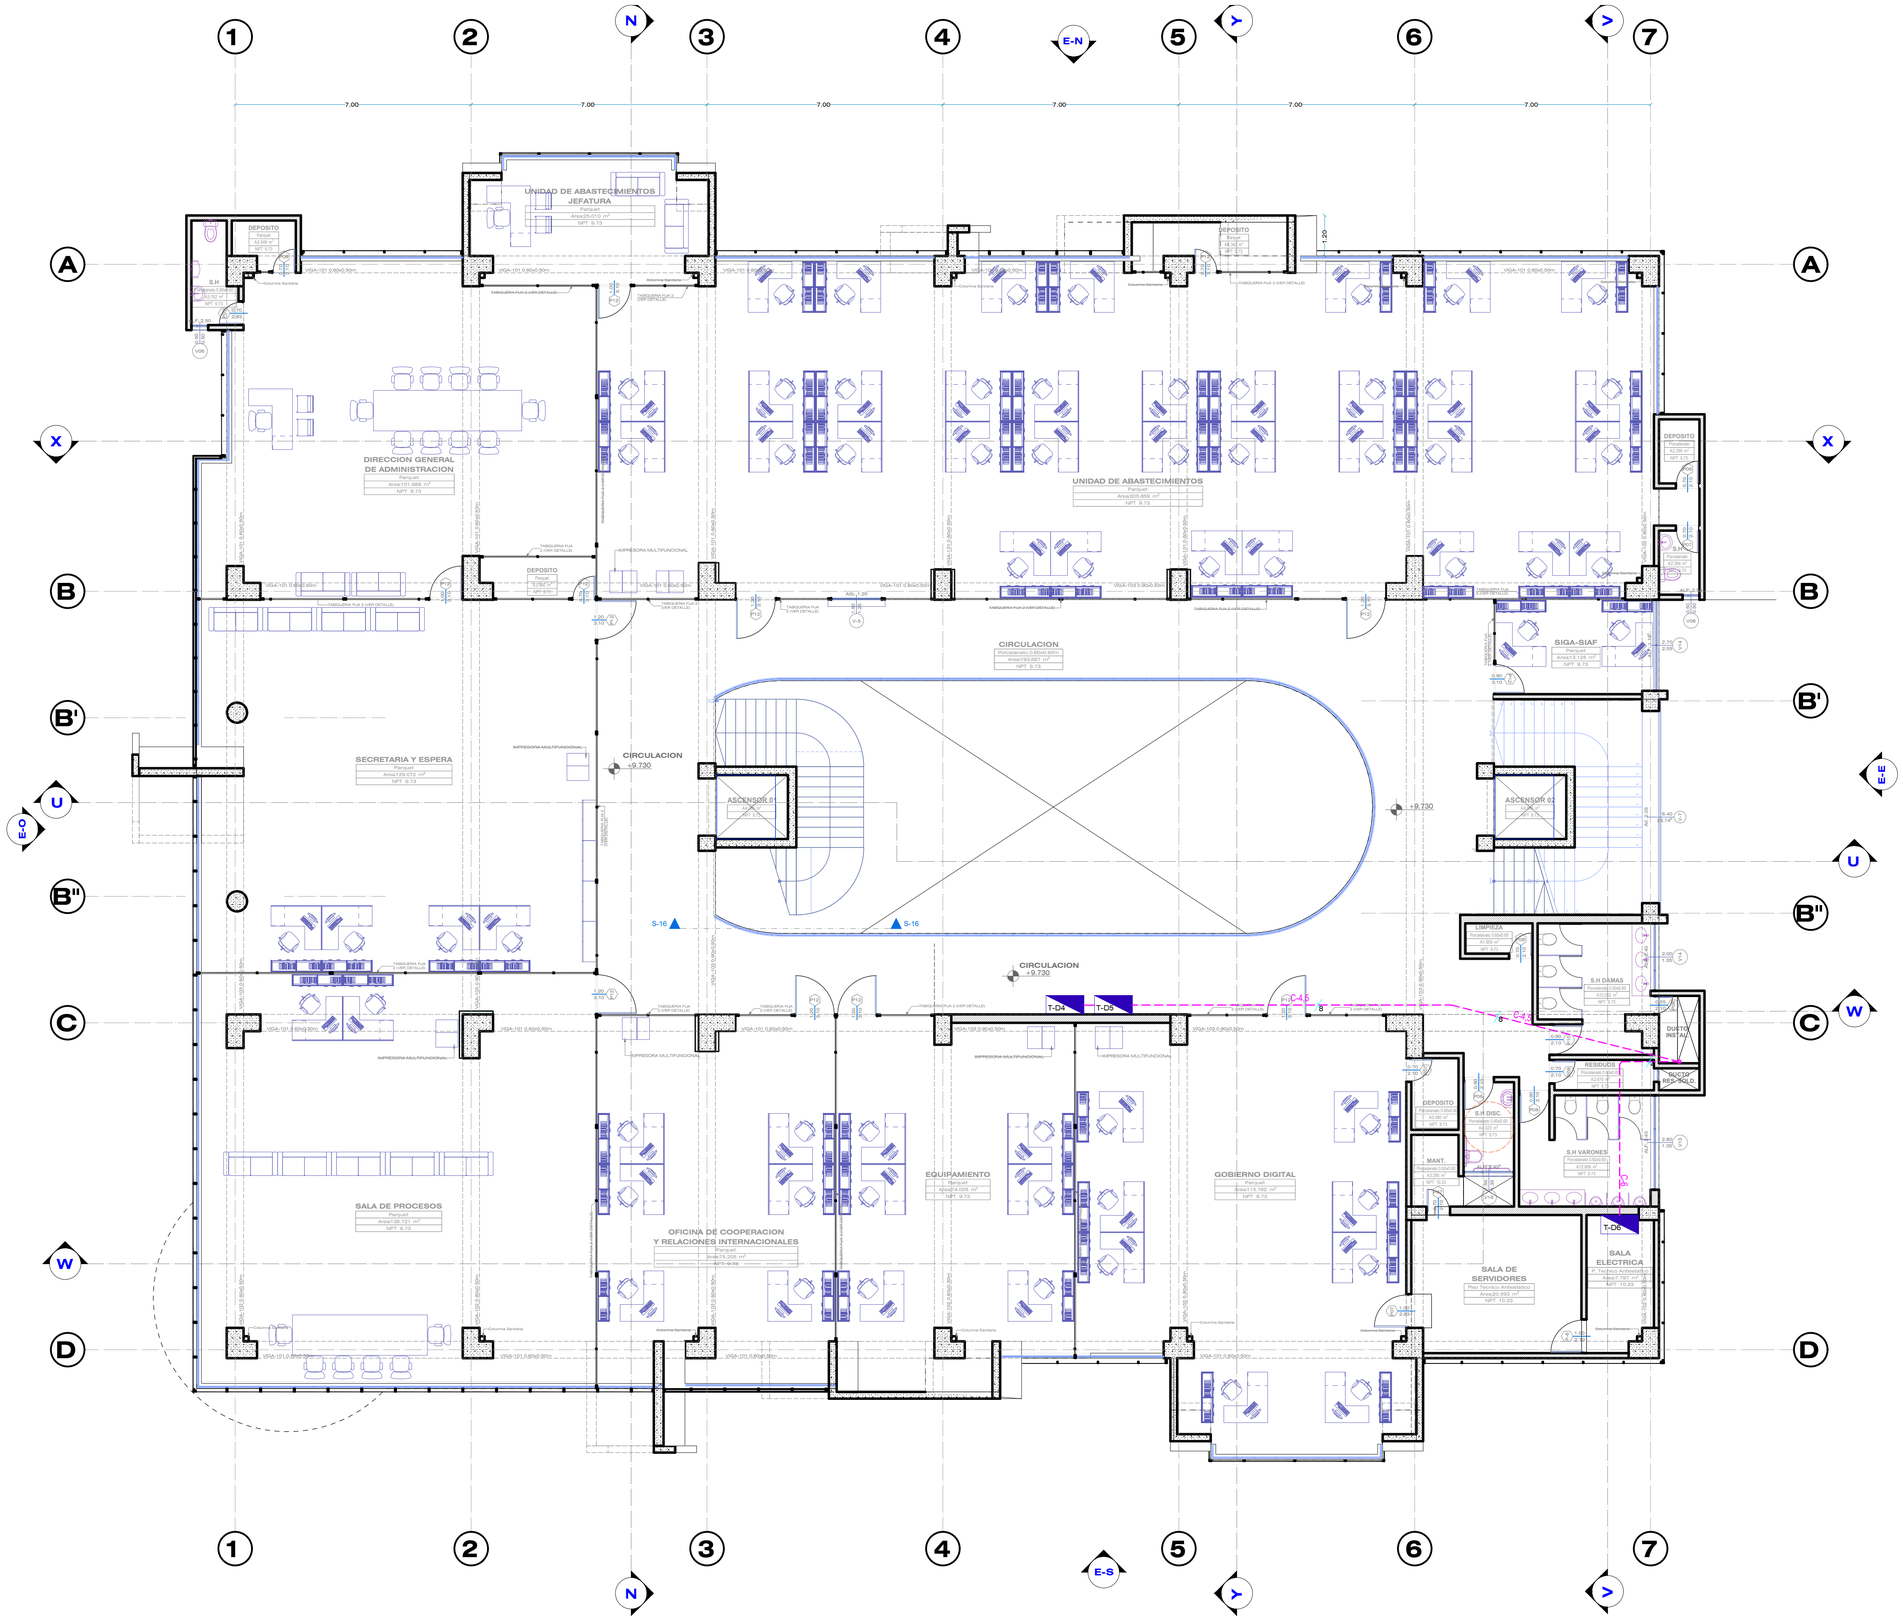

LEYENDA GENERAL

SIMBOLOS	DESCRIPCION	CAJAS (mm)	ALTURA s.n.p.t. (eje)
	SUBESTACION COMPACTA TIPO PEDESTAL PROYECTADO.	-----	-----
TG	TABLERO GENERAL ELECTRICA PARA SALIDAS NORMALES DE USO GENERAL EN LOS SECTORES EMPOTRADO SALVO INDICACION.	ESPECIAL	1.80m/ borde superior
TD	TABLERO DE DISTRIBUCION ELECTRICA PARA SALIDAS NORMALES DE USO GENERAL EN TODOS LOS SECTORES QUE CORRESPONDE.	ESPECIAL	1.80m/ borde superior
TTA	TABLERO DE TRANSFERENCIA IRA UBICADO ENTRE EL GRUPO ELECTROGENO Y EL TG	ESPECIAL	1.80m/ borde superior
STG	SUB TABLERO GENERAL (STG)	ESPECIAL	1.80m/ borde superior
TF	TABLERO DE FUERZA CONTROL DE ELECTROBOMBAS	ESPECIAL	1.80m/ borde superior
	BUZON DE BAJA TENSIÓN, SEGUN ESPECIFICACIONES TECNICAS.	-----	-----
	BUZON ELECTRICO DE CONCRETO SEGUN ESPECIFICACIONES TÉCNICAS EN POZO DE PUESTA A TIERRA	-----	-----
	POZO DE PUESTA A TIERRA CONVENCIONAL	-----	-----
	CIRCUITO DE ALIMENTADORES.	-----	-----
	CIRCUITO DE PUESTA A TIERRA DE PROTECCIÓN.	-----	-----
	REPRESENTACIÓN DEL NUMERO DE CONDUCTORES QUE TIEN UN CIRCUITO	-----	-----
	GRUPO ELECTROGENO TRIFASICO 380V/220V	-----	-----
	CIRCUITO DERIVADO DE TABLERO GENERAL A SUB TABLEROS DE DISTRIBUCION ELECTRICO PVC NT 12 ..... EMPOTRADO EN TECHO O PARED		
	CAJA DE PASO METALICO DE 4"X4" ESPESOR 1.2mm DE 150X150X80 mm PARA EMPOTRAR EN MURO.		
	CABLE DESNUDO DE 25 MM2, COBRE DE 7 HILOS PARA PUESTA A TIERRA.		

TERCER NIVEL
Escala1:75

0.
-

UNIVERSIDAD NACIONAL DEL ALTIPLANO PUNO

RECTOR:
DR.PAULINO MACHACA ARI
VICERECTOR ACADEMICO:
DR. MARIO S. CUENTAS ALVARADO
VICERECTOR DE INVESTIGACION:
DR. ARIEL VELAZCO CARDENAS

U.E.I
UNIDAD EJECUTORA DE INVERSIONES

SUB-UNIDAD DE ESTUDIOS

UNIDAD EJECUTORA DE INVERSIONES

JEFE UNIDAD EJECUTORA DE INVERSIONES:
ING. WILBER F. CAYRO ROJAS
JEFE SUB UNIDAD DE ESTUDIOS:
ING. ANDRES A. QUIZA AÑAZCO

ESPECIALIDAD:
INSTALACIONES ELECTRICAS

PLANO:
ALIMENTACIÓN TERCER NIVEL NIVEL

PROYECTO:
"MEJORAMIENTO DE LA GESTIÓN INSTITUCIONAL EN EDUCACIÓN UNIVERSITARIA DE LOS SERVICIOS ADMINISTRATIVOS DE LA UNIVERSIDAD NACIONAL DEL ALTIPLANO, DISTRITO DE PUNO -PROVINCIA DE PUNO - DEPARTAMENTO DE PUNO"

COMPONENTE:
"ADECUADA Y SUFICIENTE INFRAESTRUCTURA PARA LABOR ADMINISTRATIVA EN LA UNIVERSIDAD"

DESARROLLO PROYECTO INSTALACIONES ELECTRICAS:
ING. ANTERO NEFTALI AJROTA MAQUERA

LOCALIZACION:
BARRIO BELLAVISTA
AV. EL SOL N° 329

UBICACION:
DPTO. PUNO
PROV. PUNO
DISTR. PUNO

DIBUJO: SUB UNIDAD DE ESTUDIOS
FECHA: FEBRERO 2023
ESCALA: INDICADA
LAMINA: **IE-AL3**