



| CÁLCULO DE MÁXIMA DEMANDA |                            |                              |                   |      |                            |                                 |                          |                                        |
|---------------------------|----------------------------|------------------------------|-------------------|------|----------------------------|---------------------------------|--------------------------|----------------------------------------|
| ITEM                      | DESCRIPCIÓN                | POTENCIA<br>INSTALADA<br>(W) | CANTIDAD<br>(UND) | F.P. | POTENCIA<br>PARCIAL<br>(W) | POTENCIA<br>POR CIRCUITO<br>(W) | POTENCIA<br>TOTAL<br>(W) | CORRIENTE<br>DISEÑO (A)<br>1.25Ino (A) |
| T0                        | TABLERO GENERAL            |                              |                   |      |                            |                                 | 170,829.92               | 324.82                                 |
| C-0                       | SUB TABLERO GENERAL        |                              |                   |      |                            |                                 | 20,273.32                | 38.55                                  |
| C-1                       | TABLERO DE DISTRIBUCION 1  |                              |                   |      |                            |                                 | 14,779.00                | 28.10                                  |
| C-2                       | TABLERO DE DISTRIBUCION 2  |                              |                   |      |                            |                                 | 17,709.00                | 33.67                                  |
| C-3                       | TABLERO DE DISTRIBUCION 3  |                              |                   |      |                            |                                 | 10,816.00                | 20.57                                  |
| C-4                       | TABLERO DE DISTRIBUCION 4  |                              |                   |      |                            |                                 | 12,064.00                | 22.94                                  |
| C-5                       | TABLERO DE DISTRIBUCION 5  |                              |                   |      |                            |                                 | 13,351.00                | 25.39                                  |
| C-6                       | TABLERO DE DISTRIBUCION 6  |                              |                   |      |                            |                                 | 7,200.00                 | 13.69                                  |
| C-7                       | TABLERO DE DISTRIBUCION 7  |                              |                   |      |                            |                                 | 16,642.00                | 31.64                                  |
| C-8                       | TABLERO DE DISTRIBUCION 8  |                              |                   |      |                            |                                 | 13,093.00                | 24.90                                  |
| C-9                       | TABLERO DE DISTRIBUCION 9  |                              |                   |      |                            |                                 | 14,861.00                | 28.26                                  |
| C-10                      | TABLERO DE DISTRIBUCION 10 |                              |                   |      |                            |                                 | 11,585.00                | 22.03                                  |
| C-11                      | TABLERO DE DISTRIBUCION 11 |                              |                   |      |                            |                                 | 1,960.00                 | 3.73                                   |
| C-12                      | TABLERO DE DISTRIBUCION 12 |                              |                   |      |                            |                                 | 8,215.00                 | 15.62                                  |
| C-13                      | TABLERO DE DISTRIBUCION 13 |                              |                   |      |                            |                                 | 8,290.00                 | 15.74                                  |

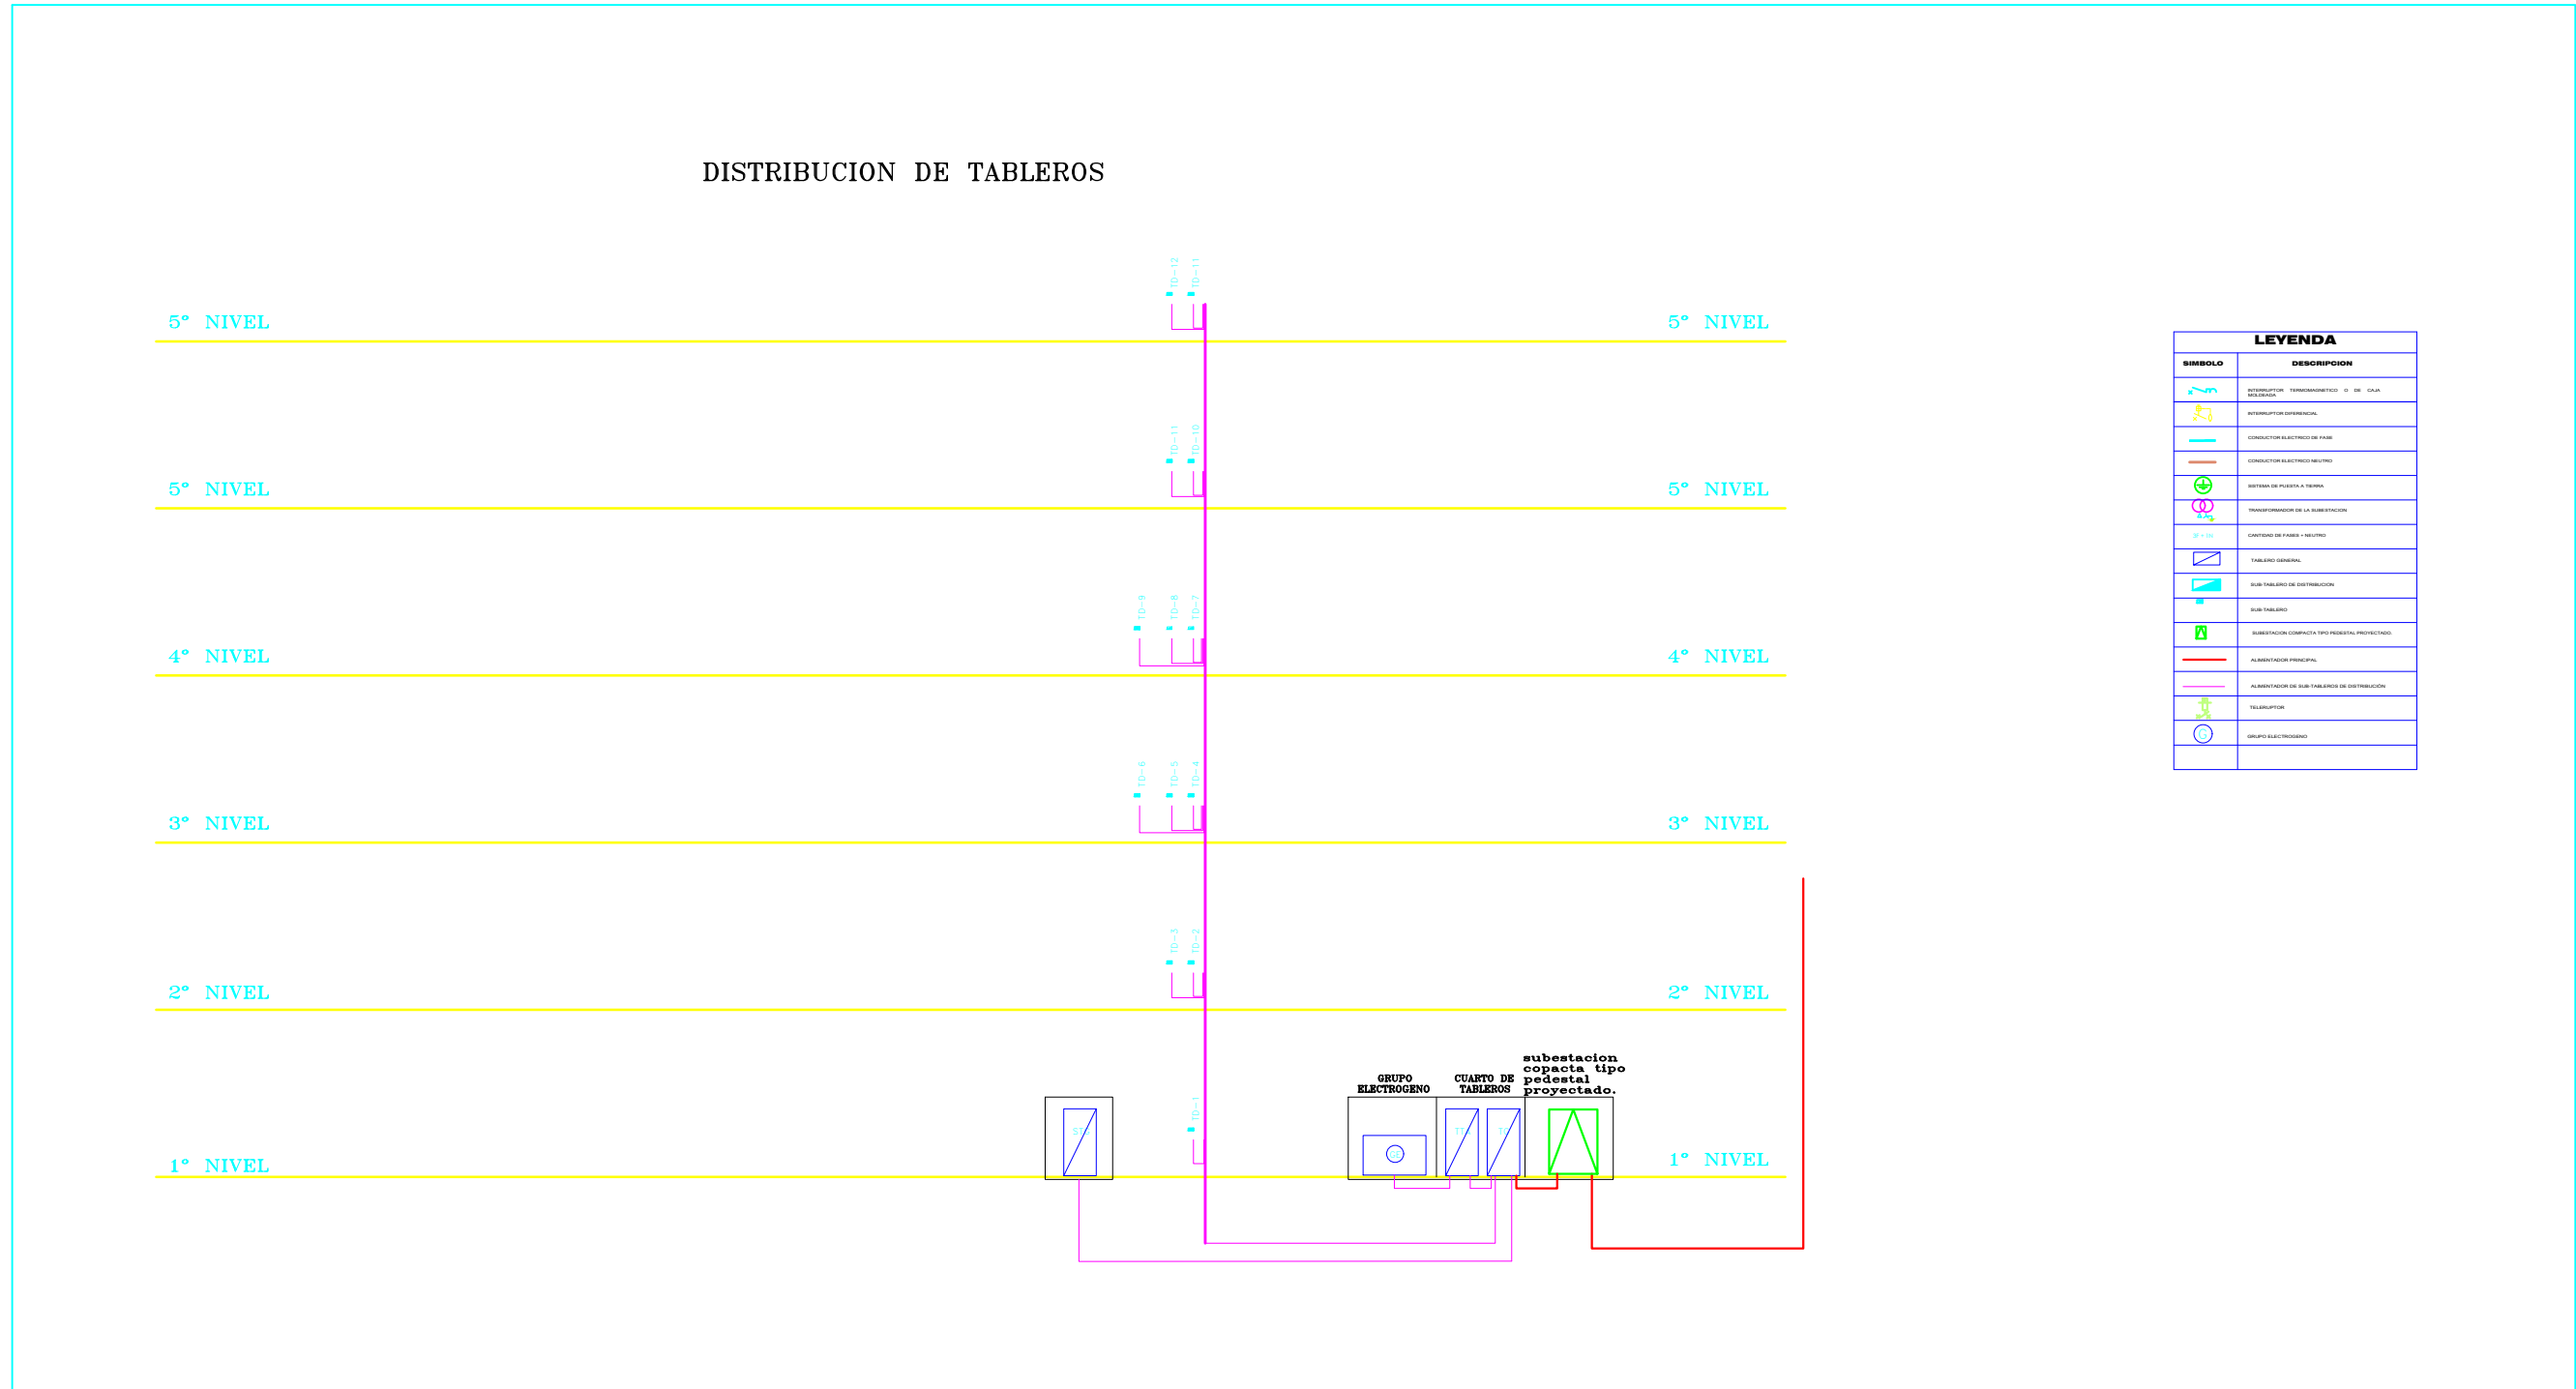


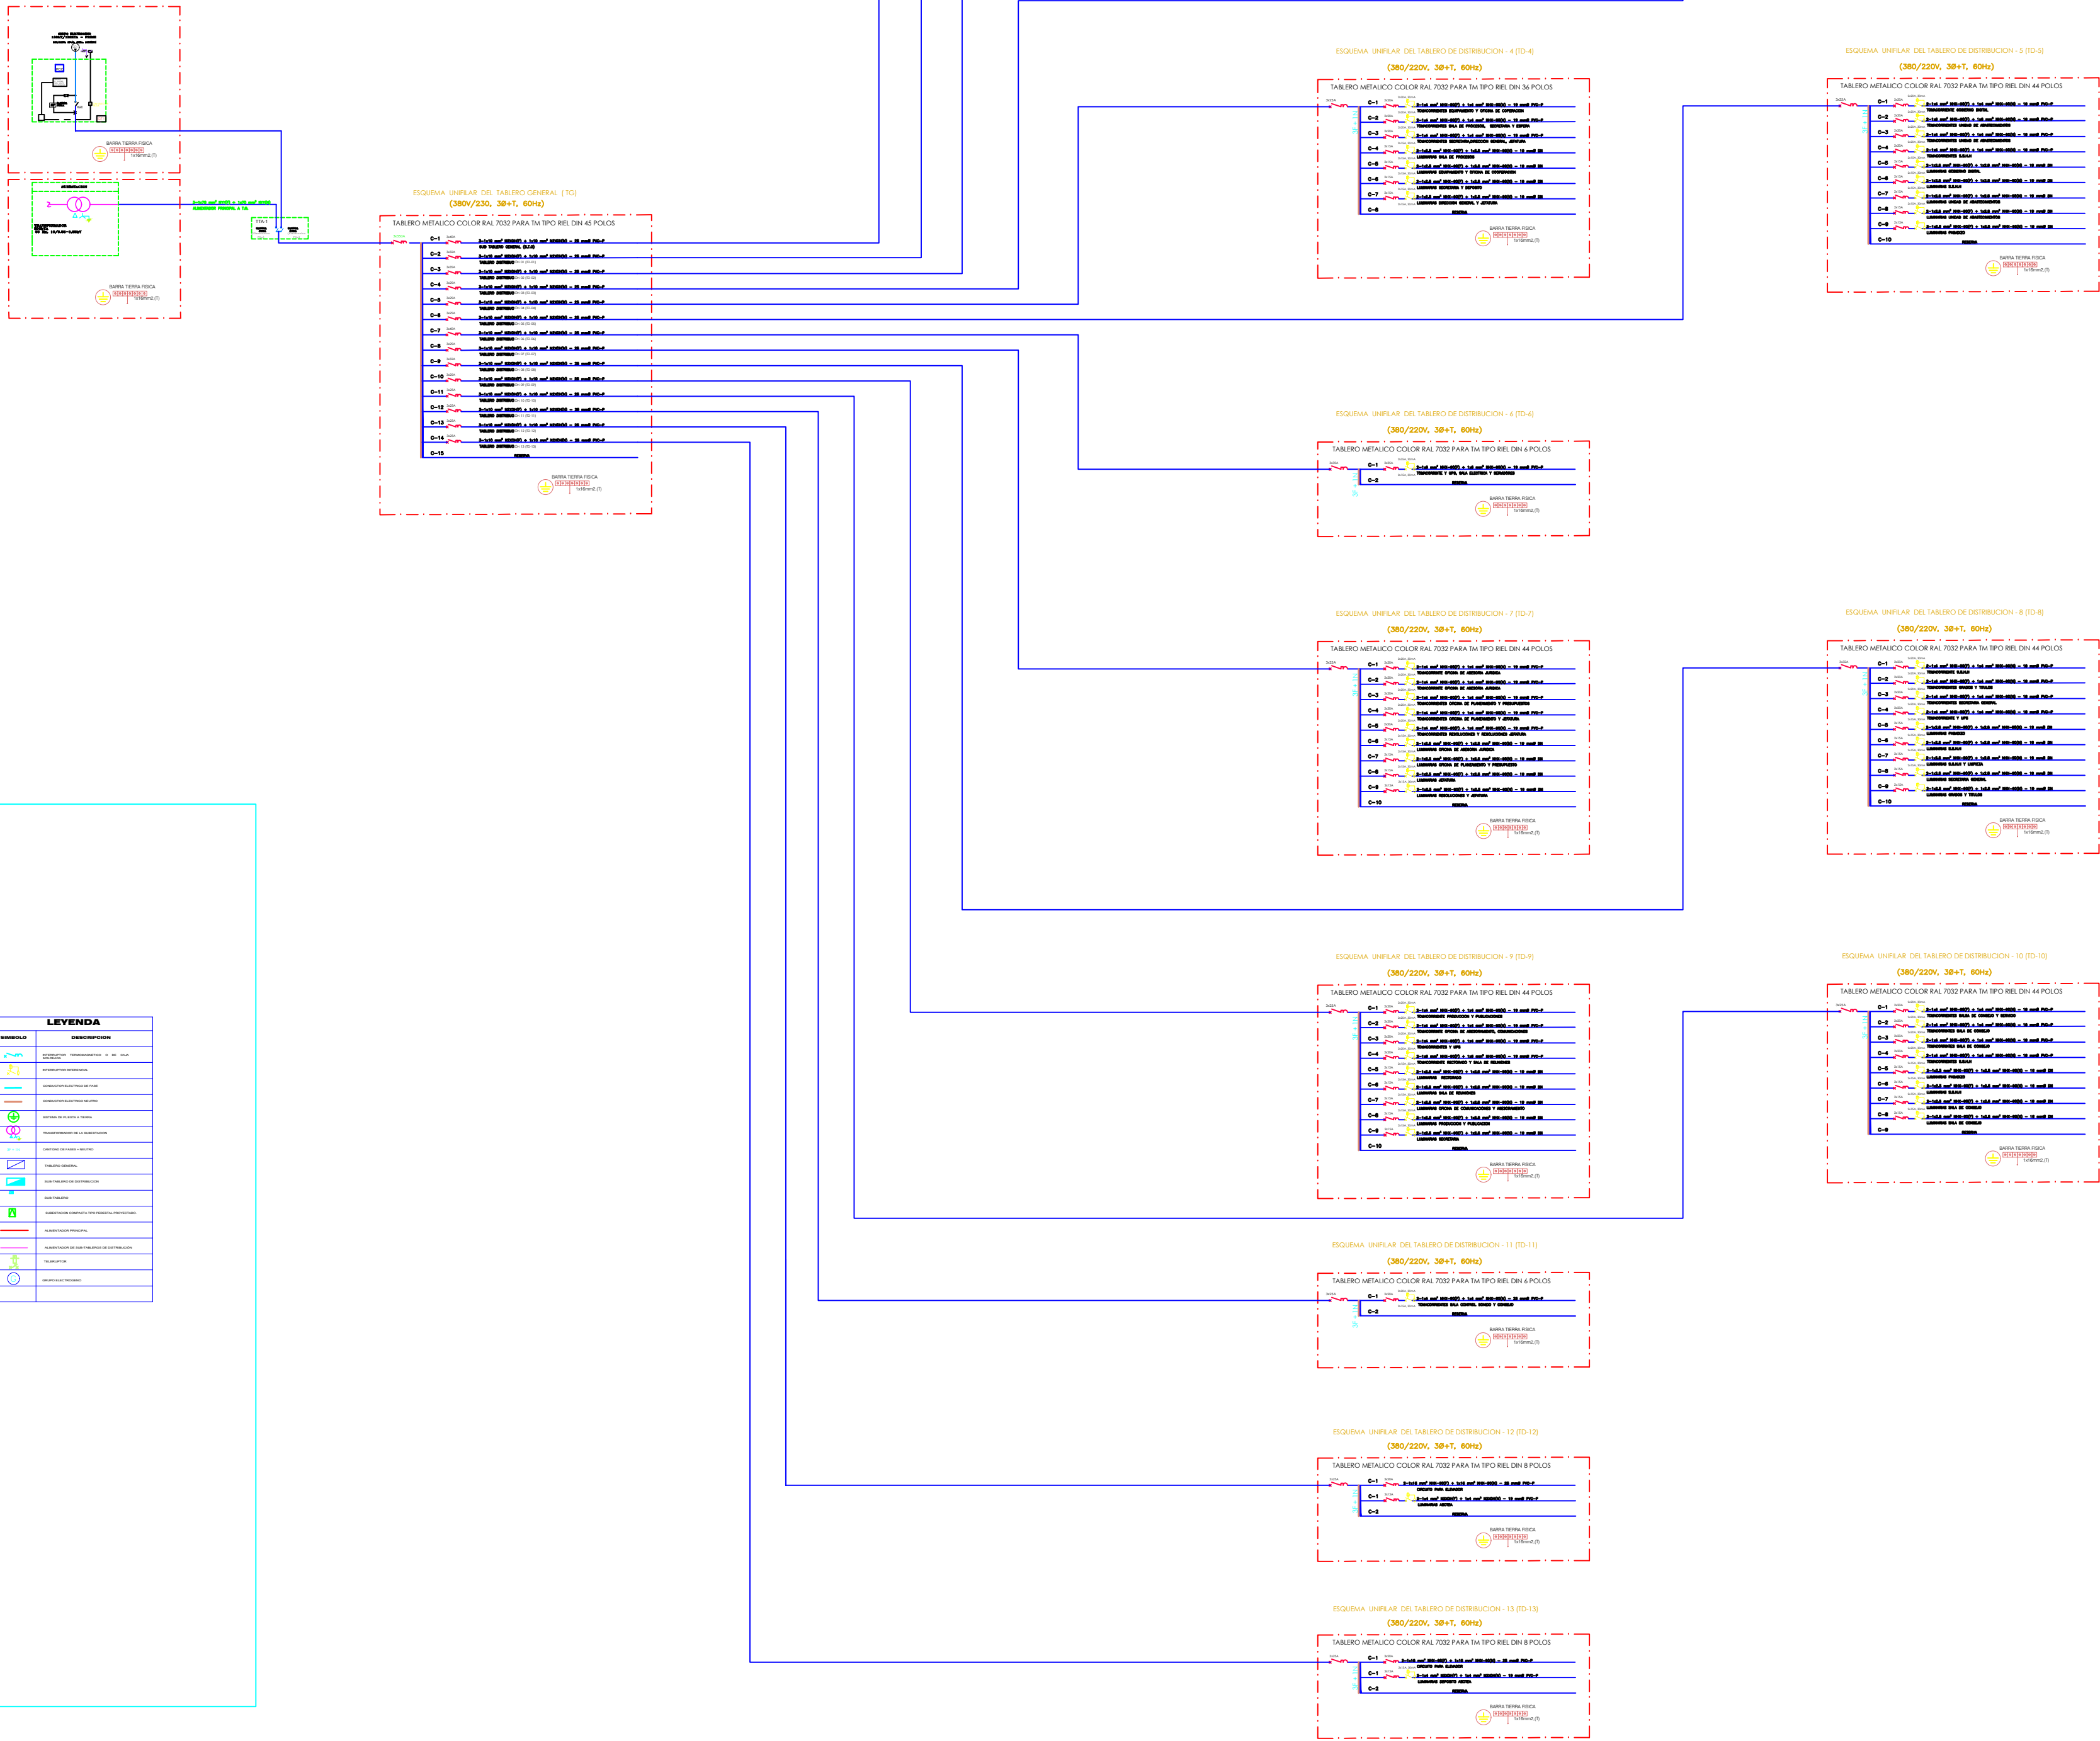

RECTOR  
DR. PAULINO MACHACA ARI  
VICERECTOR GENERAL  
DR. MARIO S. CUENTAS ALVARADO  
VICERECTOR DE INVESTIGACION  
DR. ARIEL VELAZCO CARDENAS

**U.E.I.**  
UNIDAD EJECUTORA  
DE INVERSIONES

SUB-UNIDAD  
DE ESTUDIOS

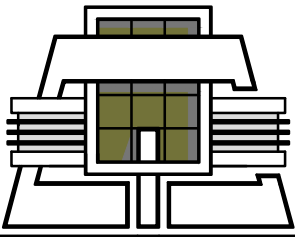

JEFE SUB-UNIDAD DE ESTUDIOS  
ING. WILBER F. CAYRO ROJAS  
JEFE LABORATORIO DE INVESTIGACION  
ING. ANDRES A. QUIZA AÑAZCO

PROYECTO  
INSTALACIONES  
ELECTRICAS

PAIS  
**DIAGRAMA UNIFILAR**

OBJETIVO  
"MEJORAMIENTO DE LA  
GESTION INSTITUCIONAL EN  
EDUCACION UNIVERSITARIA  
DE LOS SERVICIOS  
ADMINISTRATIVOS DE LA  
UNIVERSIDAD NACIONAL DEL  
ALTIPLANO, DISTRITO DE  
PUNO - PROVINCIA DE PUNO  
- DEPARTAMENTO DE PUNO"

OBJETIVO  
"ADECUADA Y SUFICIENTE  
INFRAESTRUCTURA PARA  
LABOR ADMINISTRATIVA  
EN LA UNIVERSIDAD"

COORDINADOR GENERAL DE INVESTIGACION  
ING. ANTERO NEFTALI AJROTA MAQUERA

PROYECTISTA  
BARRIO BELLAVISTA  
AV. EL SOL N° 320

UBICACION  
DFTO. PUNO  
PROV. PUNO  
DISTR. PUNO

FECHA  
FEBRERO 2023

INDICADA

