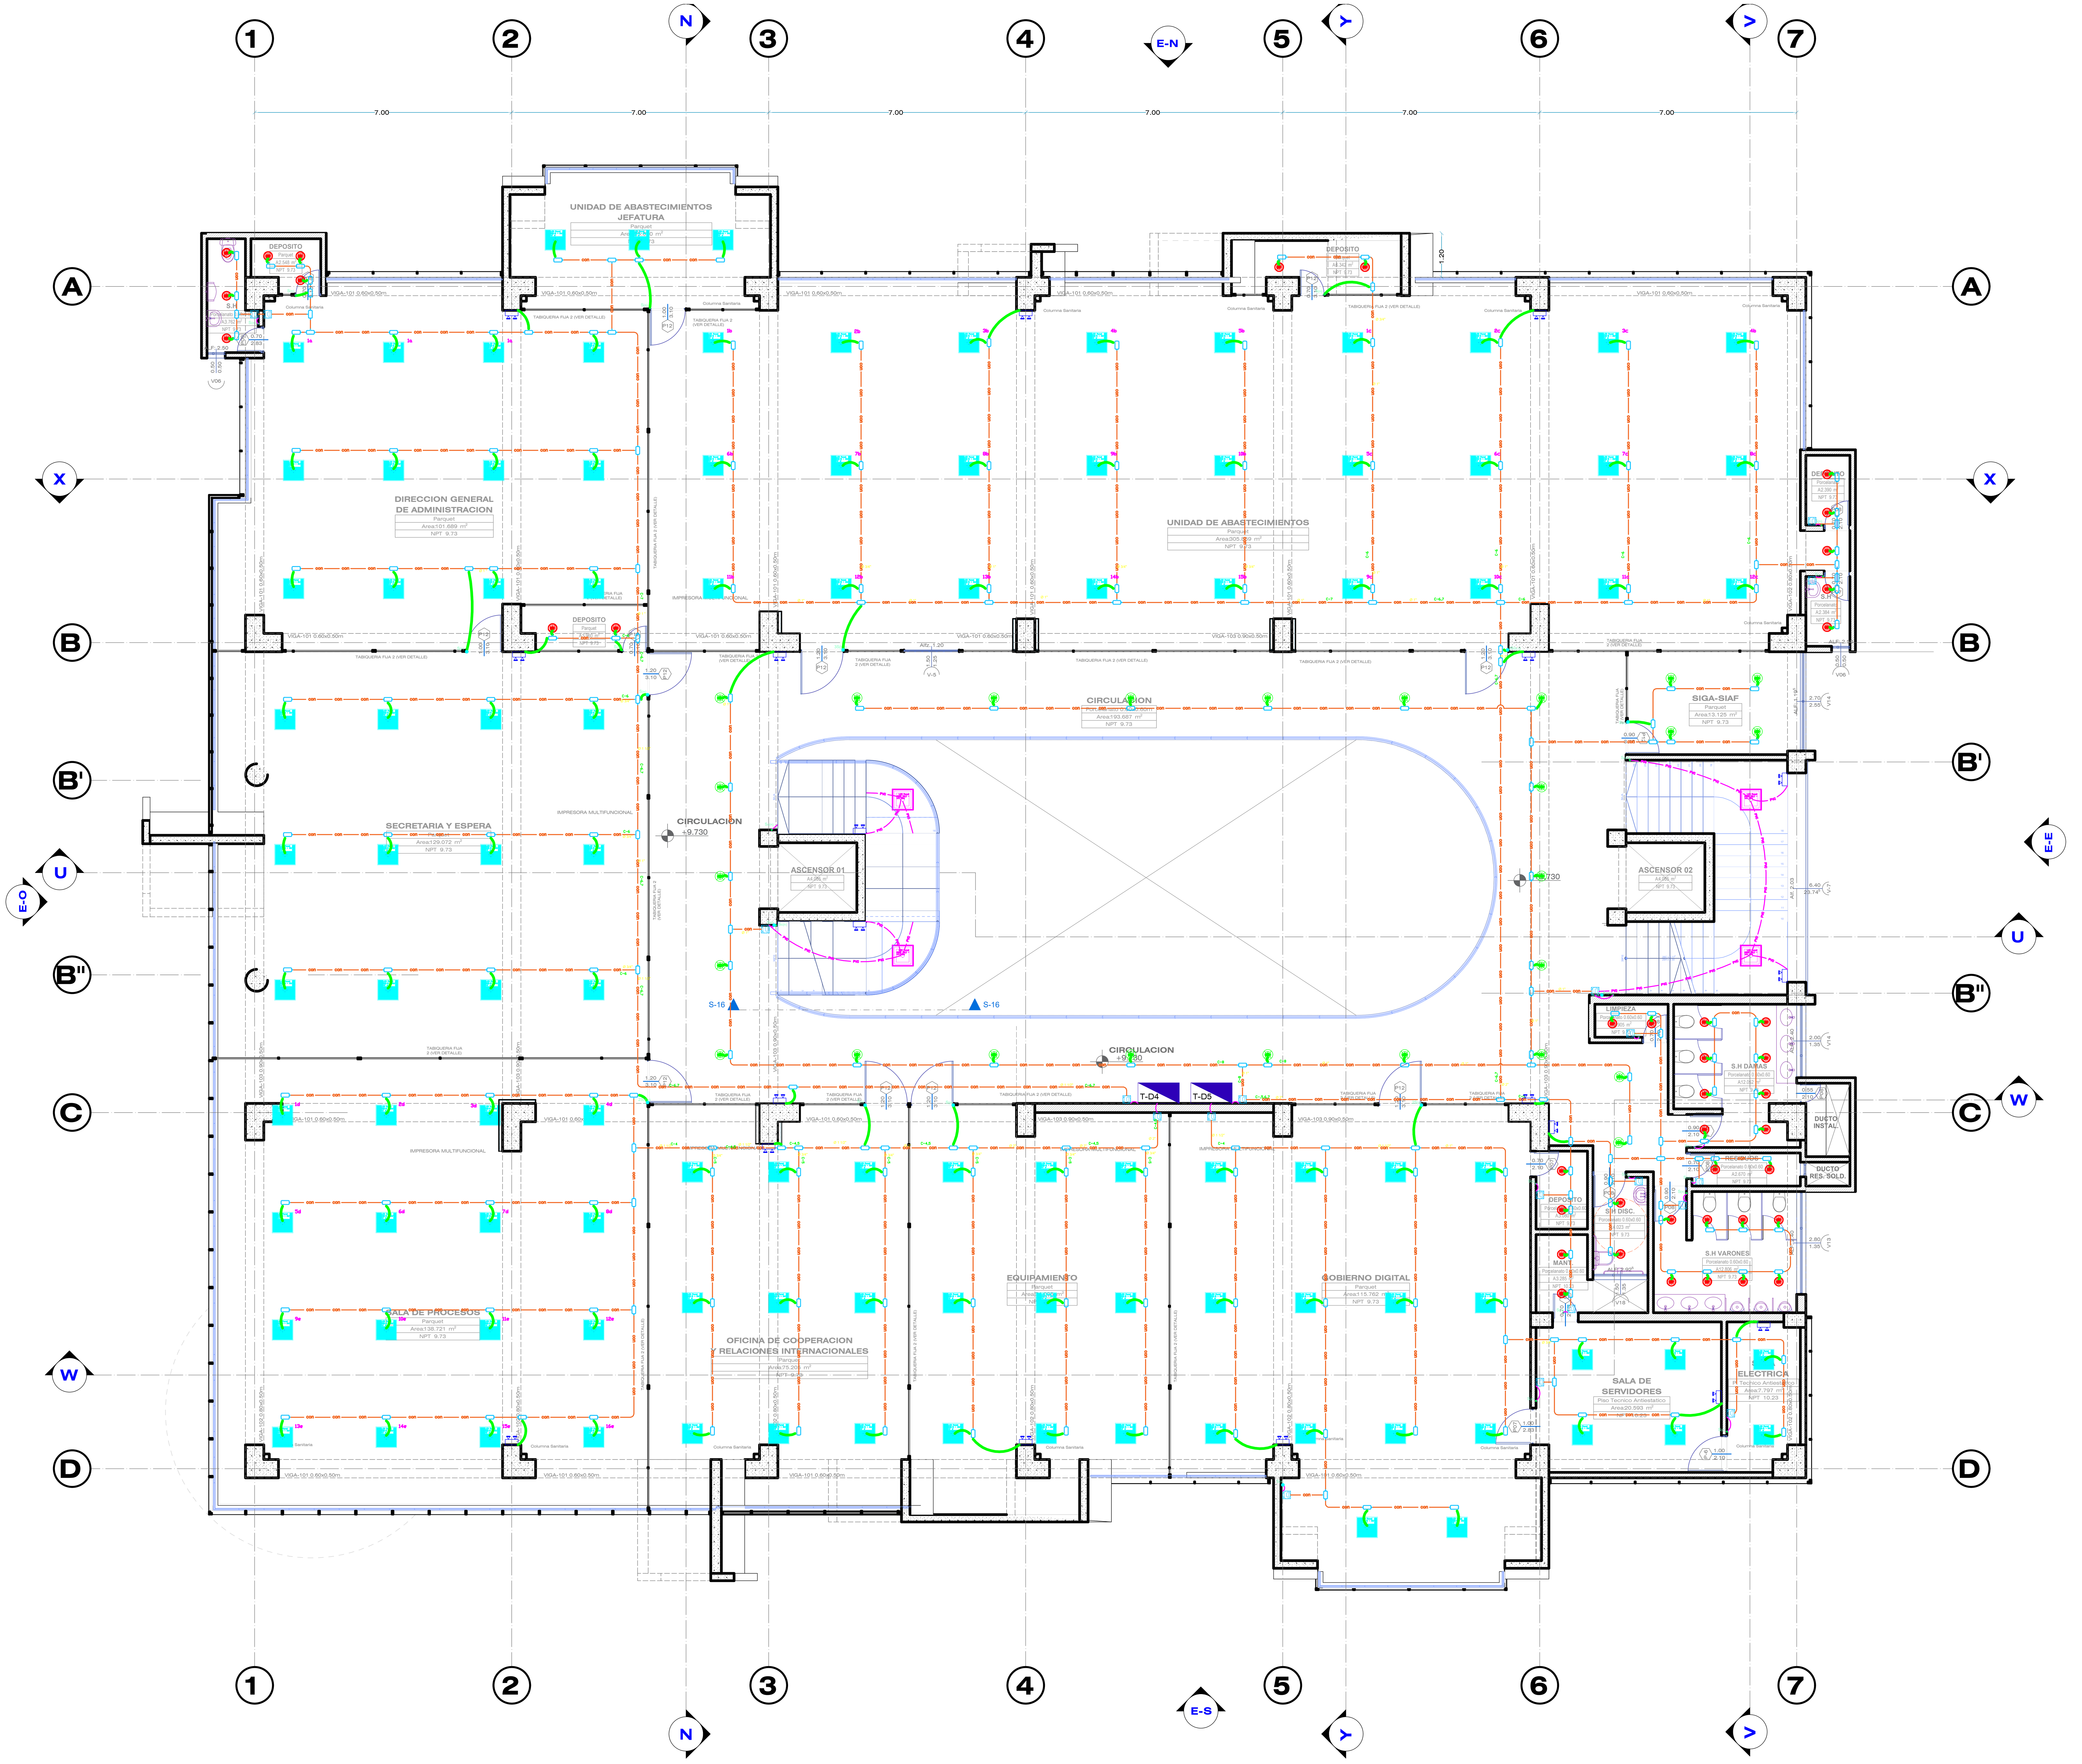

TERCER NIVEL
Escala1:75

LEYENDA

SIMBOLO	DESCRIPCION	MONTAJE (NPT+) METROS
	LUMINARIA LED LP626201DA TIPO PANEL 42 W. PARA ADOSAR DE 0.60x0.60x0.074 m DE 4000 lm.	4.83 m
	LUMINARIA LED L800L528PD TIPO PANEL 47 W. PARA ADOSAR, DE 0.60X0.60 m DE 5650 Lm.	TECHO
	LUMINARIA LED DN145B PSD D218 1xLED20S/840 TIPO DOWNLIGHT 22.5 W PARA ADOSAR DE 0.218x0.218x0.033m DE 2100 lm,	TECHO
	LUMINARIA LED DN145B PSD D166 1 xLED10S/840 TIPO DOWNLIGHT 13 W PARA ADOSAR DE 0.166x0.166x0.030m DE 1100 lm	TECHO
	LUMINARIA LED DE 45W TIPO BRAQUET PERIMETRAL P/ADOSAR A PARED 4050lm/CRI≥80/FP≥ 0.90/ VIDA UTIL ≥ 50000 HORAS/≥6000 K	2.50m PARED
T-D	TABLERO DE DISTRIBUCIÓN EMPOTRADO DE TENSION NORMAL CON BARRA DE COBRE PARA NEUTRO Y TIERRA	1.80m borde superior
	INTERRUPTOR SIMPLE, DOBLE Y TRIPLE.	1.20m pared
	INTERRUPTOR CONMUTADO SIMPLE, DOBLE, TRIPLE.	1.20m pared
	CIRCUITO DERIVADO CON CONDUCTOR LSOH, DE SECCION INDICADA, EN ELECTRODUCTO CONDUIT ADOSADO EN LOSA ALIGERADA Y/O SUSPENDIDO SEGUN LO INDICADO EN LOS DETALES DE INSTALACION	techo
	CIRCUITO DERIVADO CON CONDUCTOR LSOH, DE SECCION INDICADA, EN ELECTRODUCTO CONDUIT EMT FLEXIBLE SUSPENDIDO DE CAJA DE CONEXIONES AL ARTEFACTO.	techo
	CIRCUITO DERIVADO CON CONDUCTOR LSOH, DE SECCION INDICADA, EN ELECTRODUCTO PVC-P EMPOTRADO EN PISO Y/O PARED	piso
	CIRCUITO DERIVADO CON CONDUCTOR LSOH, DE SECCION INDICADA EN DIAGRAMA UNIFILAR, EN ELECTRODUCTO PCV-P EMPOTRADO EN LOSA ALIGERADA Y/O PARED	pared/techo
	INDICADOR DE NUMERO DE CONDUCTORES EN EL DUCTO (FASES, NETRO, RETORNOS Y TIERRA).	--
PIR	SENSOR INFRARROJO PASIVO, MODALIDAD FUNCIONAMIENTO AUTOMATICO, TIPO INSTALACION ADOSADO.	techo
	CAJA DE OCTAGONAL METALICO DE F°G° ESPESOR 1.2mm DE 100x55 mm. PARA ADOSAR EN PARED	0.80m pared
	CAJA DE PASE METALICO DE F°G° ESPESOR 1.2mm DE 100X100X80 mm. PARA ADOSAR EN TECHO	0.20m pared desde FCR
	CAJA DE PASE METALICO DE F°G° ESPESOR 1.2mm DE 150X150X80 mm. PARA EMPOTRAR EN MURO	0.40m pared
	CAJA DE CONDULET OCTAGONAL DE ALUMINIO INYECTADO A PRESION, CON TAPA DE LAMINA DE ALUMINIO Y EMPAQUE, TORNILLOS DE GALVANIZADO	techo
	CAJA DE REGISTRO OVAL TIPO OLL (DOS SALIDAS) P/ TUBO CONDUIT DE 20mm DE MATERIAL ALUMINIO NYECTADO A PRESION, CON TAPA DE LAMINA DE ALUMINIO Y EMPAQUE, TORNILLOS DE GALVANIZADO.	techo
	CAJA DE REGISTRO OVAL TIPO C (DOS SALIDAS) P/ TUBO CONDUIT DE 20mm DE MATERIAL ALUMINIO NYECTADO A PRESION, CON TAPA DE LAMINA DE ALUMINIO Y EMPAQUE, TORNILLOS DE GALVANIZADO.	techo
	CAJA DE REGISTRO OVAL TIPO X (CUATRO SALIDAS) P/ TUBO CONDUIT DE 20mm DE MATERIAL ALUMINIO NYECTADO A PRESION, CON TAPA DE LAMINA DE ALUMINIO Y EMPAQUE, TORNILLOS DE GALVANIZADO.	techo
	CAJA DE REGISTRO OVAL TIPO T (TRES SALIDAS) P/ TUBO CONDUIT DE 20mm DE MATERIAL ALUMINIO NYECTADO A PRESION, CON TAPA DE LAMINA DE ALUMINIO Y EMPAQUE, TORNILLOS DE GALVANIZADO.	techo
	PULSADOR CONMUTADO SIMPLE, DOBLE, TRIPLE.	1.20m pared
	ARTEFACTO PARA ALUMBRADO DE EMERGENCIA CON 02 FOCOS LED DE ALTA POTENCIA DE 2x18W, 220V, 60Hz, 4000LM, MODELO KC 2000 LED, SIMILAR A KOLFF.	--

RECTOR:
DR.PAULINO MACHACA ARI
VICERECTOR ACADEMICO:
DR. MARIO S. CUENTAS ALVARADO
VICERECTOR DE INVESTIGACION:
DR. ARIEL VELAZCO CARDENAS

U.E.I
UNIDAD EJECUTORA DE INVERSIONES

SUB-UNIDAD DE ESTUDIOS

UNIDAD EJECUTORA DE INVERSIONES

JEFE UNIDAD EJECUTORA DE INVERSIONES:
ING. WILBER F. CAYRO ROJAS
JEFE SUB UNIDAD DE ESTUDIOS:
ING. ANDRES A. QUIZA AÑAZCO

ESPECIALIDAD:
INSTALACIONES ELECTRICAS

PLANO:
ILUMINACIÓN TERCER NIVEL NIVEL

PROYECTO:
"MEJORAMIENTO DE LA GESTIÓN INSTITUCIONAL EN EDUCACIÓN UNIVERSITARIA DE LOS SERVICIOS ADMINISTRATIVOS DE LA UNIVERSIDAD NACIONAL DEL ALTIPLANO, DISTRITO DE PUNO -PROVINCIA DE PUNO - DEPARTAMENTO DE PUNO"

COMPONENTE:
"ADECUADA Y SUFICIENTE INFRAESTRUCTURA PARA LABOR ADMINISTRATIVA EN LA UNIVERSIDAD"

DESARROLLO PROYECTO INSTALACIONES ELÉCTRICAS:
ING. ANTERO NEFTALI AJROTA MAQUERA

LOCALIZACION:
BARRIO BELLAVISTA
AV. EL SOL N° 329

UBICACION:
DPTO. PUNO
PROV. PUNO
DISTR. PUNO

DIBUJO:
SUB UNIDAD DE ESTUDIOS

FECHA:
FEBRERO 2023

ESCALA:
INDICADA

LAMINA:
IE-IL3

0.
-