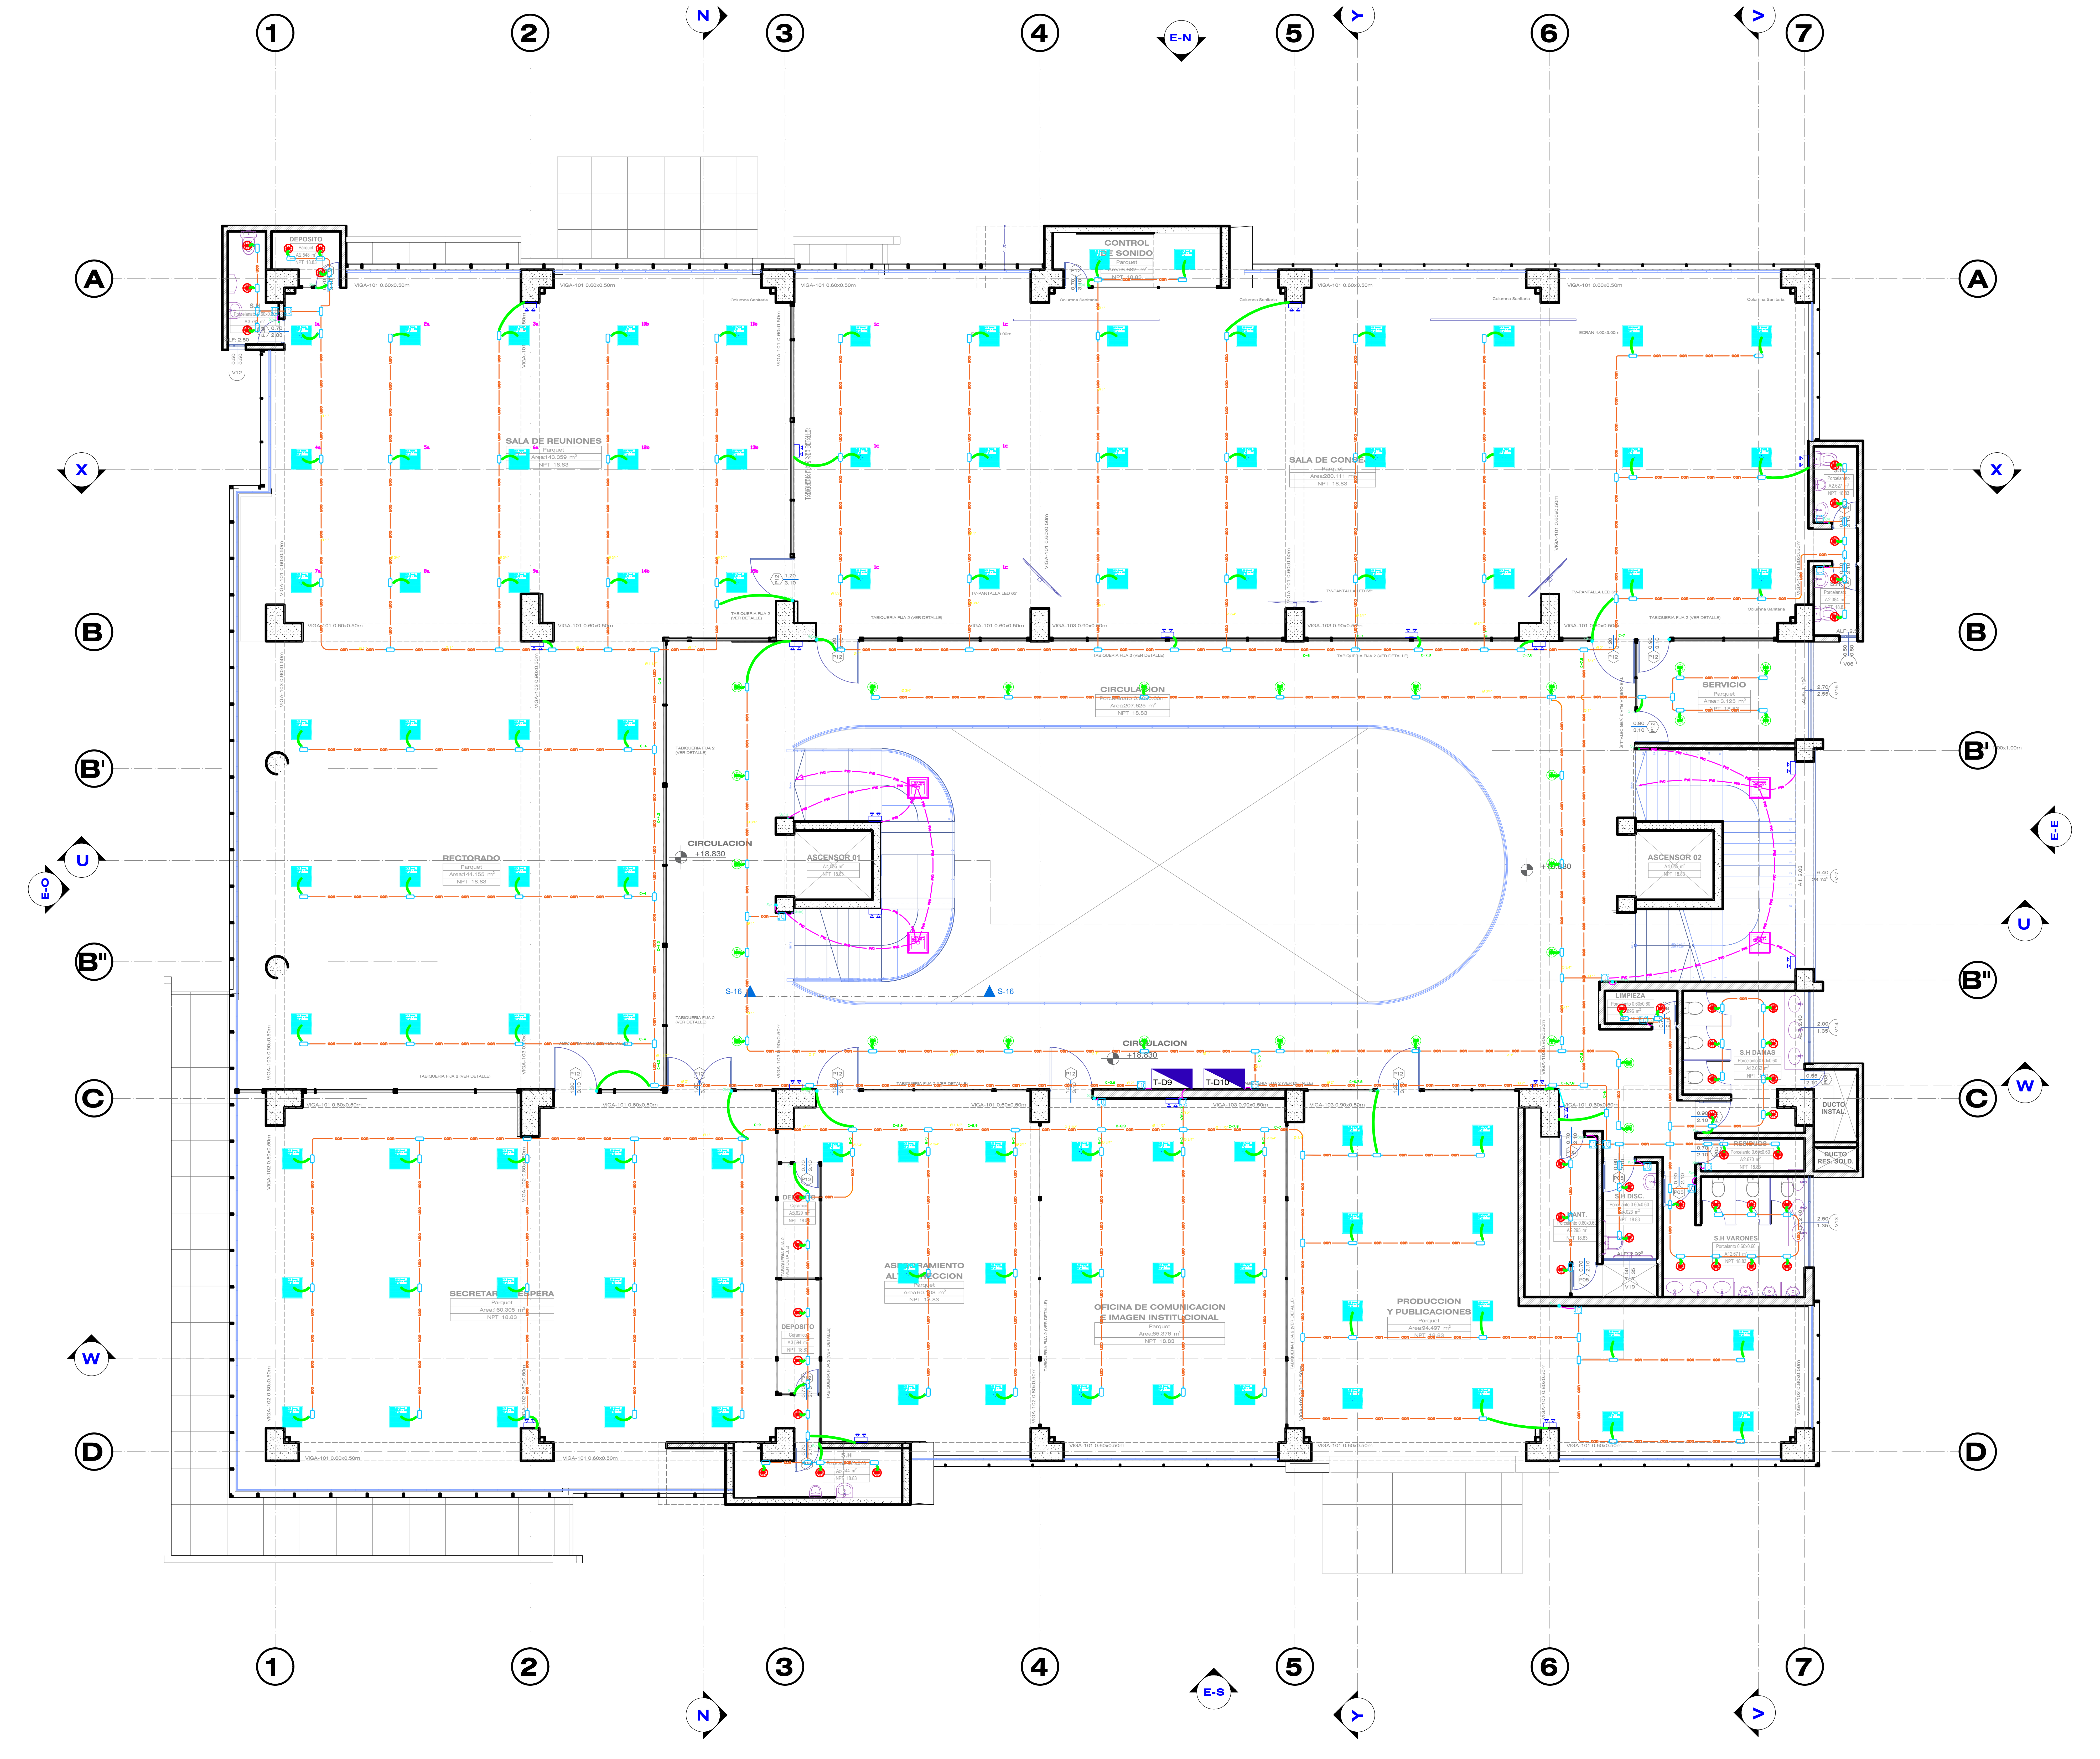

0.
-

QUINTO NIVEL

Escala1:75

LEYENDA

SIMBOLO	DESCRIPCION	MONTAJE (NPT+) METROS
🟪	LUMINARIA LED LP626201DA TIPO PANEL 42 W. PARA ADOSAR DE 0.60x0.60x0.074 m DE 4000 lm.	*4.83 m*
🟦	LUMINARIA LED L800L528PD TIPO PANEL 47 W. PARA ADOSAR, DE 0.60X0.60 m DE 5650 Lm.	*TECHO*
🟢	LUMINARIA LED DN145B PSD D218 1xLED20S/840 TIPO DOWNLIGHT 22.5 W PARA ADOSAR DE 0.218x0.218x0.033m DE 2100 lm,	*TECHO*
🔴	LUMINARIA LED DN145B PSD D166 1 xLED10S/840 TIPO DOWNLIGHT 13 W PARA ADOSAR DE 0.166x0.166x0.030m DE 1100 lm	*TECHO*
⊕	LUMINARIA LED DE 45W TIPO BRAQUET PERIMETRAL P/ADOSAR A PARED 4050lm/CRI≥80/FP≥ 0.90/ VIDA UTIL ≥ 50000 HORAS/≥6000 K	*2.50m PARED*
T-D	TABLERO DE DISTRIBUCIÓN EMPOTRADO DE TENSION NORMAL CON BARRA DE COBRE PARA NEUTRO Y TIERRA	*1.80m borde superior*
•	INTERRUPTOR SIMPLE, DOBLE Y TRIPLE.	*1.20m pared*
•	INTERRUPTOR CONMUTADO SIMPLE, DOBLE, TRIPLE.	*1.20m pared*
— con — con — con —	CIRCUITO DERIVADO CON CONDUCTOR LSOH, DE SECCION INDICADA, EN ELECTRODUCTO CONDUIT ADOSADO EN LOSA ALIGERADA Y/O SUSPENDIDO SEGUN LO INDICADO EN LOS DETALES DE INSTALACION	*techo*
— CF — CF — CF —	CIRCUITO DERIVADO CON CONDUCTOR LSOH, DE SECCION INDICADA, EN ELECTRODUCTO CONDUIT EMT FLEXIBLE SUSPENDIDO DE CAJA DE CONEXIONES AL ARTEFACTO.	*techo*
- - - -	CIRCUITO DERIVADO CON CONDUCTOR LSOH, DE SECCION INDICADA, EN ELECTRODUCTO PVC-P EMPOTRADO EN PISO Y/O PARED	*piso*
— PVC — PVC —	CIRCUITO DERIVADO CON CONDUCTOR LSOH, DE SECCION INDICADA EN DIAGRAMA UNIFILAR, EN ELECTRODUCTO PCV-P EMPOTRADO EN LOSA ALIGERADA Y/O PARED	*pared/techo*
T‖	INDICADOR DE NUMERO DE CONDUCTORES EN EL DUCTO (FASES, NETRO, RETORNOS Y TIERRA).	--
PIR	SENSOR INFRARROJO PASIVO, MODALIDAD FUNCIONAMIENTO AUTOMATICO, TIPO INSTALACION ADOSADO.	*techo*
⊗	CAJA DE OCTAGONAL METALICO DE F°G° ESPESOR 1.2mm DE 100x55 mm. PARA ADOSAR EN PARED	*0.80m pared*
10	CAJA DE PASE METALICO DE F°G° ESPESOR 1.2mm DE 100X100X80 mm. PARA ADOSAR EN TECHO	*0.20m pared desde FCR*
P10	CAJA DE PASE METALICO DE F°G° ESPESOR 1.2mm DE 150X150X80 mm. PARA EMPOTRAR EN MURO	*0.40m pared*
⊗	CAJA DE CONDULET OCTAGONAL DE ALUMINIO INYECTADO A PRESION, CON TAPA DE LAMINA DE ALUMINIO Y EMPAQUE, TORNILLOS DE GALVANIZADO	*techo*
▭	CAJA DE REGISTRO OVAL TIPO OLL (DOS SALIDAS) P/ TUBO CONDUIT DE 20mm DE MATERIAL ALUMINIO NYECTADO A PRESION, CON TAPA DE LAMINA DE ALUMINIO Y EMPAQUE, TORNILLOS DE GALVANIZADO.	*techo*
▭	CAJA DE REGISTRO OVAL TIPO C (DOS SALIDAS) P/ TUBO CONDUIT DE 20mm DE MATERIAL ALUMINIO NYECTADO A PRESION, CON TAPA DE LAMINA DE ALUMINIO Y EMPAQUE, TORNILLOS DE GALVANIZADO.	*techo*
▭	CAJA DE REGISTRO OVAL TIPO X (CUATRO SALIDAS) P/ TUBO CONDUIT DE 20mm DE MATERIAL ALUMINIO NYECTADO A PRESION, CON TAPA DE LAMINA DE ALUMINIO Y EMPAQUE, TORNILLOS DE GALVANIZADO.	*techo*
▯ ▭	CAJA DE REGISTRO OVAL TIPO T (TRES SALIDAS) P/ TUBO CONDUIT DE 20mm DE MATERIAL ALUMINIO NYECTADO A PRESION, CON TAPA DE LAMINA DE ALUMINIO Y EMPAQUE, TORNILLOS DE GALVANIZADO.	*techo*
•	PULSADOR CONMUTADO SIMPLE, DOBLE, TRIPLE.	*1.20m pared*
▭	ARTEFACTO PARA ALUMBRADO DE EMERGENCIA CON 02 FOCOS LED DE ALTA POTENCIA DE 2x18W, 220V, 60Hz, 4000LM, MODELO KC 2000 LED, SIMILAR A KOLFF.	--

RECTOR:
DR.PAULINO MACHACA ARI
VICERECTOR ACADEMICO:
DR. MARIO S. CUENTAS ALVARADO
VICERECTOR DE INVESTIGACION:
DR. ARIEL VELAZCO CARDENAS

U.E.I
UNIDAD EJECUTORA
DE INVERSIONES

SUB-UNIDAD
DE ESTUDIOS

UNIDAD EJECUTORA
DE INVERSIONES

JEFE UNIDAD EJECUTORA DE INVERSIONES:
ING. WILBER F. CAYRO ROJAS
JEFE SUB UNIDAD DE ESTUDIOS:
ING. ANDRES A. QUIZA AÑAZCO

ESPECIALIDAD:
INSTALACIONES ELECTRICAS

PLANO:
ILUMINACIÓN QUINTO NIVEL

PROYECTO:
"MEJORAMIENTO DE LA GESTIÓN INSTITUCIONAL EN EDUCACIÓN UNIVERSITARIA DE LOS SERVICIOS ADMINISTRATIVOS DE LA UNIVERSIDAD NACIONAL DEL ALTIPLANO, DISTRITO DE PUNO -PROVINCIA DE PUNO - DEPARTAMENTO DE PUNO"

COMPONENTE:
"ADECUADA Y SUFICIENTE INFRAESTRUCTURA PARA LABOR ADMINISTRATIVA EN LA UNIVERSIDAD"

DESARROLLO PROYECTO INSTALACIONES ELÉCTRICAS:
ING. ANTERO NEFTALI AJROTA MAQUERA

LOCALIZACION:
BARRIO BELLAVISTA
AV. EL SOL N° 329

UBICACION:
DPTO. PUNO
PROV. PUNO
DISTR. PUNO

DIBUJO:
SUB UNIDAD DE ESTUDIOS

FECHA:
FEBRERO 2023

ESCALA:
INDICADA

LAMINA:
IE-IL5